




ОСНОВЕН ПРОЕКТ

За

Изградба на атмосферска канализација по улици
Ордан Поп Јорданов, Ордан Пиперката и Иван Наумов
Алабакот, Маџари 1, Урбан блок 1, Општина Гази Баба

Техн. бр. 074 / 2021 – К

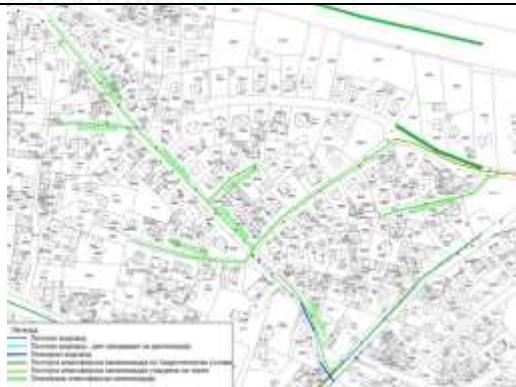

Инвеститор: ОПШТИНА ГАЗИ БАБА

Објект: Изградба на атмосферска канализација по улици Ордан
Поп Јорданов, Ордан Пиперката и Иван Наумов Алабакот,
Маџари 1, Урбан блок 1, Општина Гази Баба


Место: Општина Гази Баба


Ниво на проект: Основен проект

Ознака: Водовод и канализација (ВК)


Дата: Јануари, 2023

ФАЗА: | ВК |

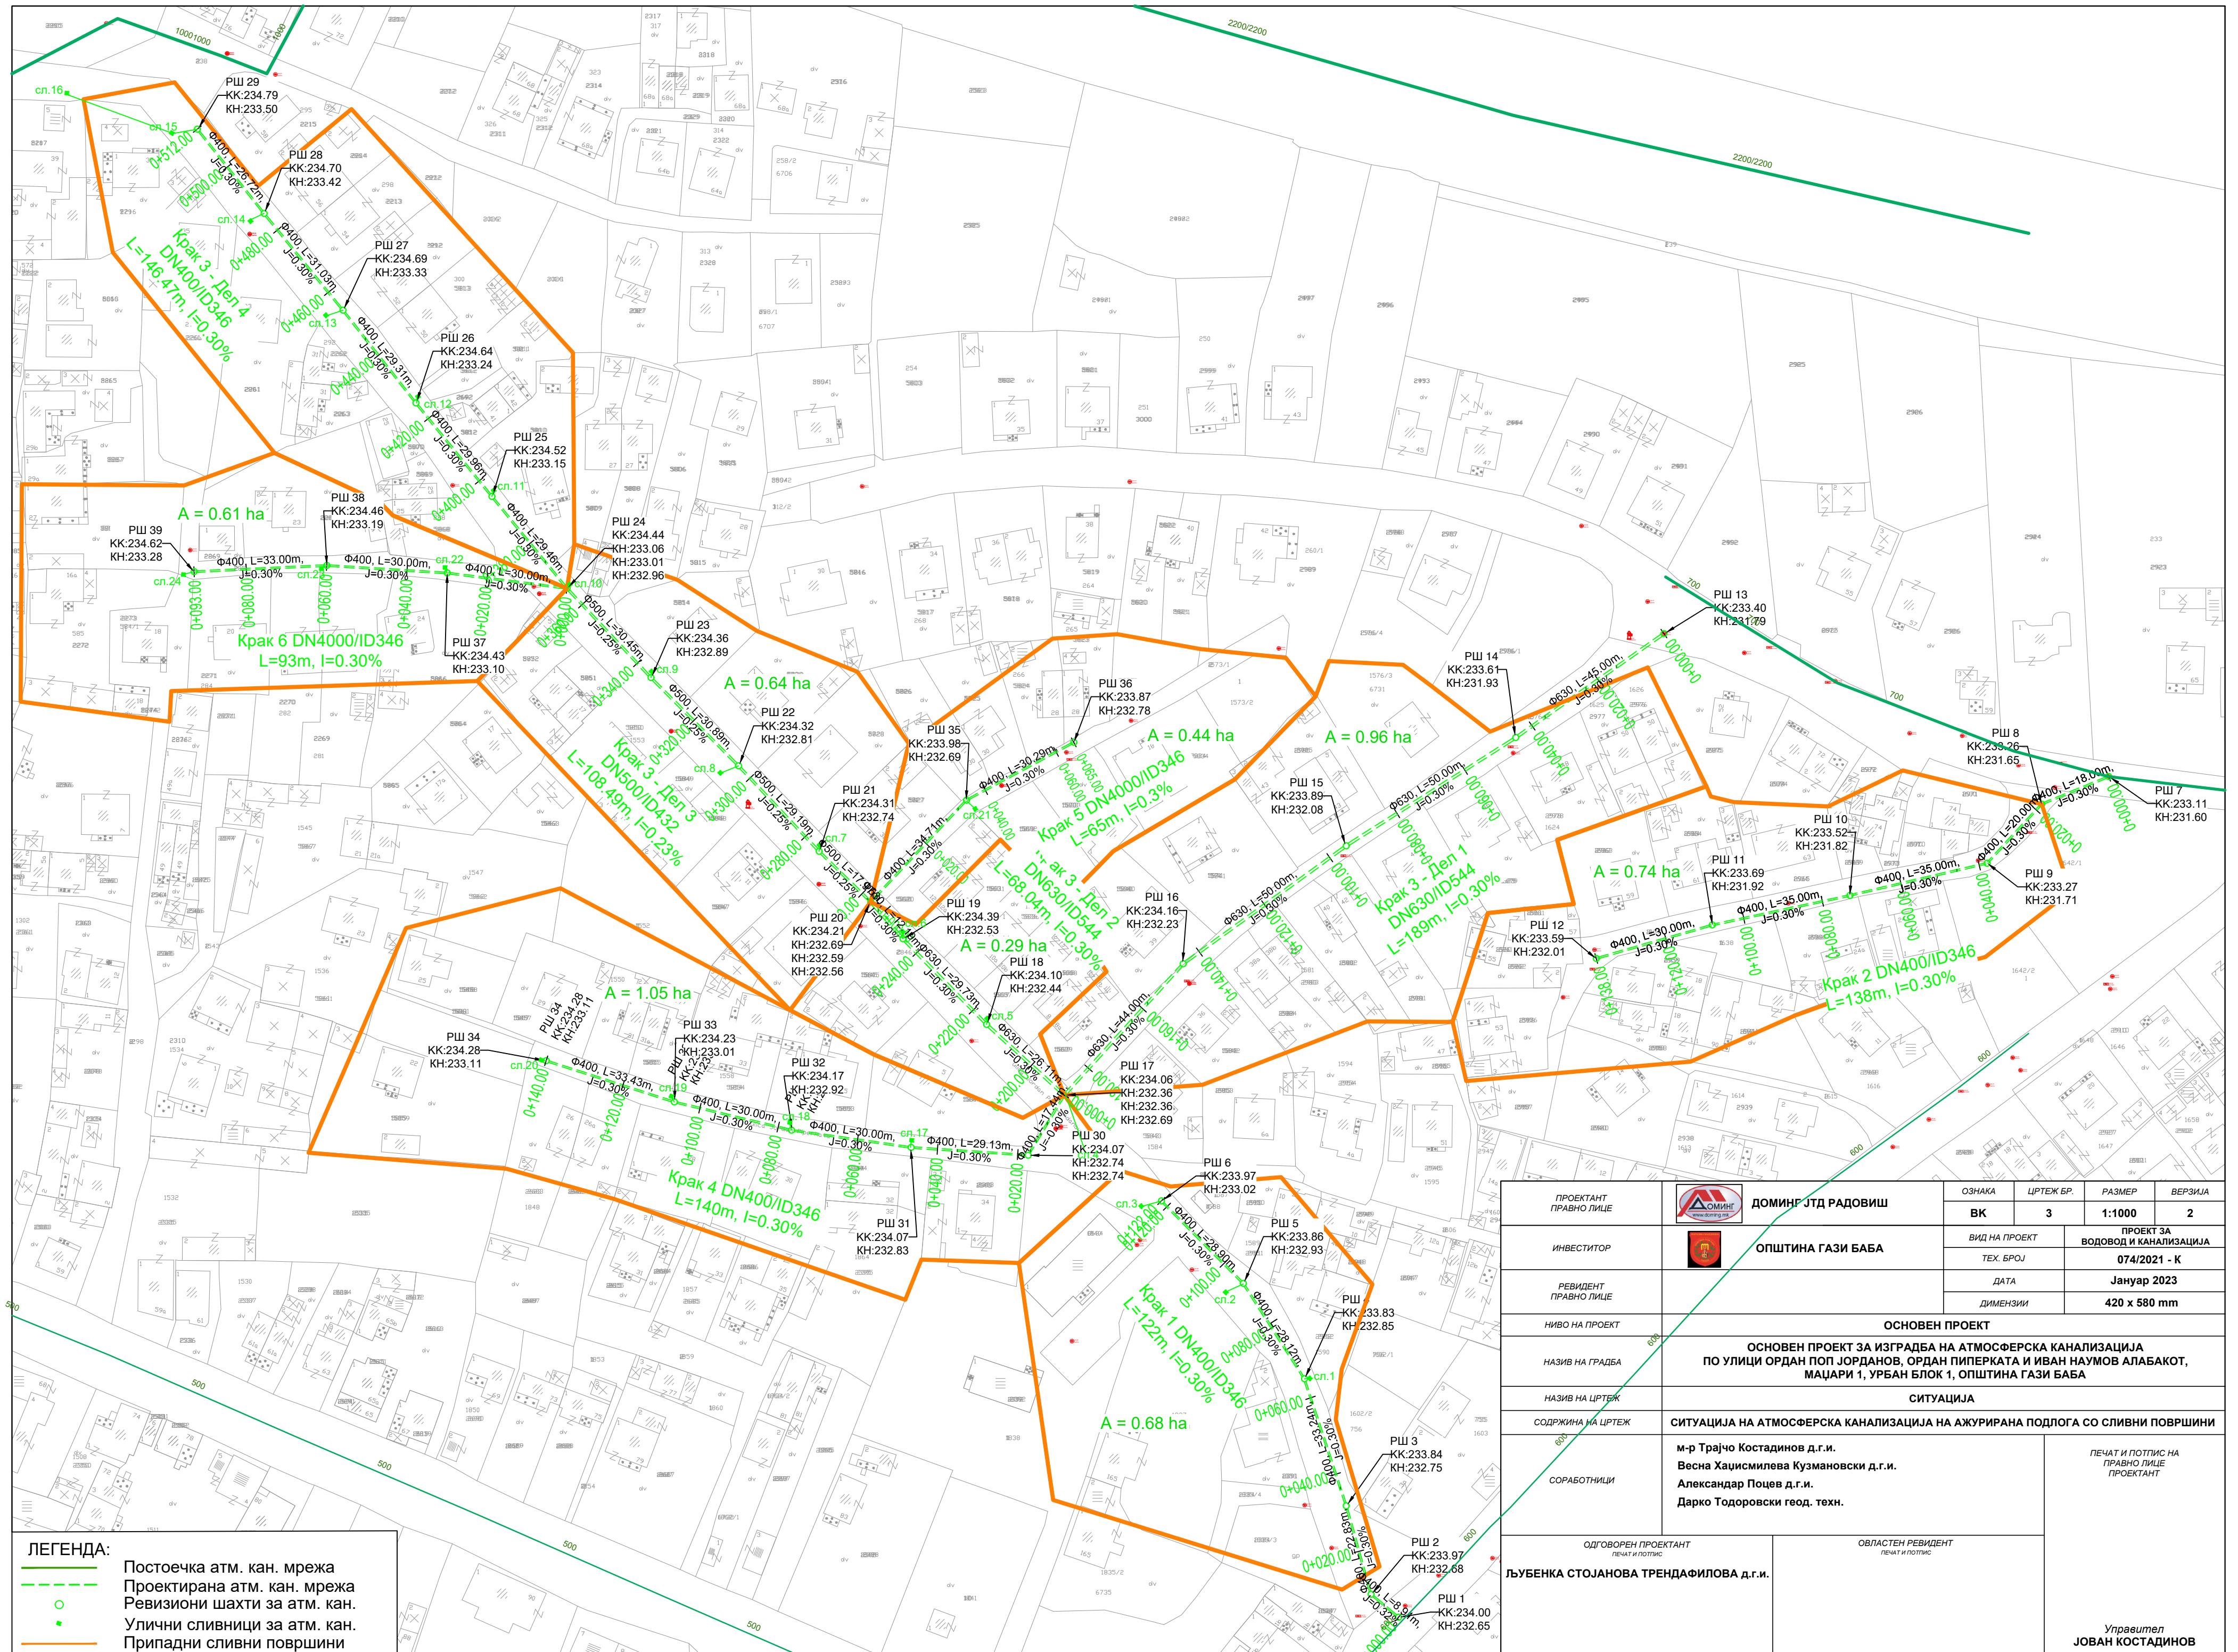


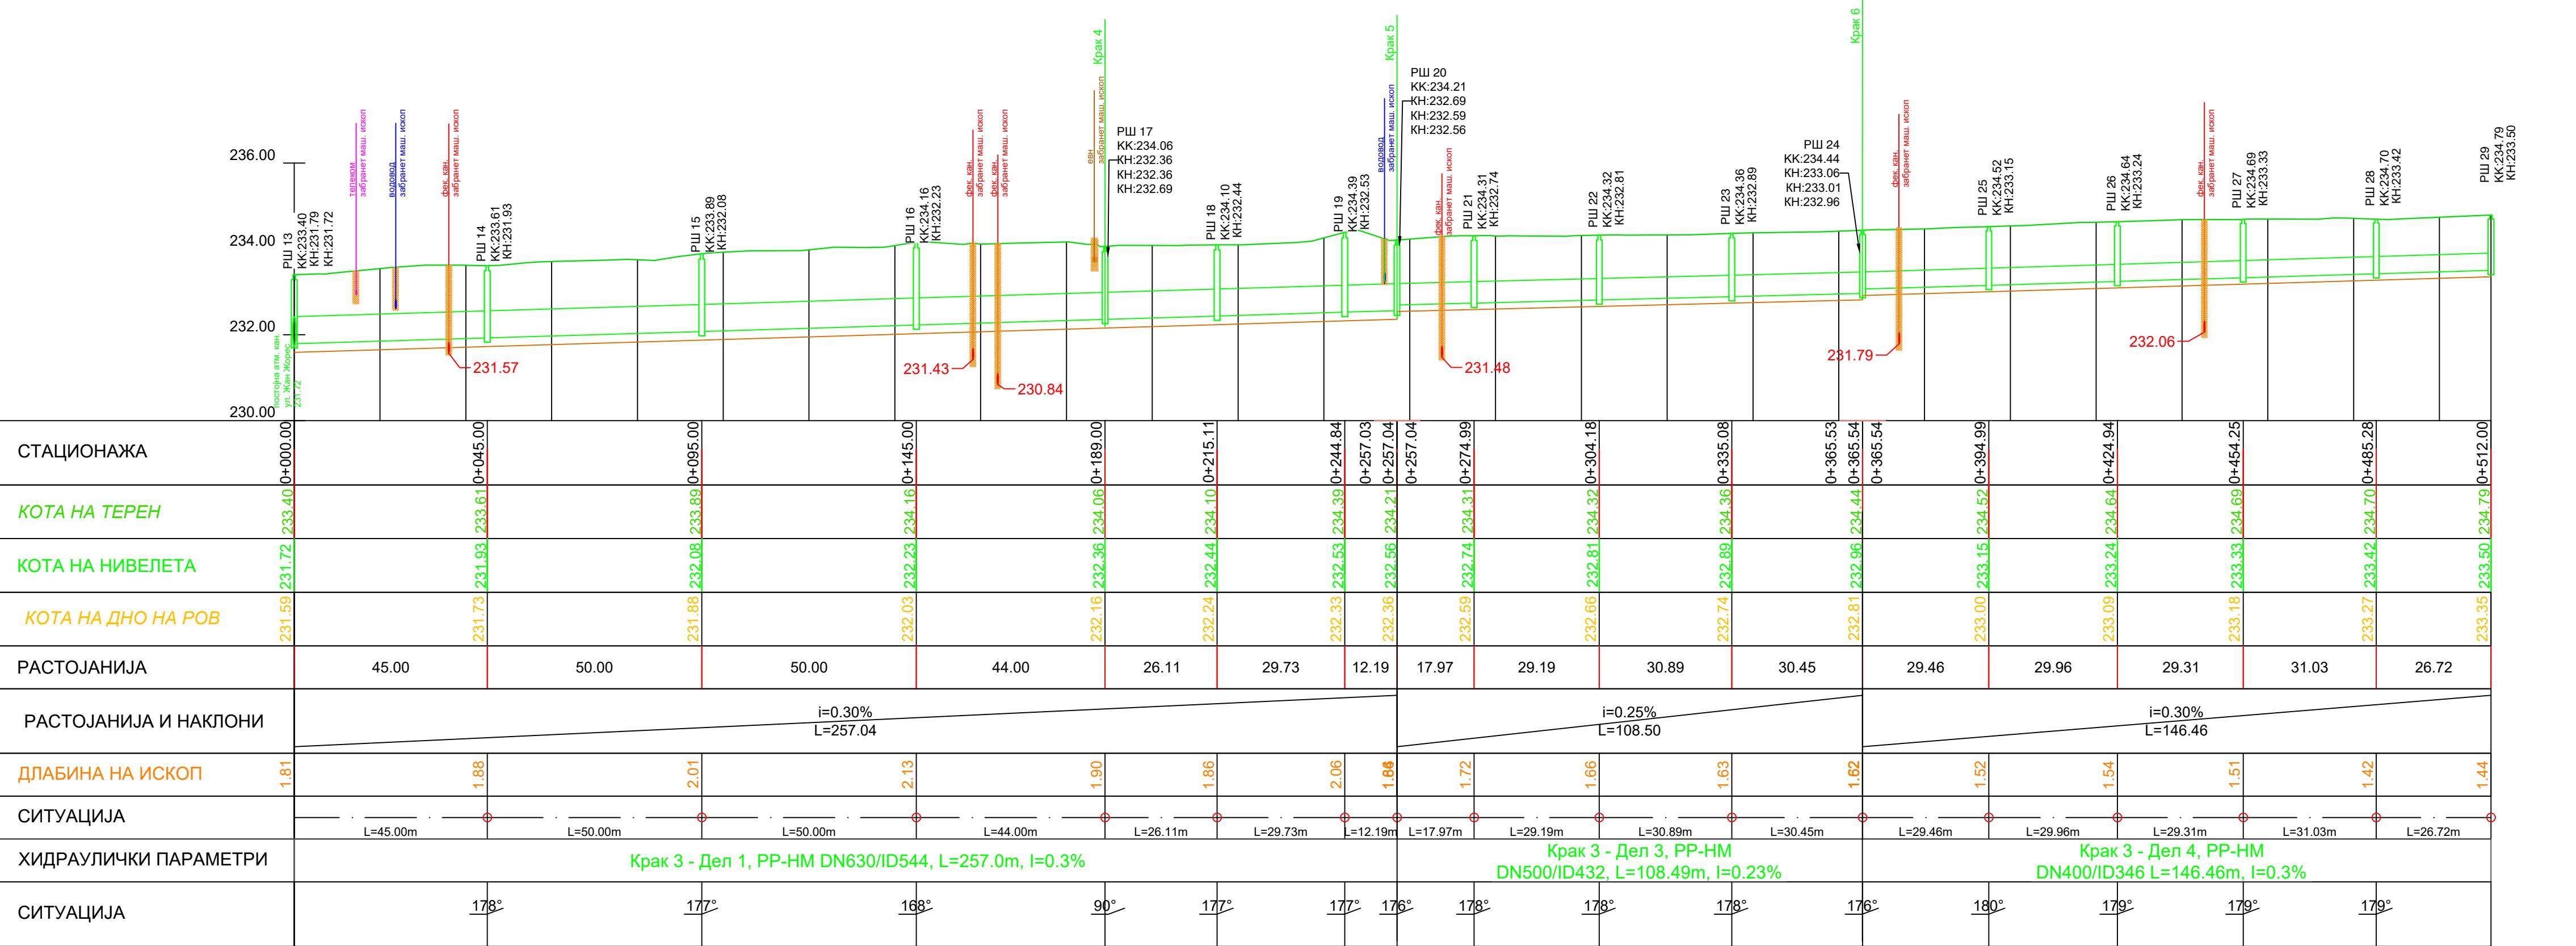

ПРОЕКТАНТ ПРАВНО ЛИЦЕ	ДОМИНГ ЈТД РАДОВИШ	ОЗНАКА	ЦРТЕЖ БР.	РАЗМЕР	ВЕРЗИЈА
		ВК	4.3	1:100/1000	2
ИНВЕСТИТОР	ОПШТИНА ГАЗИ БАБА	ВИД НА ПРОЕКТ		ПРОЕКТ ЗА ВОДОВОД И КАНАЛИЗАЦИЈА	
		ТЕХ. БРОЈ	074/2021 - К		
		ДАТА	Јануар 2023		
		ДИМЕНЗИИ	297 x 950 mm		
ОСНОВЕН ПРОЕКТ					
ОСНОВЕН ПРОЕКТ ЗА ИЗГРАДБА АТМОСФЕРСКА КАНАЛИЗАЦИЈА ПО УЛИЦИ ОРДАН ПОП ЈОРДАНОВ, ОРДАН ПИЛКЕРКАТА И ИВАН НАУМОВ АЛАБАКОТ, МАЦАРИ 1, УРБАН БЛОК 1, ОПШТИНА ГАЗИ БАБА					
НАЗИВ НА ГРАДБА		НАДОЛЖЕН ПРОФИЛ			
НАЗИВ НА ЦРТЕЖ		НАДОЛЖЕН ПРОФИЛ НА КРАК 3			
СОДРЖИНА НА ЦРТЕЖ	м-р Трајко Костадинов д.г.и. Весна Хаџимилева Кузмановски д.г.и. Александар Пощев д.г.и. Дарко Тодоровски геод. техн.	НАДОЛЖЕН ПРОФИЛ НА КРАК 3			
СОРАБОТНИЦИ	ПЕЧАТ И ПОПИС НА ПРАВНО ЛИЦЕ ПРОЕКТАНТ				
ОДГОВОРЕН ПРОЕКТАНТ ПЕЧАТ И ПОПИС	ОВЛАСТЕН РЕВИДЕНТ ПЕЧАТ И ПОПИС				
ЉУБЕНКА СТОЈАНОВА ТРЕНДАФИЛОВА д.г.и.					
Управител	ЈОВАН КОСТАДИНОВ				

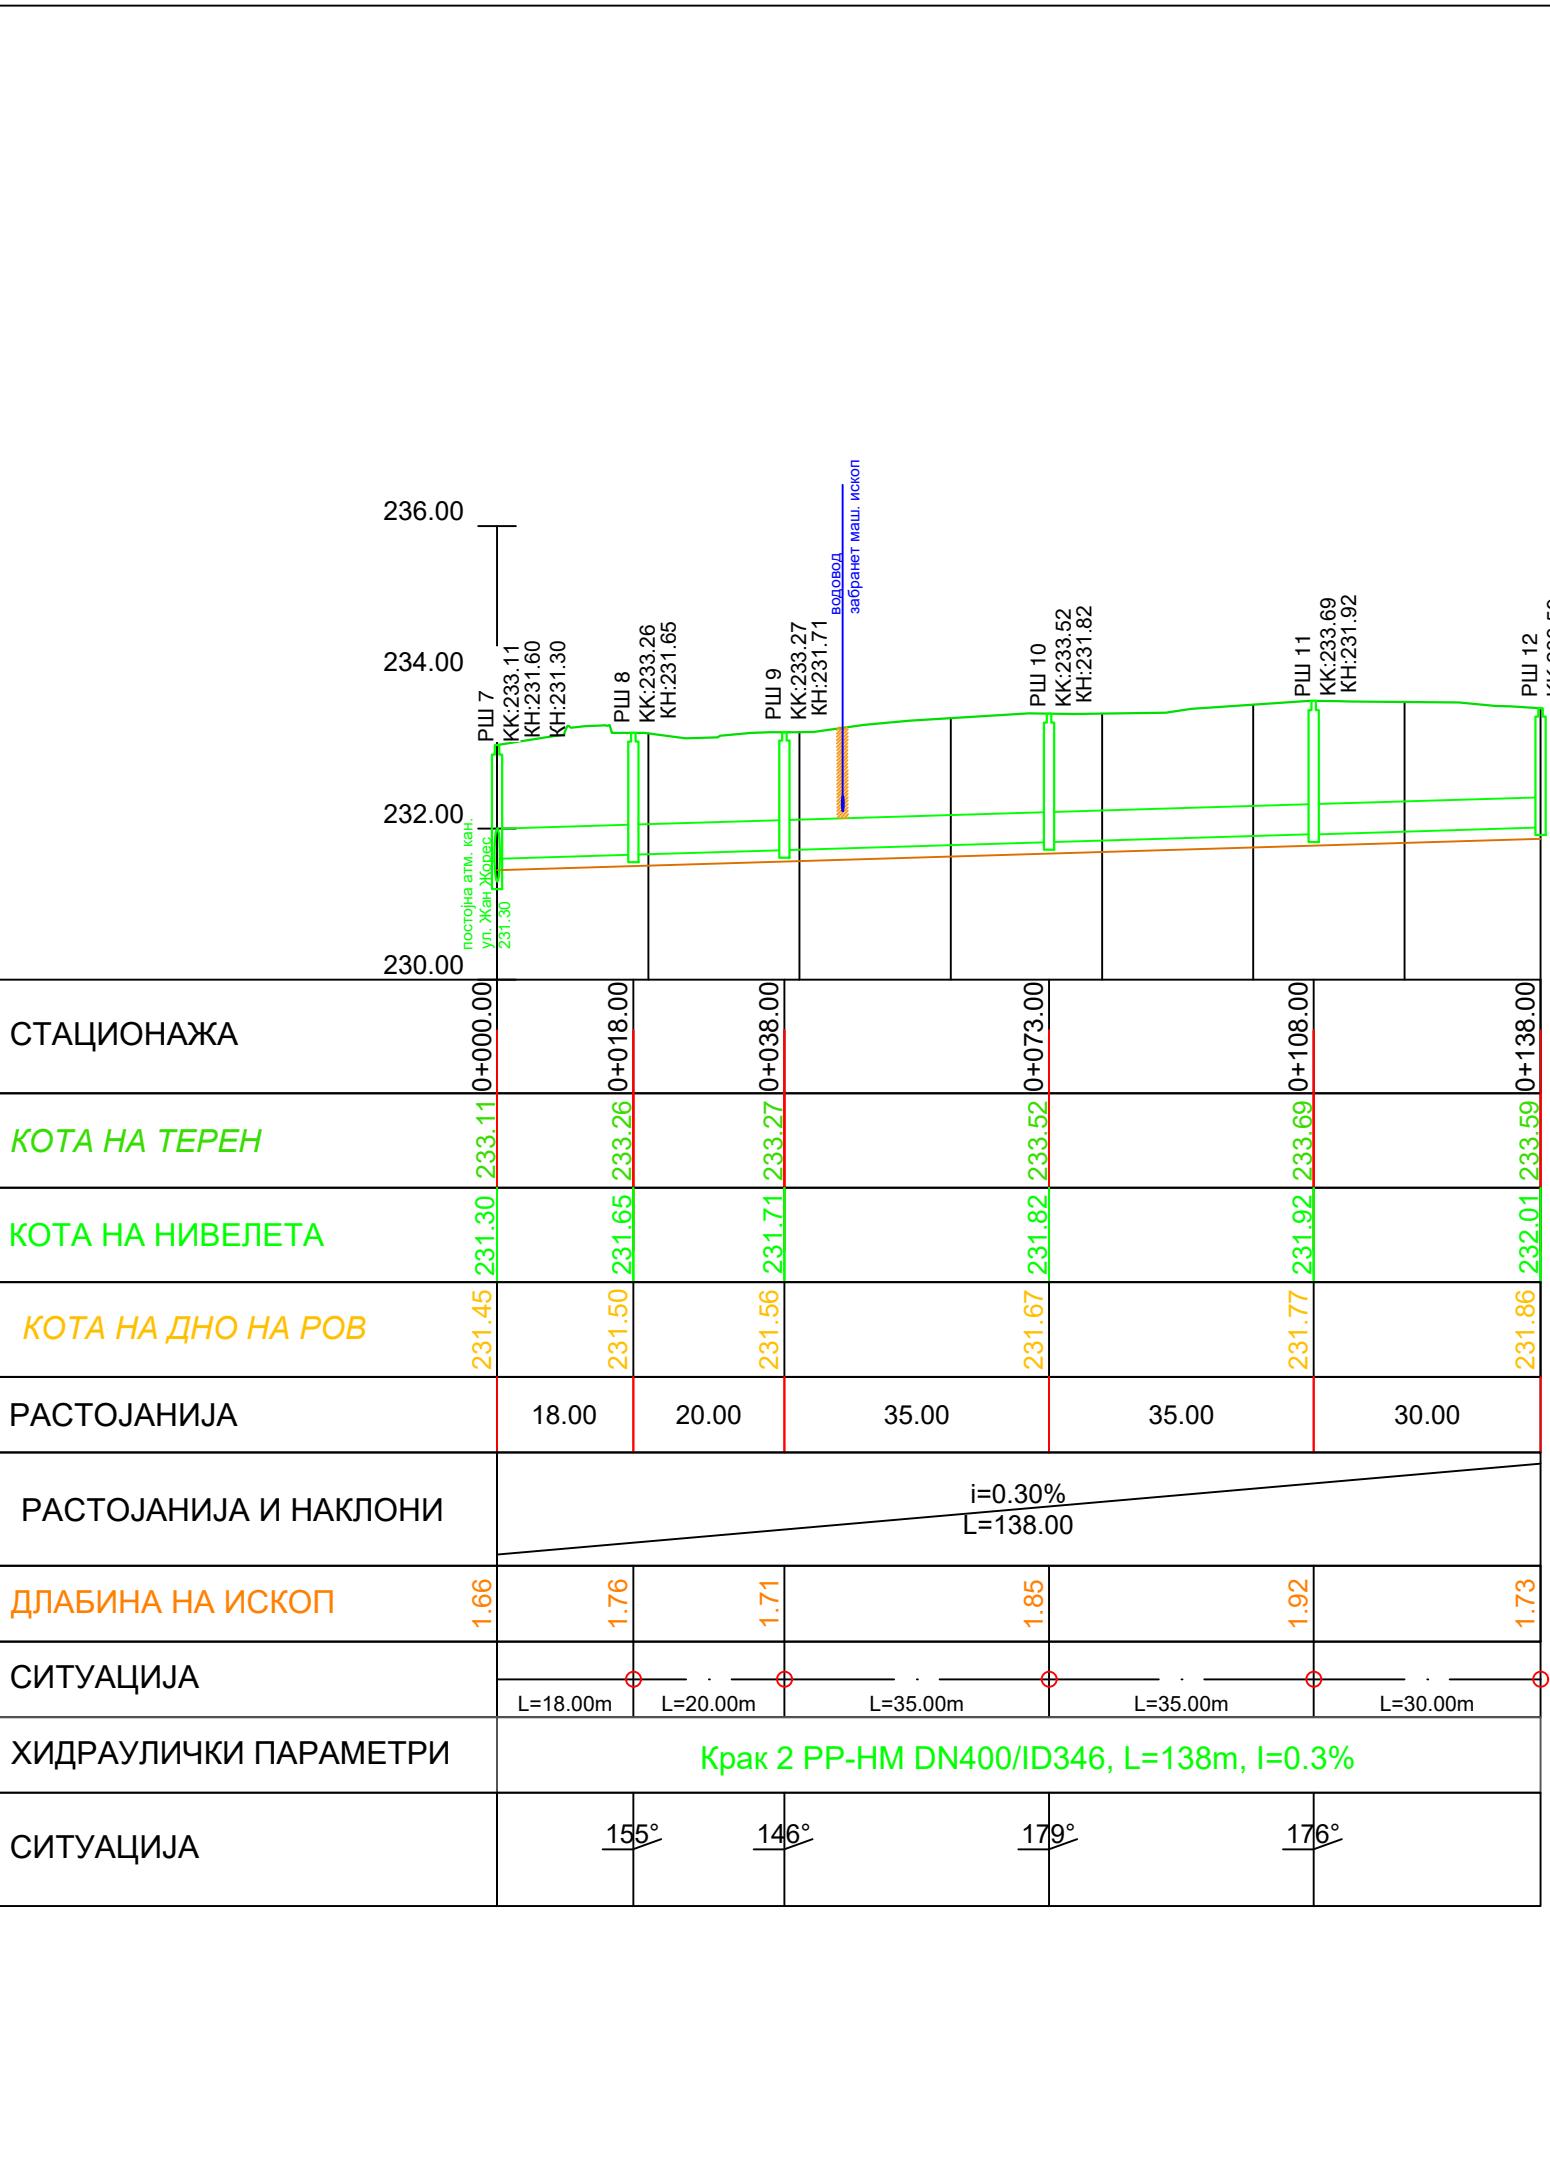


ПРОЕКТАНТ ПРАВНО ЛИЦЕ	 ДОМИНГ ЈТД РАДОВИШ	ОЗНАКА	ЦРТЕЖ БР.	РАЗМЕР	ВЕРЗИЈА
		ВК	4.2	1:100/1000	2
ИНВЕСТИТОР	 ОПШТИНА ГАЗИ БАБА	ПРОЕКТ ЗА ВОДОВОД И КАНАЛИЗАЦИЈА			
		TEX. БРОЈ	074/2021 - К		
РЕВИДЕНТ ПРАВНО ЛИЦЕ		ДАТА	Јануар 2023		
НИВО НА ПРОЕКТ		ДИМЕНЗИИ	297 x 420 mm		
НАЗИВ НА ГРАДБА	ОСНОВЕН ПРОЕКТ				
	ОСНОВЕН ПРОЕКТ ЗА ИЗГРАДБА НА АТМОСФЕРСКА КАНАЛИЗАЦИЈА ПО УЛИЦИ ОРДАН ПОП ЈОРДАНОВ, ОРДАН ПИПЕРКАТА И ИВАН НАУМОВ АЛАБАКОТ, МАЦАРИ 1, УРБАН БЛОК 1, ОПШТИНА ГАЗИ БАБА				
НАЗИВ НА ЦРТЕЖ	НАДОЛЖЕН ПРОФИЛ				
СОДРЖИНА НА ЦРТЕЖ	НАДОЛЖЕН ПРОФИЛ НА КРАК 2				
СОРАБОТНИЦИ	м-р Трајчо Костадинов д.г.и. Весна Хаџисмилева Кузмановски д.г.и. Александар Поцев д.г.и. Дарко Тодоровски геод. техн.				
ОДГОВОРЕН ПРОЕКТАНТ ПЕЧАТ И ПОПСИС	ПЕЧАТ И ПОПСИС НА ПРАВНО ЛИЦЕ ПРОЕКТАНТ				
ЉУБЕНКА СТОЈАНОВА ТРЕНДАФИЛОВА д.г.и.	ОВЛАСТЕН РЕВИДЕНТ ПЕЧАТ И ПОПСИС				
	Управител ЈОВАН КОСТАДИНОВ				

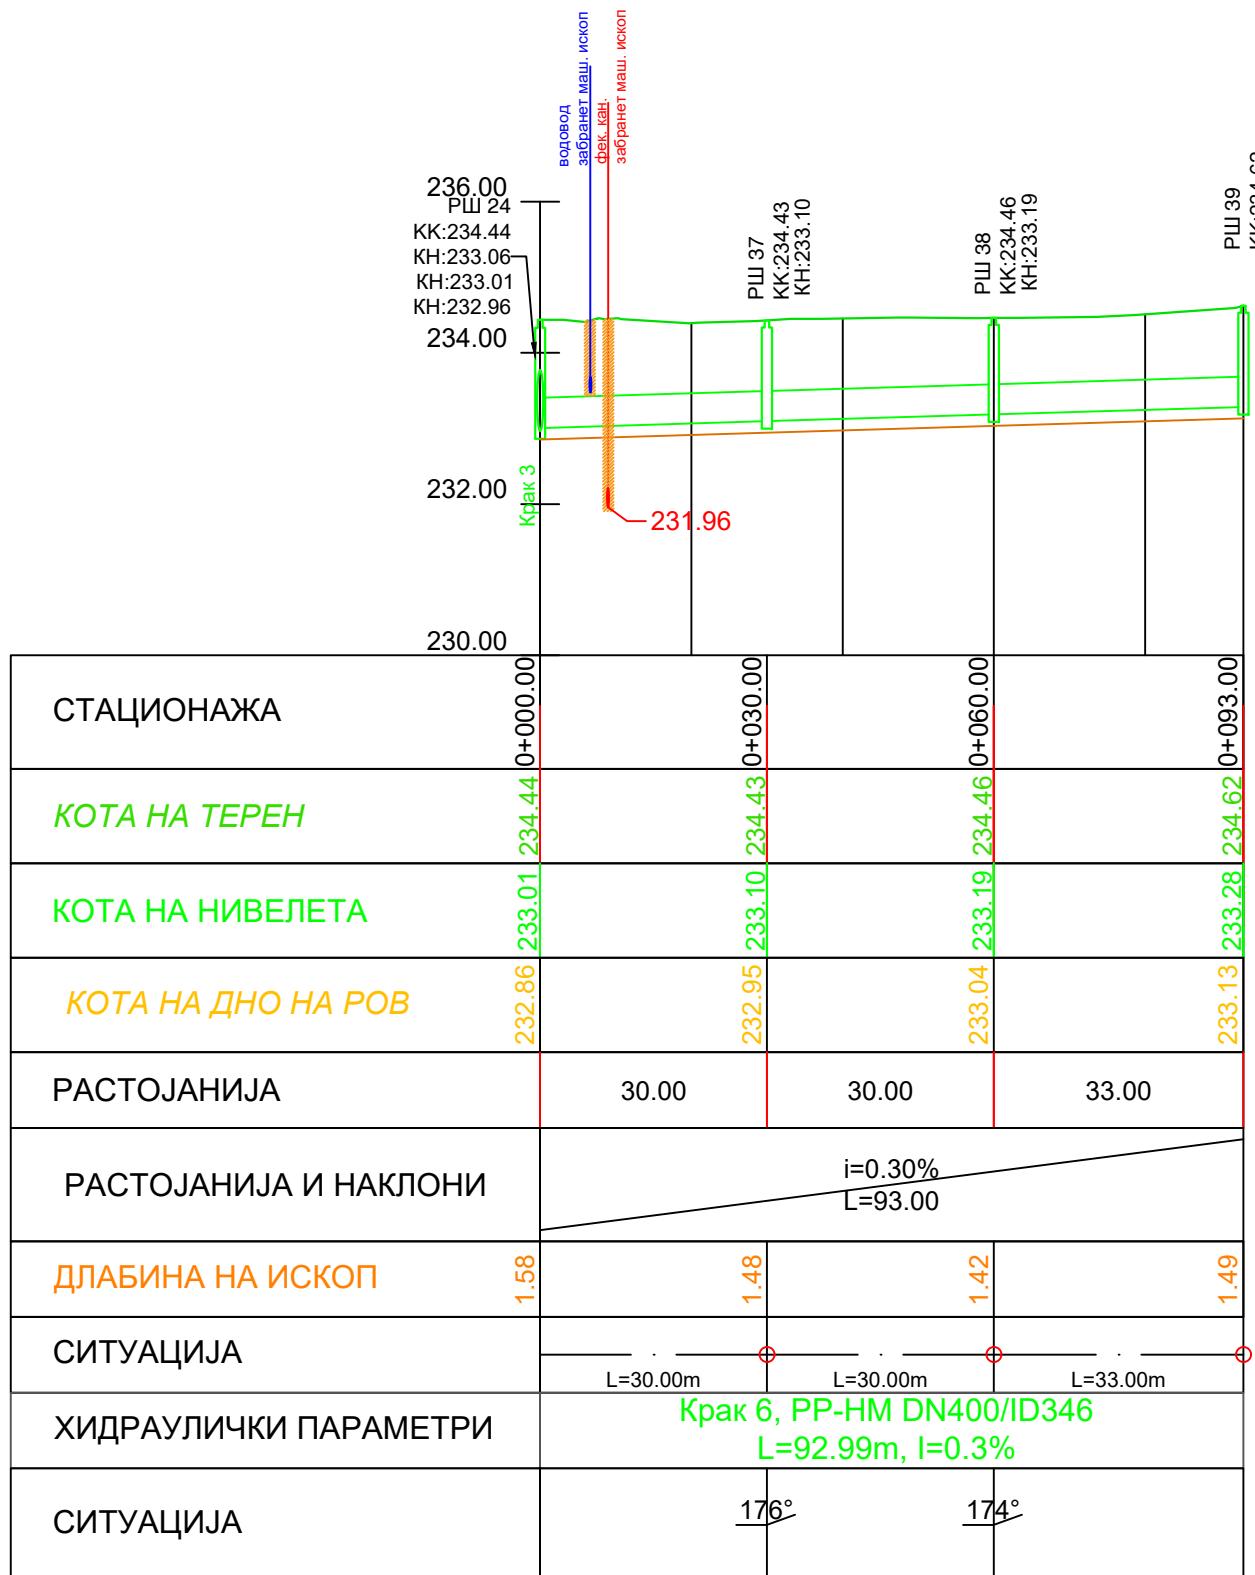


ПРОЕКТАНТ ПРАВНО ЛИЦЕ	 ДОМИНГ ЈТД РАДОВИШ	ОЗНАКА	ЦРТЕЖ БР.	РАЗМЕР	ВЕРЗИЈА
		ВК	4.6	1:100/1000	2
ИНВЕСТИТОР	 ОПШТИНА ГАЗИ БАБА	ПРОЕКТ ЗА ВОДОВОД И КАНАЛИЗАЦИЈА			
		TEX. БРОЈ	074/2021 - К		
РЕВИДЕНТ ПРАВНО ЛИЦЕ		ДАТА	Јануар 2023		
		ДИМЕНЗИИ	297 x 420 mm		
НИВО НА ПРОЕКТ	ОСНОВЕН ПРОЕКТ				
НАЗИВ НА ГРАДБА	ОСНОВЕН ПРОЕКТ ЗА ИЗГРАДБА НА АТМОСФЕРСКА КАНАЛИЗАЦИЈА ПО УЛИЦИ ОРДАН ПОП ЈОРДАНОВ, ОРДАН ПИПЕРКАТА И ИВАН НАУМОВ АЛАБАКОТ, МАЦАРИ 1, УРБАН БЛОК 1, ОПШТИНА ГАЗИ БАБА				
НАЗИВ НА ЦРТЕЖ	НАДОЛЖЕН ПРОФИЛ				
СОДРЖИНА НА ЦРТЕЖ	НАДОЛЖЕН ПРОФИЛ НА КРАК 6				
СОРАБОТНИЦИ	м-р Трајко Костадинов д.г.и. Весна Хаџисмилева Кузмановски д.г.и. Александар Поцев д.г.и. Дарко Тодоровски геод. техн.				
	ПЕЧАТ И ПОТПИС НА ПРАВНО ЛИЦЕ ПРОЕКТАНТ				
ОДГОВОРЕН ПРОЕКТАНТ ПЕЧАТ И ПОТПИС	ОВЛАСТЕН РЕВИДЕНТ ПЕЧАТ И ПОТПИС				
ЉУБЕНКА СТОЈАНОВА ТРЕНДАФИЛОВА д.г.и.					

Управител
ЈОВАН КОСТАДИНОВ

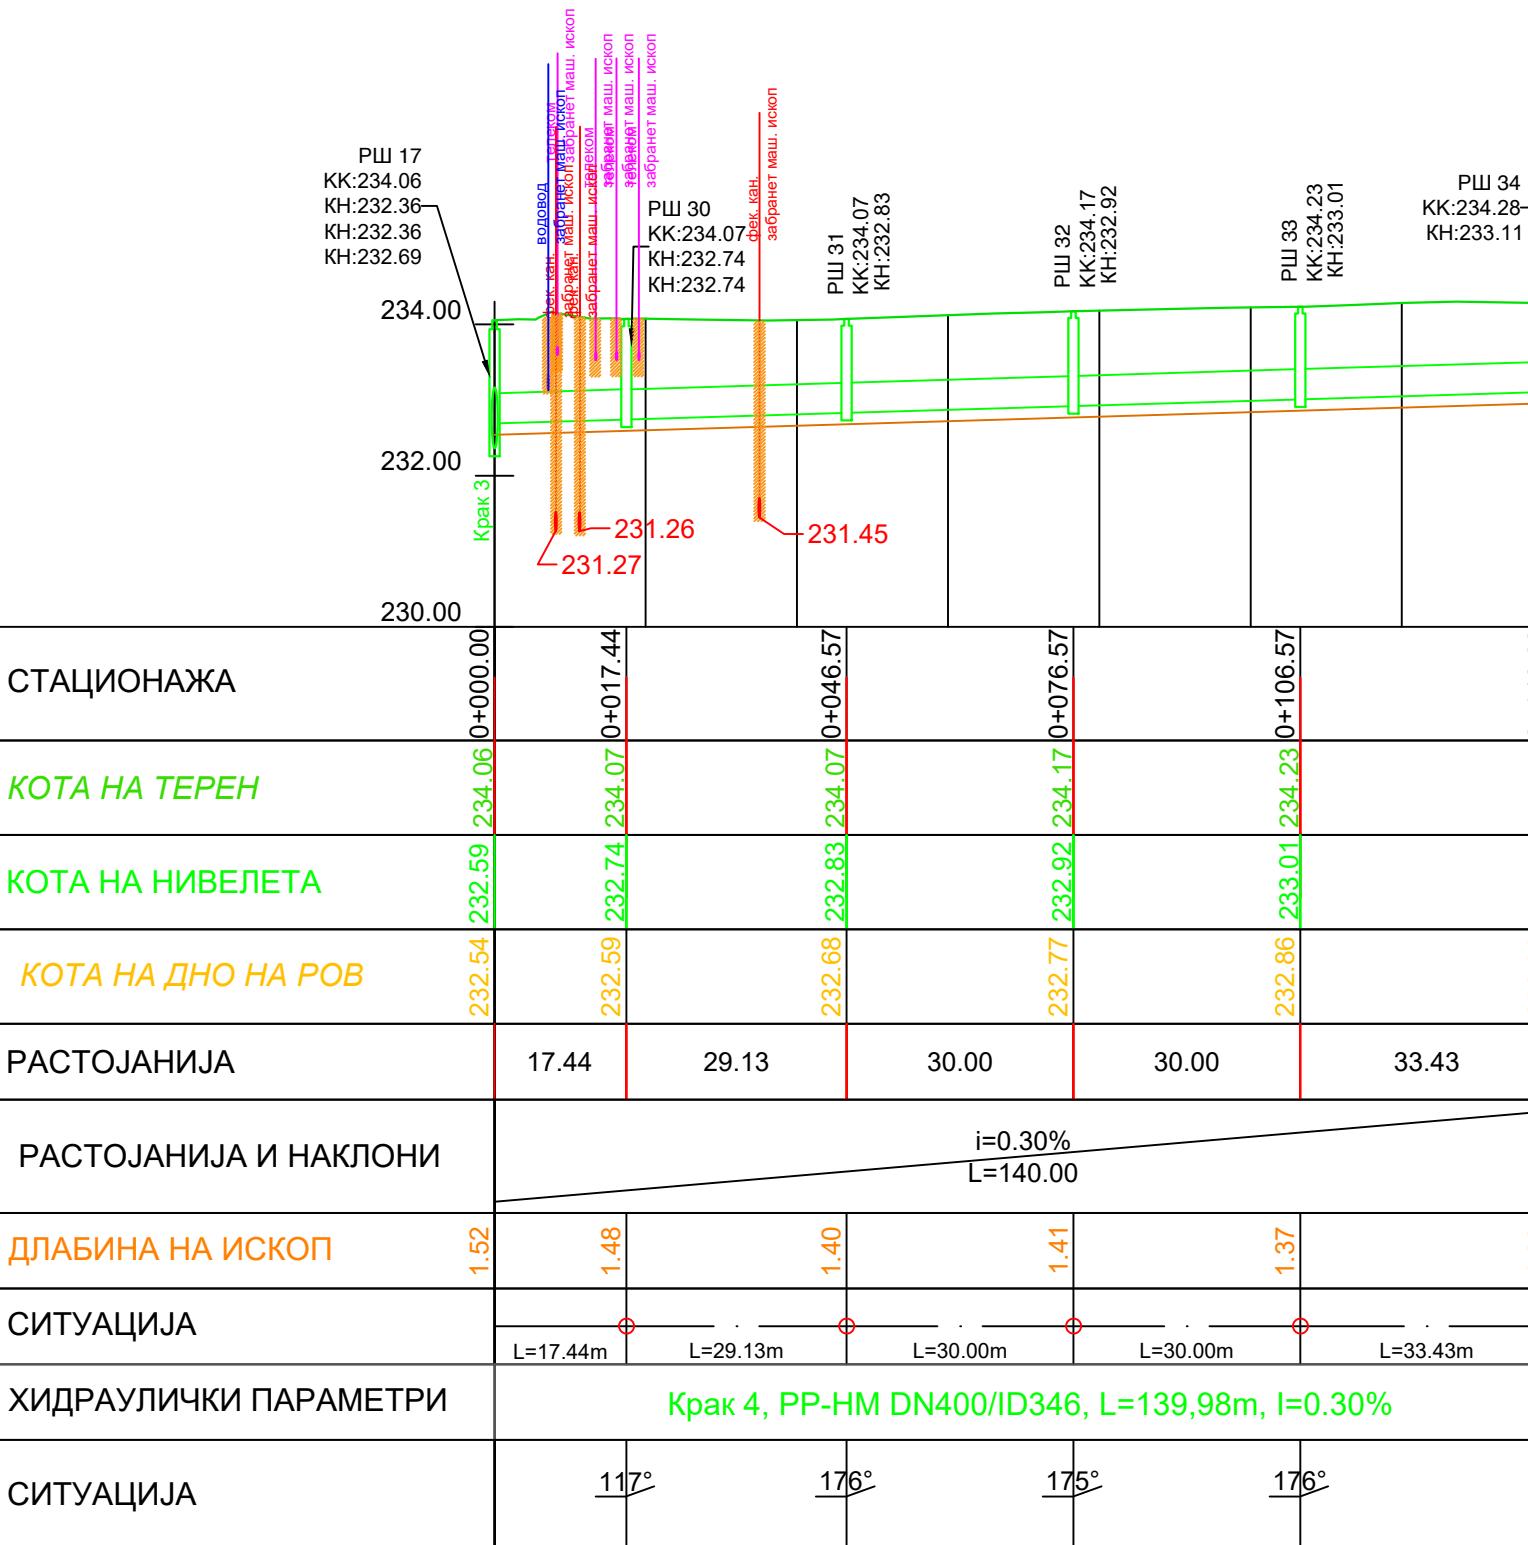


ПРОЕКТАНТ ПРАВНО ЛИЦЕ		ДОМИНГ ЈТД РАДОВИШ	ОЗНАКА	ЦРТЕЖ БР.	РАЗМЕР	ВЕРЗИЈА
			ВК	4.4	1:100/1000	2
ИНВЕСТИТОР		ОПШТИНА ГАЗИ БАБА	ВИД НА ПРОЕКТ	ПРОЕКТ ЗА ВОДОВОД И КАНАЛИЗАЦИЈА		
			TEX. БРОЈ	074/2021 - К		
РЕВИДЕНТ ПРАВНО ЛИЦЕ			ДАТА	Јануар 2023		
			ДИМЕНЗИИ	297 x 420 mm		
НИВО НА ПРОЕКТ	ОСНОВЕН ПРОЕКТ					
НАЗИВ НА ГРАДБА	ОСНОВЕН ПРОЕКТ ЗА ИЗГРАДБА НА АТМОСФЕРСКА КАНАЛИЗАЦИЈА ПО УЛИЦИ ОРДАН ПОП ЈОРДАНОВ, ОРДАН ПИПЕРКАТА И ИВАН НАУМОВ АЛАБАКОТ, МАЦАРИ 1, УРБАН БЛОК 1, ОПШТИНА ГАЗИ БАБА					
НАЗИВ НА ЦРТЕЖ	НАДОЛЖЕН ПРОФИЛ					
СОДРЖИНА НА ЦРТЕЖ	НАДОЛЖЕН ПРОФИЛ НА КРАК 4					
СОРАБОТНИЦИ	м-р Трајко Костадинов д.г.и. Весна Хаџисмилева Кузмановски д.г.и. Александар Поцев д.г.и. Дарко Тодоровски геод. техн.				ПЕЧАТ И ПОТПИС НА ПРАВНО ЛИЦЕ ПРОЕКТАНТ	
ОДГОВОРЕН ПРОЕКТАНТ ПЕЧАТ И ПОТПИС	ЛЪУБЕНКА СТОЈАНОВА ТRENДАФИЛОВА д.г.и.		ОВЛАСТЕН РЕВИДЕНТ ПЕЧАТ И ПОТПИС			

Управител
ДОВАН КОСТАДИНОВ

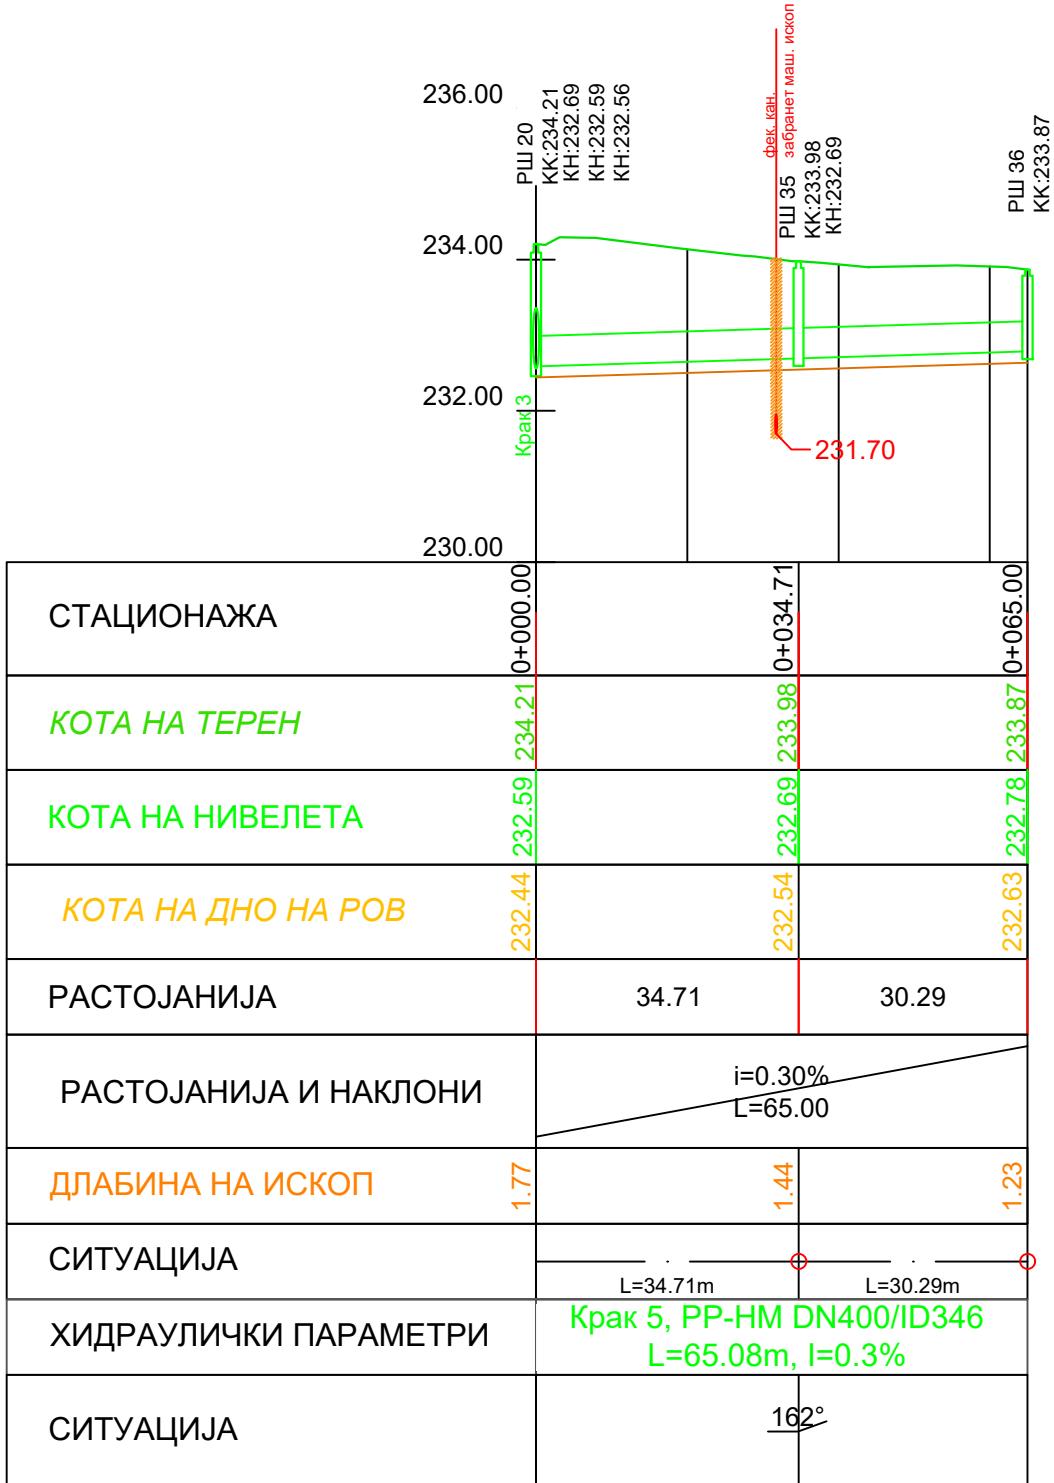


ПРОЕКТАНТ ПРАВНО ЛИЦЕ	 ДОМИНГ ЈТД РАДОВИШ	ОЗНАКА	ЦРТЕЖ БР.	РАЗМЕР	ВЕРЗИЈА
		ВК	4.5	1:100/1000	2
ИНВЕСТИТОР		ПРОЕКТ ЗА ВОДОВОД И КАНАЛИЗАЦИЈА	ВИД НА ПРОЕКТ	074/2021 - К	
РЕВИДЕНТ ПРАВНО ЛИЦЕ		ТЕХ. БРОЈ	ДАТА	Јануар 2023	
НИВО НА ПРОЕКТ			ДИМЕНЗИИ	297 x 420 mm	
НАЗИВ НА ГРАДБА	ОСНОВЕН ПРОЕКТ				
	ОСНОВЕН ПРОЕКТ ЗА ИЗГРАДБА НА АТМОСФЕРСКА КАНАЛИЗАЦИЈА ПО УЛИЦИ ОРДАН ПОП ЈОРДАНОВ, ОРДАН ПИПЕРКАТА И ИВАН НАУМОВ АЛАБАКОТ, МАЦАРИ 1, УРБАН БЛОК 1, ОПШТИНА ГАЗИ БАБА				
НАЗИВ НА ЦРТЕЖ	НАДОЛЖЕН ПРОФИЛ				
СОДРЖИНА НА ЦРТЕЖ	НАДОЛЖЕН ПРОФИЛ НА КРАК 5				
СОРАБОТНИЦИ	м-р Трајко Костадинов д.г.и. Весна Хаџисмилева Кузмановски д.г.и. Александар Поцев д.г.и. Дарко Тодоровски геод. техн.				
	ПЕЧАТ И ПОТПИС НА ПРАВНО ЛИЦЕ ПРОЕКТАНТ				
ОДГОВОРЕН ПРОЕКТАНТ ПЕЧАТ И ПОТПИС	ОВЛАСТЕН РЕВИДЕНТ ПЕЧАТ И ПОТПИС				
ЉУБЕНКА СТОЈАНОВА ТРЕНДАФИЛОВА д.г.и.					

Управител
ЈОВАН КОСТАДИНОВ

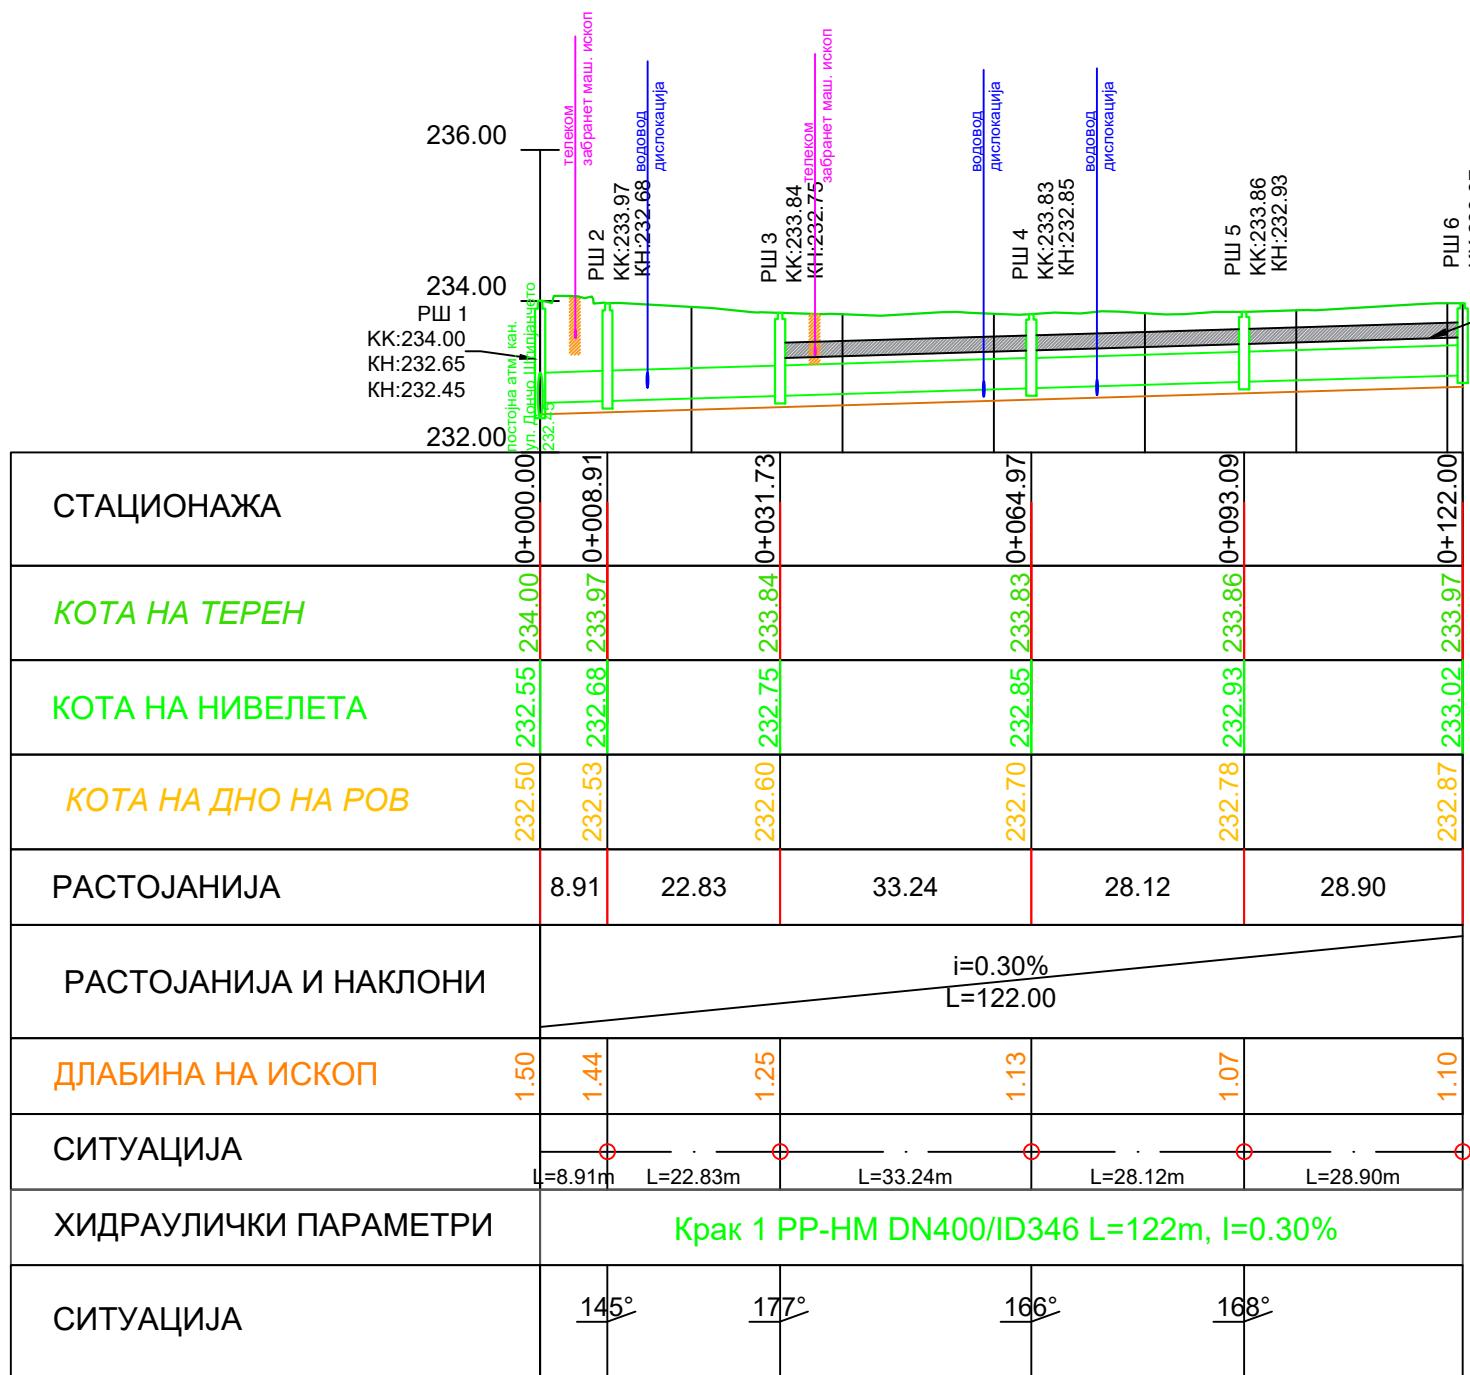


предвидена заштита
во форма на потковица
над новопроектирана цевка


ПРОЕКТАНТ ПРАВНО ЛИЦЕ	ДОМИНГ ЈТД РАДОВИШ 	ОЗНАКА	ЦРТЕЖ БР.	РАЗМЕР	ВЕРЗИЈА
		ВК	4.1	1:100/1000	2
ИНВЕСТИТОР		ПРОЕКТ ЗА ВОДОВОД И КАНАЛИЗАЦИЈА			
		ТЕХ. БРОЈ	074/2021 - К		
РЕВИДЕНТ ПРАВНО ЛИЦЕ		ДАТА	Јануар 2023		
		ДИМЕНЗИИ	297 x 420 mm		
НИВО НА ПРОЕКТ	ОСНОВЕН ПРОЕКТ				
НАЗИВ НА ГРАДБА	ОСНОВЕН ПРОЕКТ ЗА ИЗГРАДБА НА АТМОСФЕРСКА КАНАЛИЗАЦИЈА ПО УЛИЦИ ОРДАН ПОП ЈОРДАНОВ, ОРДАН ПИПЕРКАТА И ИВАН НАУМОВ АЛАБАКОТ, МАЦАРИ 1, УРБАН БЛОК 1, ОПШТИНА ГАЗИ БАБА				
НАЗИВ НА ЦРТЕЖ	НАДОЛЖЕН ПРОФИЛ				
СОДРЖИНА НА ЦРТЕЖ	НАДОЛЖЕН ПРОФИЛ НА КРАК 1				
СОРАБОТНИЦИ	м-р Трајко Костадинов д.г.и. Весна Хаџисмилева Кузмановски д.г.и. Александар Поцев д.г.и. Дарко Тодоровски геод. техн.				
	ПЕЧАТ И ПОТПИС НА ПРАВНО ЛИЦЕ ПРОЕКТАНТ				
ОДГОВОРЕН ПРОЕКТАНТ ПЕЧАТ И ПОТПИС	ОВЛАСТЕН РЕВИДЕНТ ПЕЧАТ И ПОТПИС				
ЉУБЕНКА СТОЈАНОВА ТРЕНДАФИЛОВА д.г.и.					

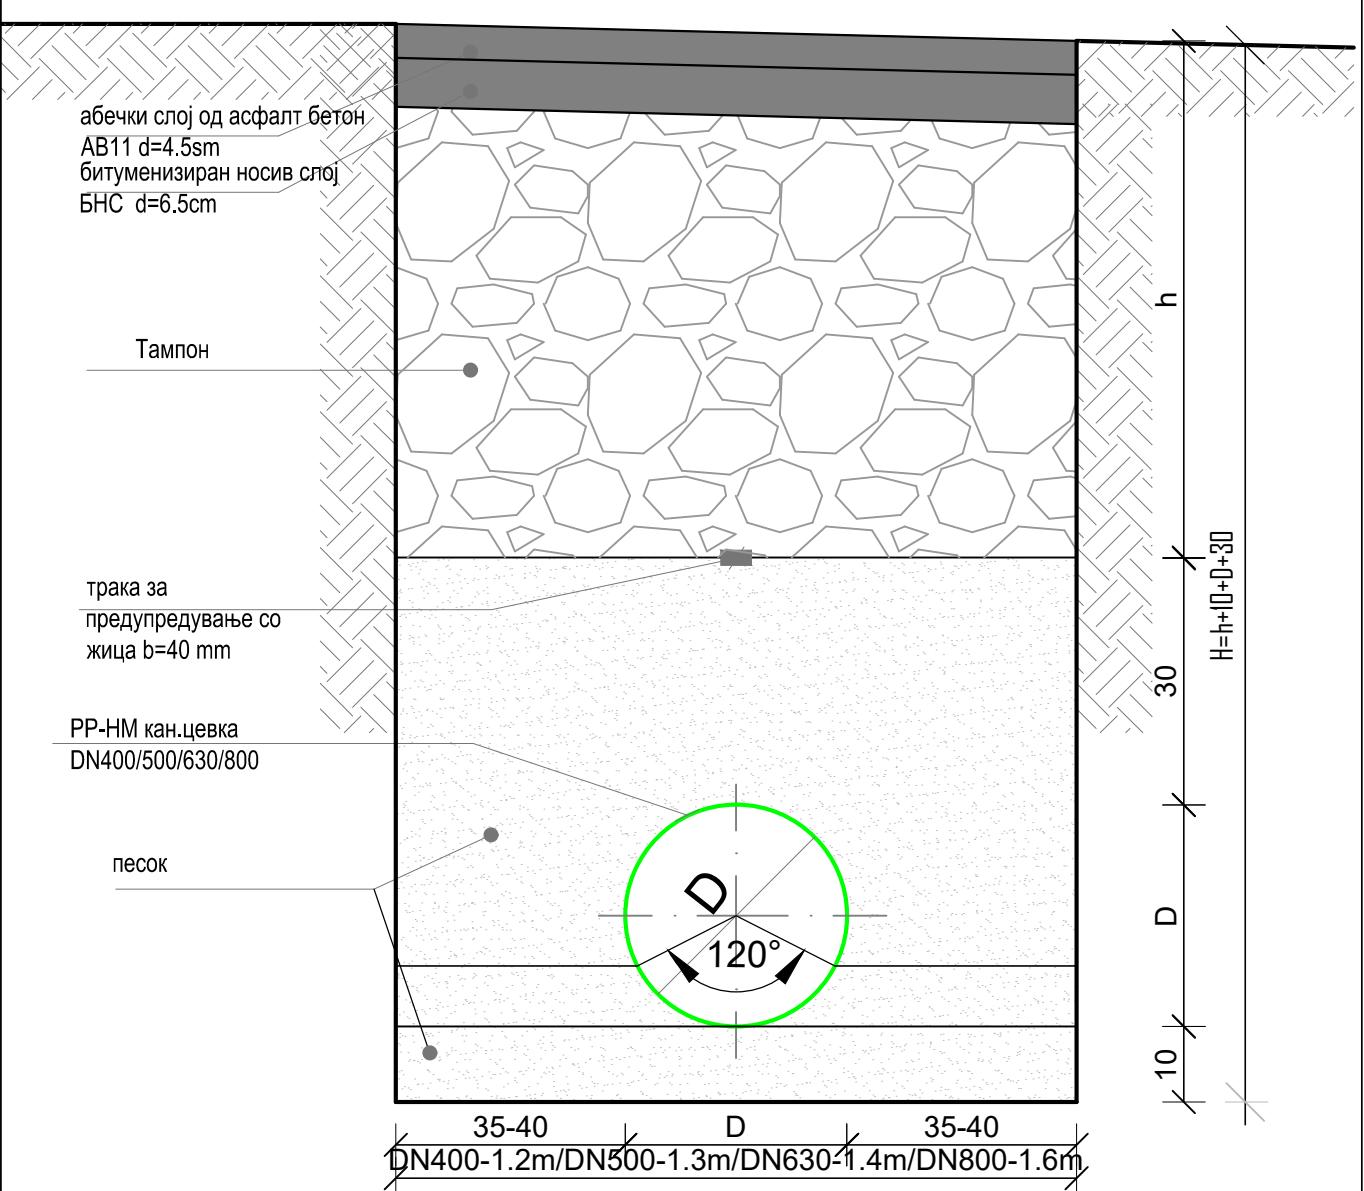





ПРОЕКТАНТ ПРАВНО ЛИЦЕ	 ДОМИНИГ ЈТД РАДОВИШ	ОЗНАКА	ЦРТЕЖ БР.	РАЗМЕР	ВЕРЗИЈА		
		ВК	7	1:10	2		
ИНВЕСТИТОР		ВИД НА ПРОЕКТ	ПРОЕКТ ЗА ВОДОВОД И КАНАЛИЗАЦИЈА				
		ТЕХ. БРОЈ	074/2021 - К				
РЕВИДЕНТ ПРАВНО ЛИЦЕ		ДАТА	Јануари 2023				
		ДИМЕНЗИИ	297 x 210 mm				
НИВО НА ПРОЕКТ	ОСНОВЕН ПРОЕКТ						
НАЗИВ НА ГРАДБА	ОСНОВЕН ПРОЕКТ ЗА ИЗГРАДБА НА АТМОСФЕРСКА КАНАЛИЗАЦИЈА ПО УЛИЦИ ОРДАН ПОП ЈОРДАНОВ, ОРДАН ПИПЕРКАТА И ИВАН НАУМОВ АЛАБАКОТ, МАЦАРИ 1, УРБАН БЛОК 1, ОПШТИНА ГАЗИ БАБА						
НАЗИВ НА ЦРТЕЖ	ДЕТАЛИ						
СОДРЖИНА НА ЦРТЕЖ	ДЕТАЛ НА ТИПСКИ ПОПРЕЧЕН ПРЕСЕК НА РОВ ЗА КАНАЛИЗАЦИЈА НА АСФАЛТ						
СОРАБОТНИЦИ	м-р Трајко Костадинов д.г.и. Весна Хаџисмилева Кузмановски д.г.и. Александар Поцев д.г.и. Дарко Тодоровски геод. техн.			ПЕЧАТ И ПОТПИС НА ПРАВНО ЛИЦЕ ПРОЕКТАНТ			
ОДГОВОРЕН ПРОЕКТАНТ ПЕЧАТ И ПОТПИС	ОВЛАСТЕН РЕВИДЕНТ ПЕЧАТ И ПОТПИС						
ЉУБЕНКА СТОЈАНОВА ТРЕНДАФИЛОВА д.г.и.			Управител ЈОВАН КОСТАДИНОВ				

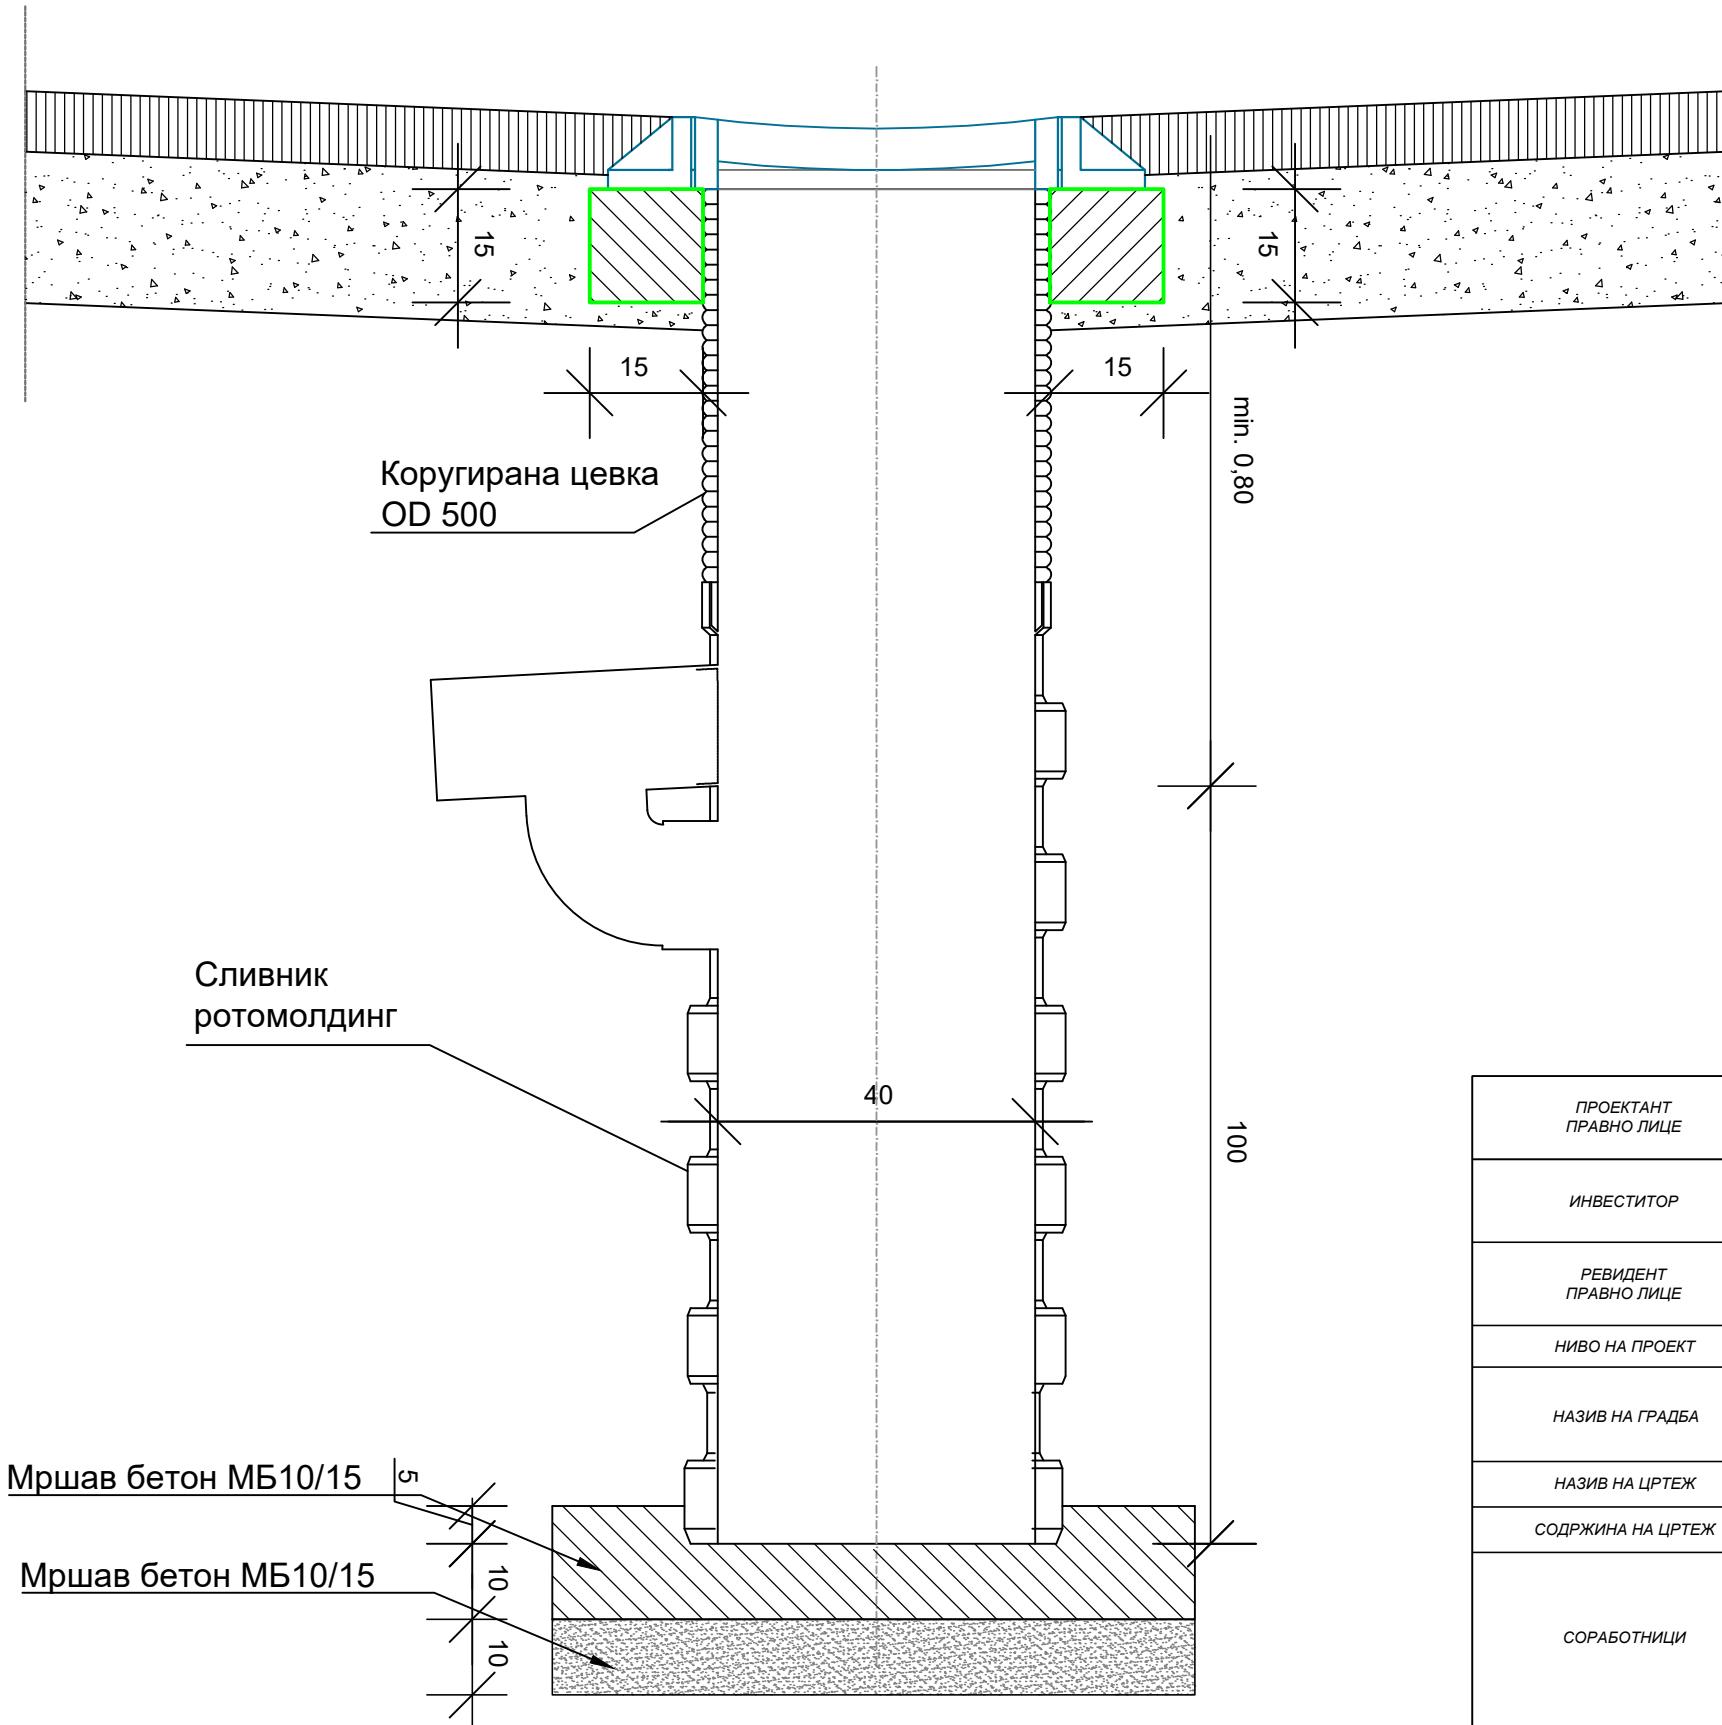


- ОСНОВА
R=1:10

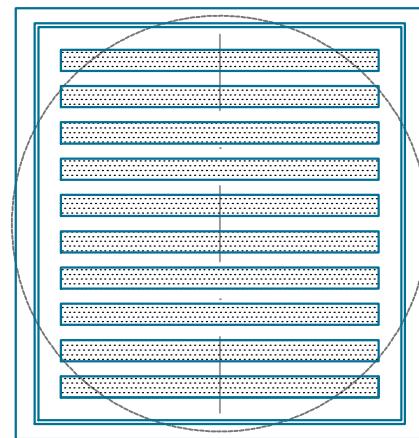



ПРОЕКТАНТ ПРАВНО ЛИЦЕ	ДОМИНГ ЈТД РАДОВИШ 	ОЗНАКА	ЦРТЕЖ БР.	РАЗМЕР	ВЕРЗИЈА			
		ВК	5	1:10	2			
ИНВЕСТИТОР	ОПШТИНА ГАЗИ БАБА 	ВИД НА ПРОЕКТ	ПРОЕКТ ЗА ВОДОВОД И КАНАЛИЗАЦИЈА					
		ТЕХ. БРОЈ	074/2021 - К					
РЕВИДЕНТ ПРАВНО ЛИЦЕ		ДАТА	Јануари 2023					
		ДИМЕНЗИИ	297 x 210 mm					
ОСНОВЕН ПРОЕКТ								
ОСНОВЕН ПРОЕКТ ЗА ИЗГРАДБА НА АТМОСФЕРСКА КАНАЛИЗАЦИЈА ПО УЛИЦИ ОРДАН ПОП ЈОРДАНОВ, ОРДАН ПИПЕРКАТА И ИВАН НАУМОВ АЛАБАКОТ, МАЦАРИ 1, УРБАН БЛОК 1, ОПШТИНА ГАЗИ БАБА								
ДЕТАЛИ								
ДЕТАЛ НА ТИПСКИ СЛИВНИК ЗА АТМОСФЕРСКА КАНАЛИЗАЦИЈА								
м-р Трајко Костадинов д.г.и. Весна Хаџисмилева Кузмановски д.г.и. Александар Поцев д.г.и. Дарко Тодоровски геод. техн.								
ПЕЧАТ И ПОТПИС НА ПРАВНО ЛИЦЕ ПРОЕКТАНТ								
ОДГОВОРЕН ПРОЕКТАНТ печат и потпис			ОВЛАСТЕН РЕВИДЕНТ печат и потпис					
ЉУБЕНКА СТОЈАНОВА ТРЕНДАФИЛОВА д.г.и.								
Управител ЈОВАН КОСТАДИНОВ								

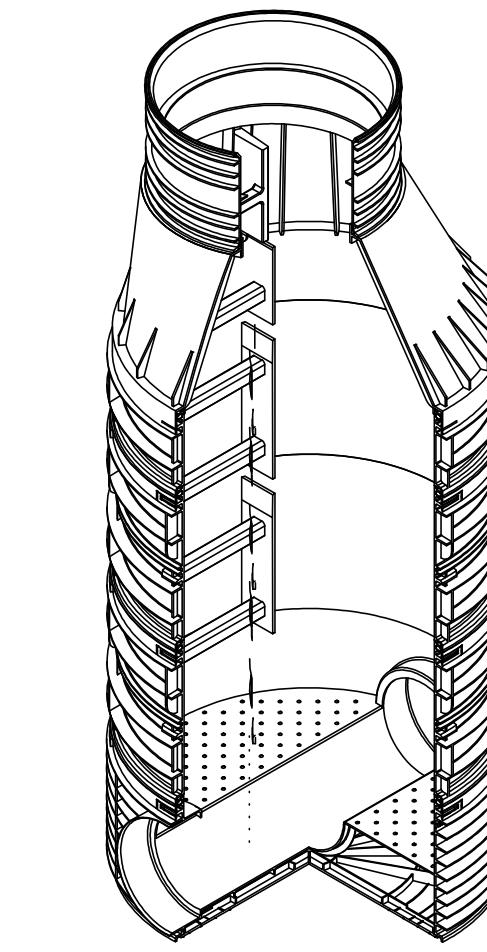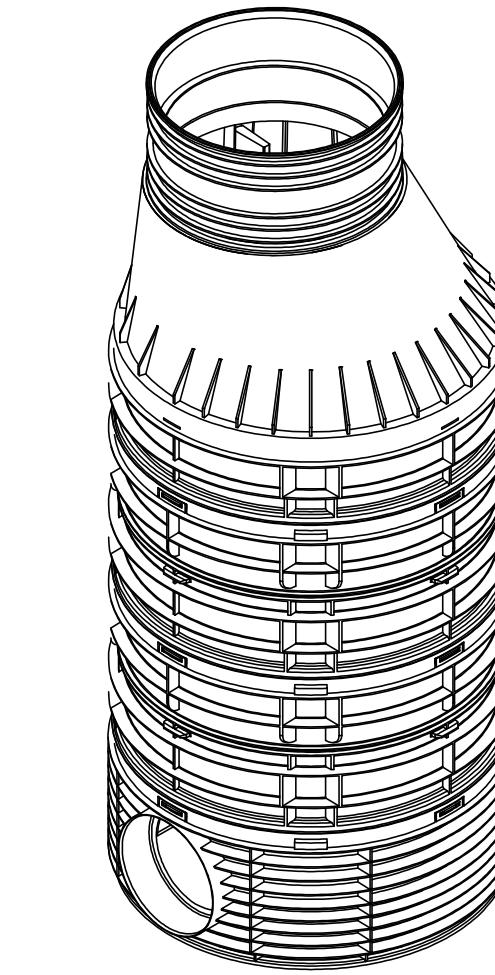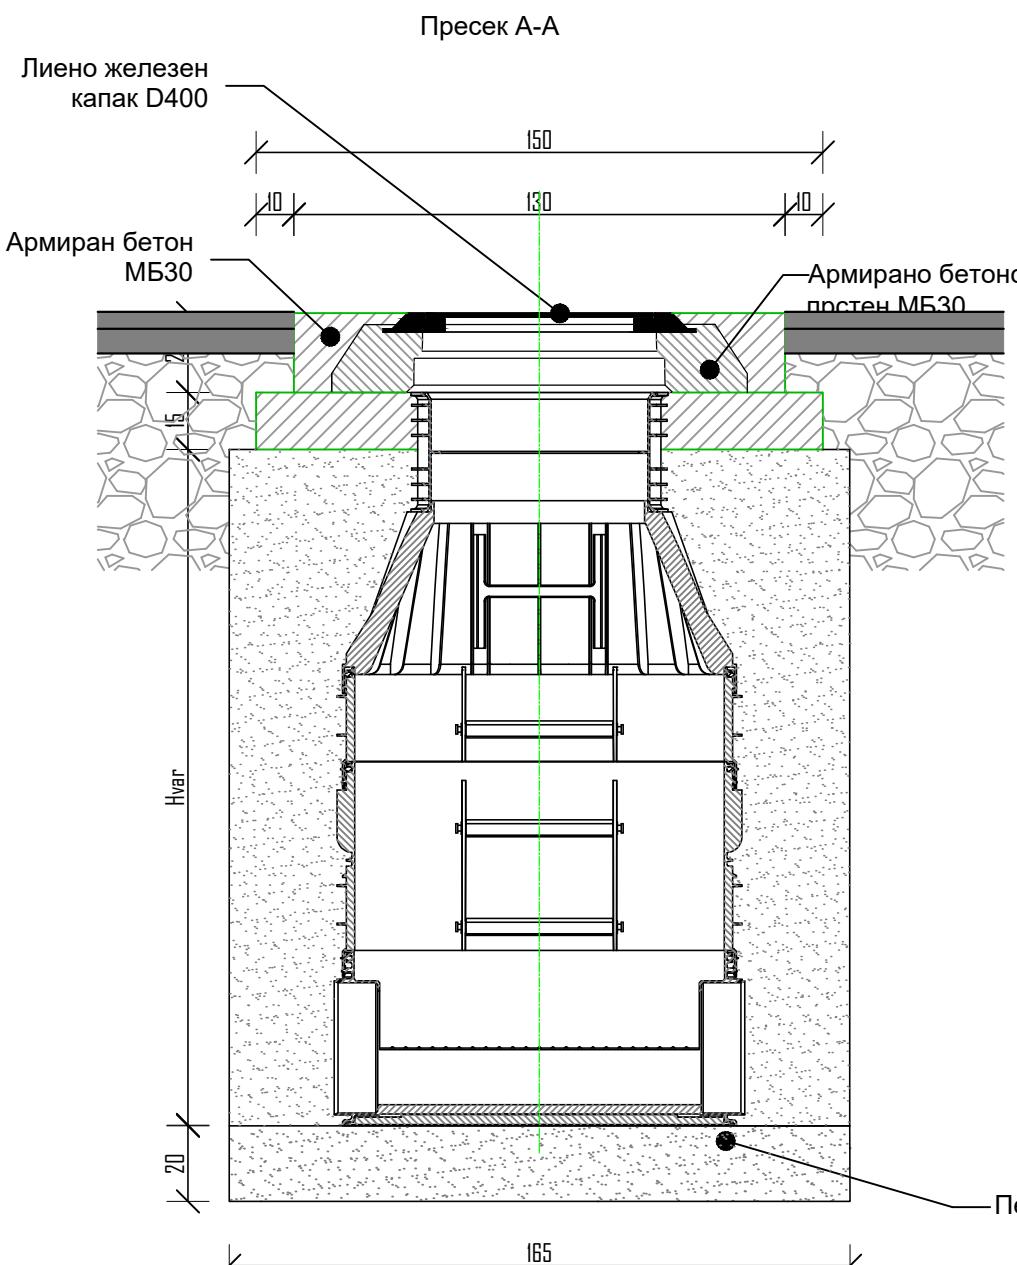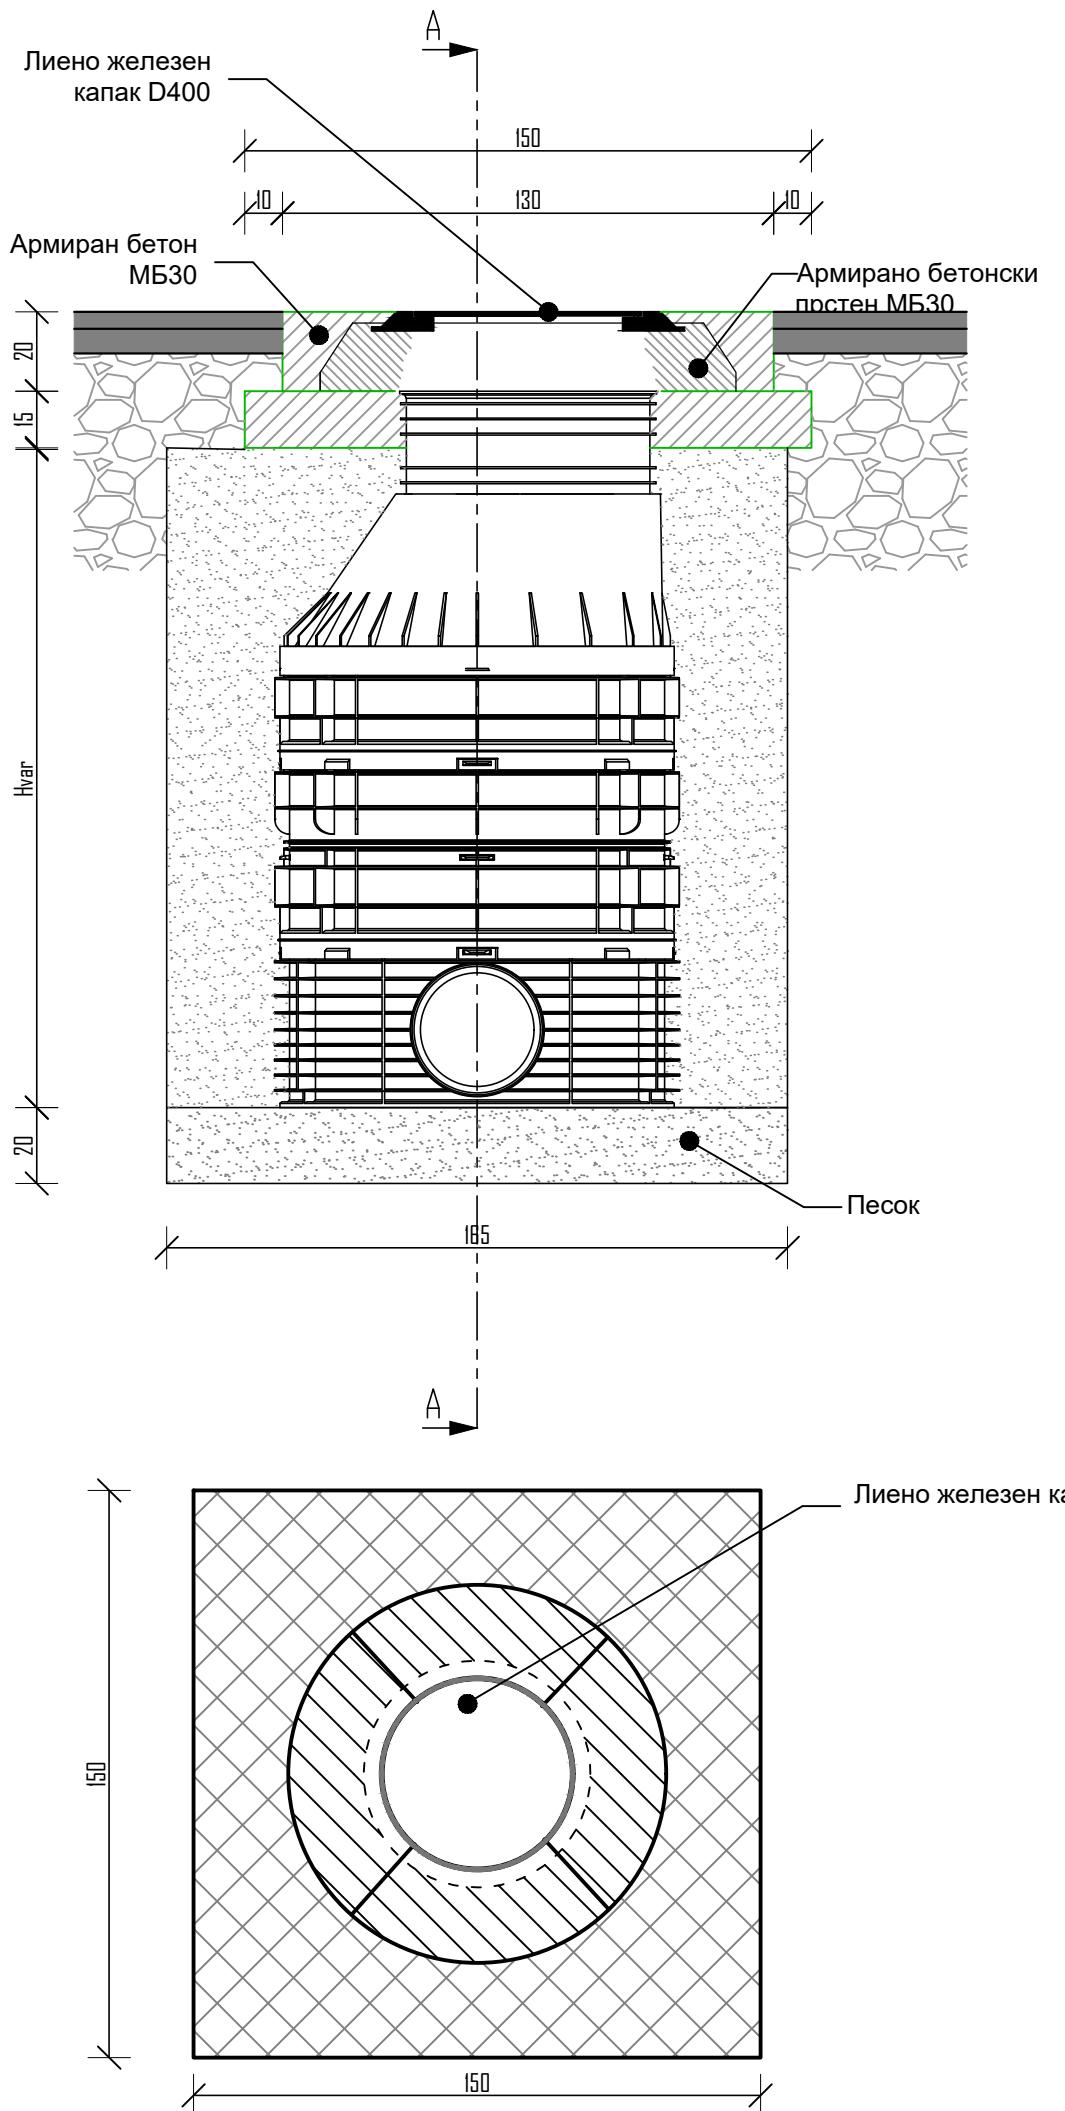

ПРОЕКТАНТ ПРАВНО ЛИЦЕ	ДОМИНГ ЈТД РАДОВИШ	ОЗНАКА	ЦРТЕЖ БР.	РАЗМЕР	ВЕРЗИЈА
ВК	6	1:20	2		ПРОЕКТ ЗА ВОДОВОД И КАНАЛИЗАЦИЈА
ИНВЕСТИТОР	ОПШТИНА ГАЗИ БАБА				ВИД НА ПРОЕКТ ТЕХ. БРОЈ 074/2021 - К
РЕВИДЕНТ ПРАВНО ЛИЦЕ					ДАТА Јануари 2023
НИВО НА ПРОЕКТ					ДИМЕНЗИИ 297 x 580 mm
НАЗИВ НА ГРАДБА	ОСНОВЕН ПРОЕКТ ЗА ИЗГРАДБА НА АТМОСФЕРСКА КАНАЛИЗАЦИЈА ПО УЛИЦИ ОРДАН ПОП ЈОРДАНОВ, ОРДАН ПИПЕРКАТА И ИВАН НАУМОВ АЛАБАКОТ, МАЦАРИ 1, УРБАН БЛОК 1, ОПШТИНА ГАЗИ БАБА				
НАЗИВ НА ЦРТЕЖ	ДЕТАЛИ				
СОДРЖИНА НА ЦРТЕЖ	ДЕТАЛ НА ТИПСКА РЕВИЗИОНА ШАХТА - РШ1-РШ6, РШ8-РШ12, РШ21-РШ39				
СОРАБОТНИЦИ	м-р Трајко Костадинов д.г.и. Весна Хаџисимилева Кузмановски д.г.и. Александар Поцев д.г.и. Дарко Тодоровски геод. техн.	ПЕЧАТ И ПОПИС НА ПРАВНО ЛИЦЕ ПРОЕКТАНТ			
ОДГОВОРЕН ПРОЕКТАНТ ПЕЧАТ И ПОПИС	ЛЈУБЕНКА СТОЈАНОВА ТРЕНДАФИЛОВА д.г.и.	ОВЛАСТЕН РЕВИДЕНТ ПЕЧАТ И ПОПИС			
			Управител ЈОВАН КОСТАДИНОВ		

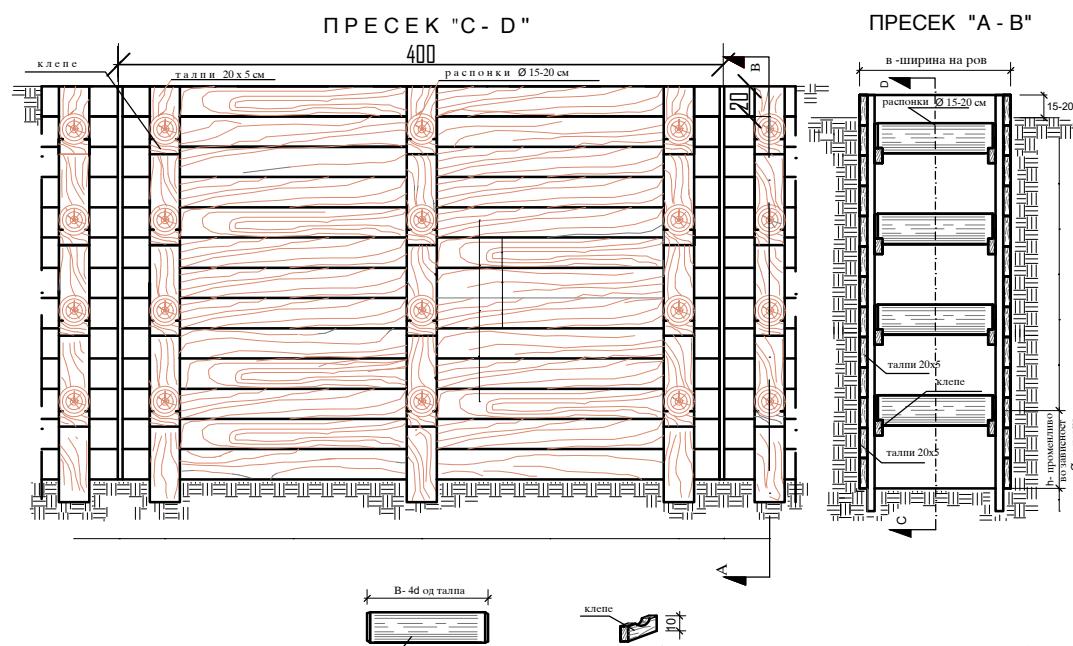

НАЧИН НА РАЗУПИРАЊЕ НА РОВОТ
ПРИ ТЕРЕН СО ЈАК ПРИТИСОК
M=1:25

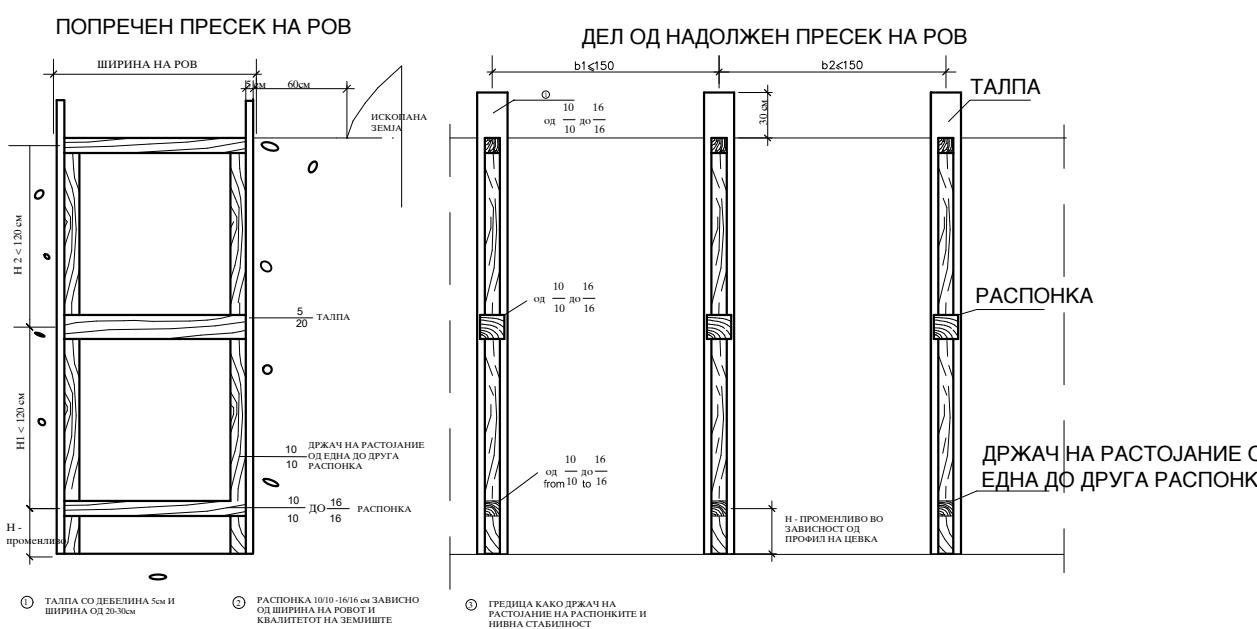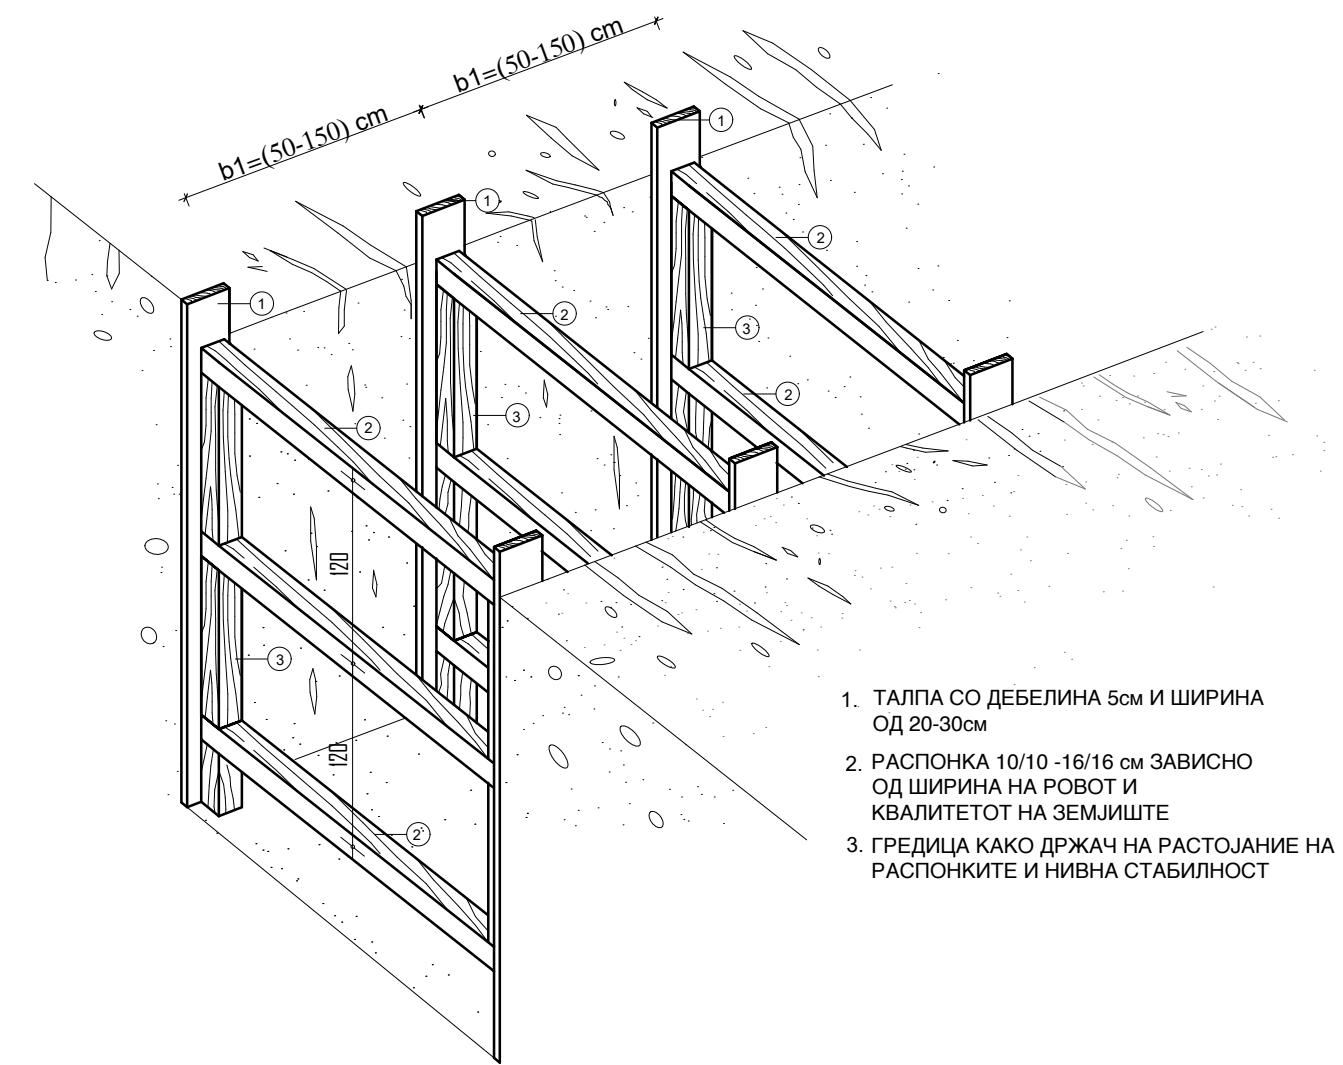

НАЧИН НА РАЗУПИРАЊЕ НА РОВОТ
ПРИ ТЕРЕН СО СЛАБ ПРИТИСОК
M = 1:25

ПРОЕКТАНТ ПРАВНО ЛИЦЕ	ДОМИНГ ЈТД РАДОВИШ 	ОЗНАКА	ЦРТЕЖ БР.	РАЗМЕР	ВЕРЗИЈА
ИНЕСТИТОР		ВК	8	1:50	2
РЕВИДЕНТ ПРАВНО ЛИЦЕ		ПРОЕКТ ЗА ВОДОВОД И КАНАЛИЗАЦИЈА			
НИВО НА ПРОЕКТ		ТЕХ. БРОЈ	074/2021 - К		
НАЗИВ НА ГРАДБА		ДАТА	Јануари 2023		
НАЗИВ НА ЦРТЕЖ		ДИМЕНЗИИ	297 x 420 mm		
СОДРЖИНА НА ЦРТЕЖ	ОСНОВЕН ПРОЕКТ ОСНОВЕН ПРОЕКТ ЗА ИЗГРАДБА НА АТМОСФЕРСКА КАНАЛИЗАЦИЈА ПО УЛИЦИ ОРДАН ПОП ЈОРДАНОВ, ОРДАН ПИПЕРКАТА И ИВАН НАУМОВ АЛАБАКОТ, МАЦАРИ 1, УРБАН БЛОК 1, ОПШТИНА ГАЗИ БАБА				
СОРАБОТНИЦИ	ДЕТАЛИ ДЕТАЛ НА РАЗУПИРАЊЕ НА РОВ м-р Трајко Костадинов д.г.и. Весна Хаџисимилева Кузмановски д.г.и. Александар Потев д.г.и. Дарко Тодоровски геод. техн.				
	ПЕЧАТ И ПОТПИС НА ПРАВНО ЛИЦЕ ПРОЕКТАНТ				
ОДГОВОРЕН ПРОЕКТАНТ печат и потпис	ОВЛАСТЕН РЕВИДЕНТ печат и потпис				
ЉУБЕНКА СТОЈАНОВА ТРЕНДАФИЛОВА д.г.и.					

Управител
ЈОВАН КОСТАДИНОВ