



МГ ПРОЕКТ ДООЕЛ СКОПЈЕ


Друштво за проектирање, инженеринг, трговија и услуги
ул. Никола Парапунов бр. 27-3/20, Скопје; моб: 070/262-154; 070/207-561
email: mgprojekt2018@gmail.com

**ОСНОВЕН ПРОЕКТ ЗА ИЗГРАДБА НА
ПЕШАЧКА УЛИЦА ДЕЛ ОД УЛ. ВАНЧО ПРЌЕ
ДЕЛ ОД КП 7505/1 И ДЕЛ ОД КП 7153/1 КО ШТИП 5
ОПШТИНА ШТИП
ФАЗА АРХИТЕКТУРА**

Тех.бр. ОП – 67/24

2024

ГРАФИЧКИ ПРИЛОЗИ

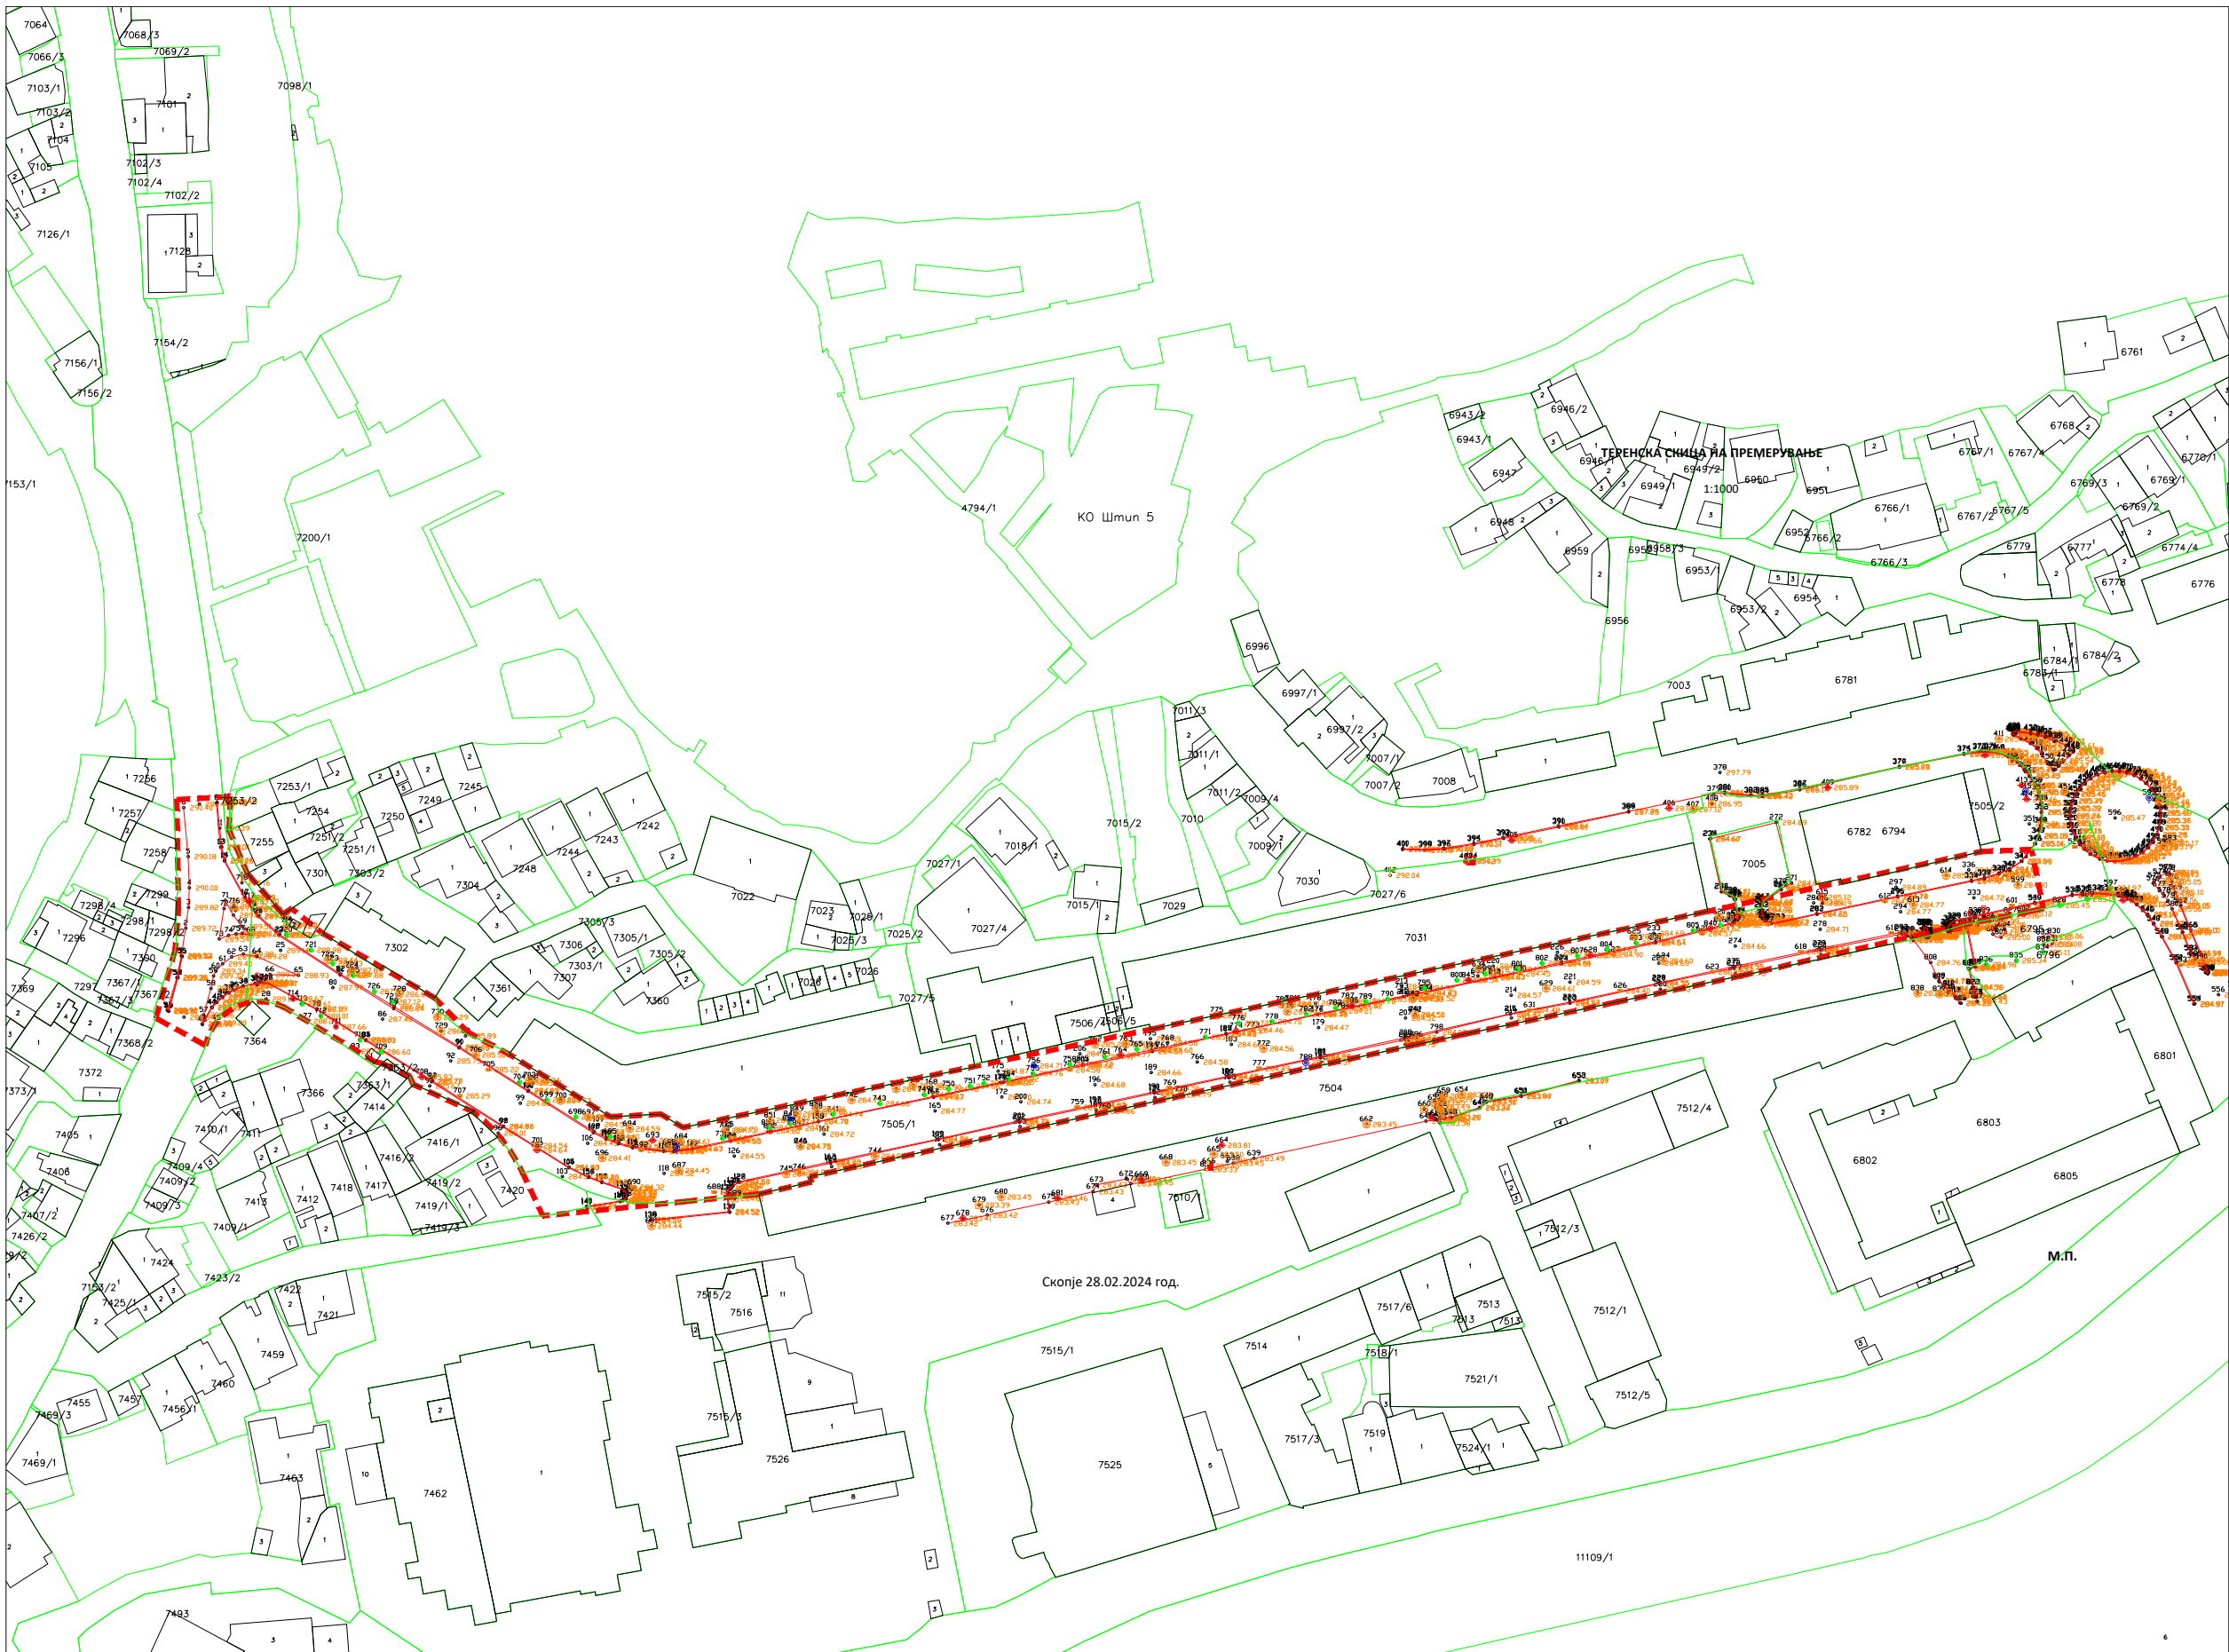


ЛЕГЕНДА	
ГРАФИЧКИ ПРИКАЗ НА ТОПОГРАФСКИ ЗНАК	ОПИС НА ЗНАКОТ
	ГРАНИЦИ НА КАТАСТАРСКИ ПАРЦЕЛИ
	СИТУАЦИЈА НА ЛАЖНО МЕСТО
	ИЗОЛИНИИ
	ОПШТИ
	ТРЕЌИНИ
	ПРИРОДНО ЕЗЕРО
	ДЕЛ
	СТОВНИК
	БЕТОНСКИ ЗИД
	ЖИЧНА ОГРАДА
	РЕВИЗИОНО ОКНО НЕПРСТАСТО
	ПАДНА ЛАНКА (ТРАП)
	УЛИЦИ
	НЕКАТЕГОРИЗИРАНИ ПАТИШТА
	ДАЛЕКОВОД НАПОД ДРВЕН
	ДАЛЕКОВОД НАПОД БЕТОНСКИ
	ТЕЛЕФОНСКИ СТОП ДРВЕН
	ТЕЛЕФОНСКИ СТОП БЕТОНСКИ
	ДИРЕКТНО ОСВЕТЛУВАЊЕ
	ПАРКИРАЛИШТЕ
	ПОСТОЈЕН ЗИД
	ЖЕЛЕЗНА ОГРАДА НА ЗИД
	ЖИЧНА ОГРАДА НА ЗИД
	ЕЛЕКТРОЕНЕРГЕТСКИ ОБЈЕКТИ
	ИНДИВИДУАЛНА ЗГРАДА
	ДВООБНА ЗГРАДА
	ПОВИСОКА ЗГРАДА
	РЕВИЗИОНО ОКНО КРУЖНО

- ПРИКЛУЧОК ЗА ВОДА
- ПОДЗЕМЕН ХИРАНТ СО ЗАТВОРАН
- ДРВОРЕД
- СОВЕТАМЕН ЗНАК
- СЕМАФОР
- РЕКЛАМНО ПАНО
- ТРАНСФОРМАТОР
- ЖИЧНА ОГРАДА
- ЖИЧНА ОГРАДА НА ЗИД
- ЖЕЛЕЗНА ОГРАДА НА ЗИД
- ОГРАДА СИДАН КАМЕН
- СИДАН КАМЕН ЖИЦА
- КАНАЛ
- ПРОПУСТ ПРАВОАГОЛЕН
- ПРОПУСТ ЦРКА
- ЧЕШМА





МГ ПРОЕКТ ДООЕЛ СКОПЈЕ

ИНВЕСТИТОР	ОПШТИНА ШТИП		ПРОЕКТАНТИ	
	ОП ЗА ИЗГРАДБА НА ПЕШАЧКА УЛИЦА ДЕЛ ОД УЛ.ВАНЧО ПРКЕ ДЕЛ ОД КП7505/1 И ДЕЛ ОД КП7153/1 КО ШТИП 5		ОДГОВОРЕН ПРОЕКТАНТ	А
ОБЈЕКТ	АЖУРИРАНА ГЕОДЕТСКА СИТУАЦИЈА		МИА: КРИСТИНА ПАВЛЕСКА	
ЦРТЕЖ	УЛИЦИ		ДГИ: САШО ТЕРЗИОСКИ	
ФАЗА	УЛИЦИ		ТЕХ.БР.	ОП -67/24
ДАТА 2024	М 1:1500	БР.НА ЦРТЕЖ	1	

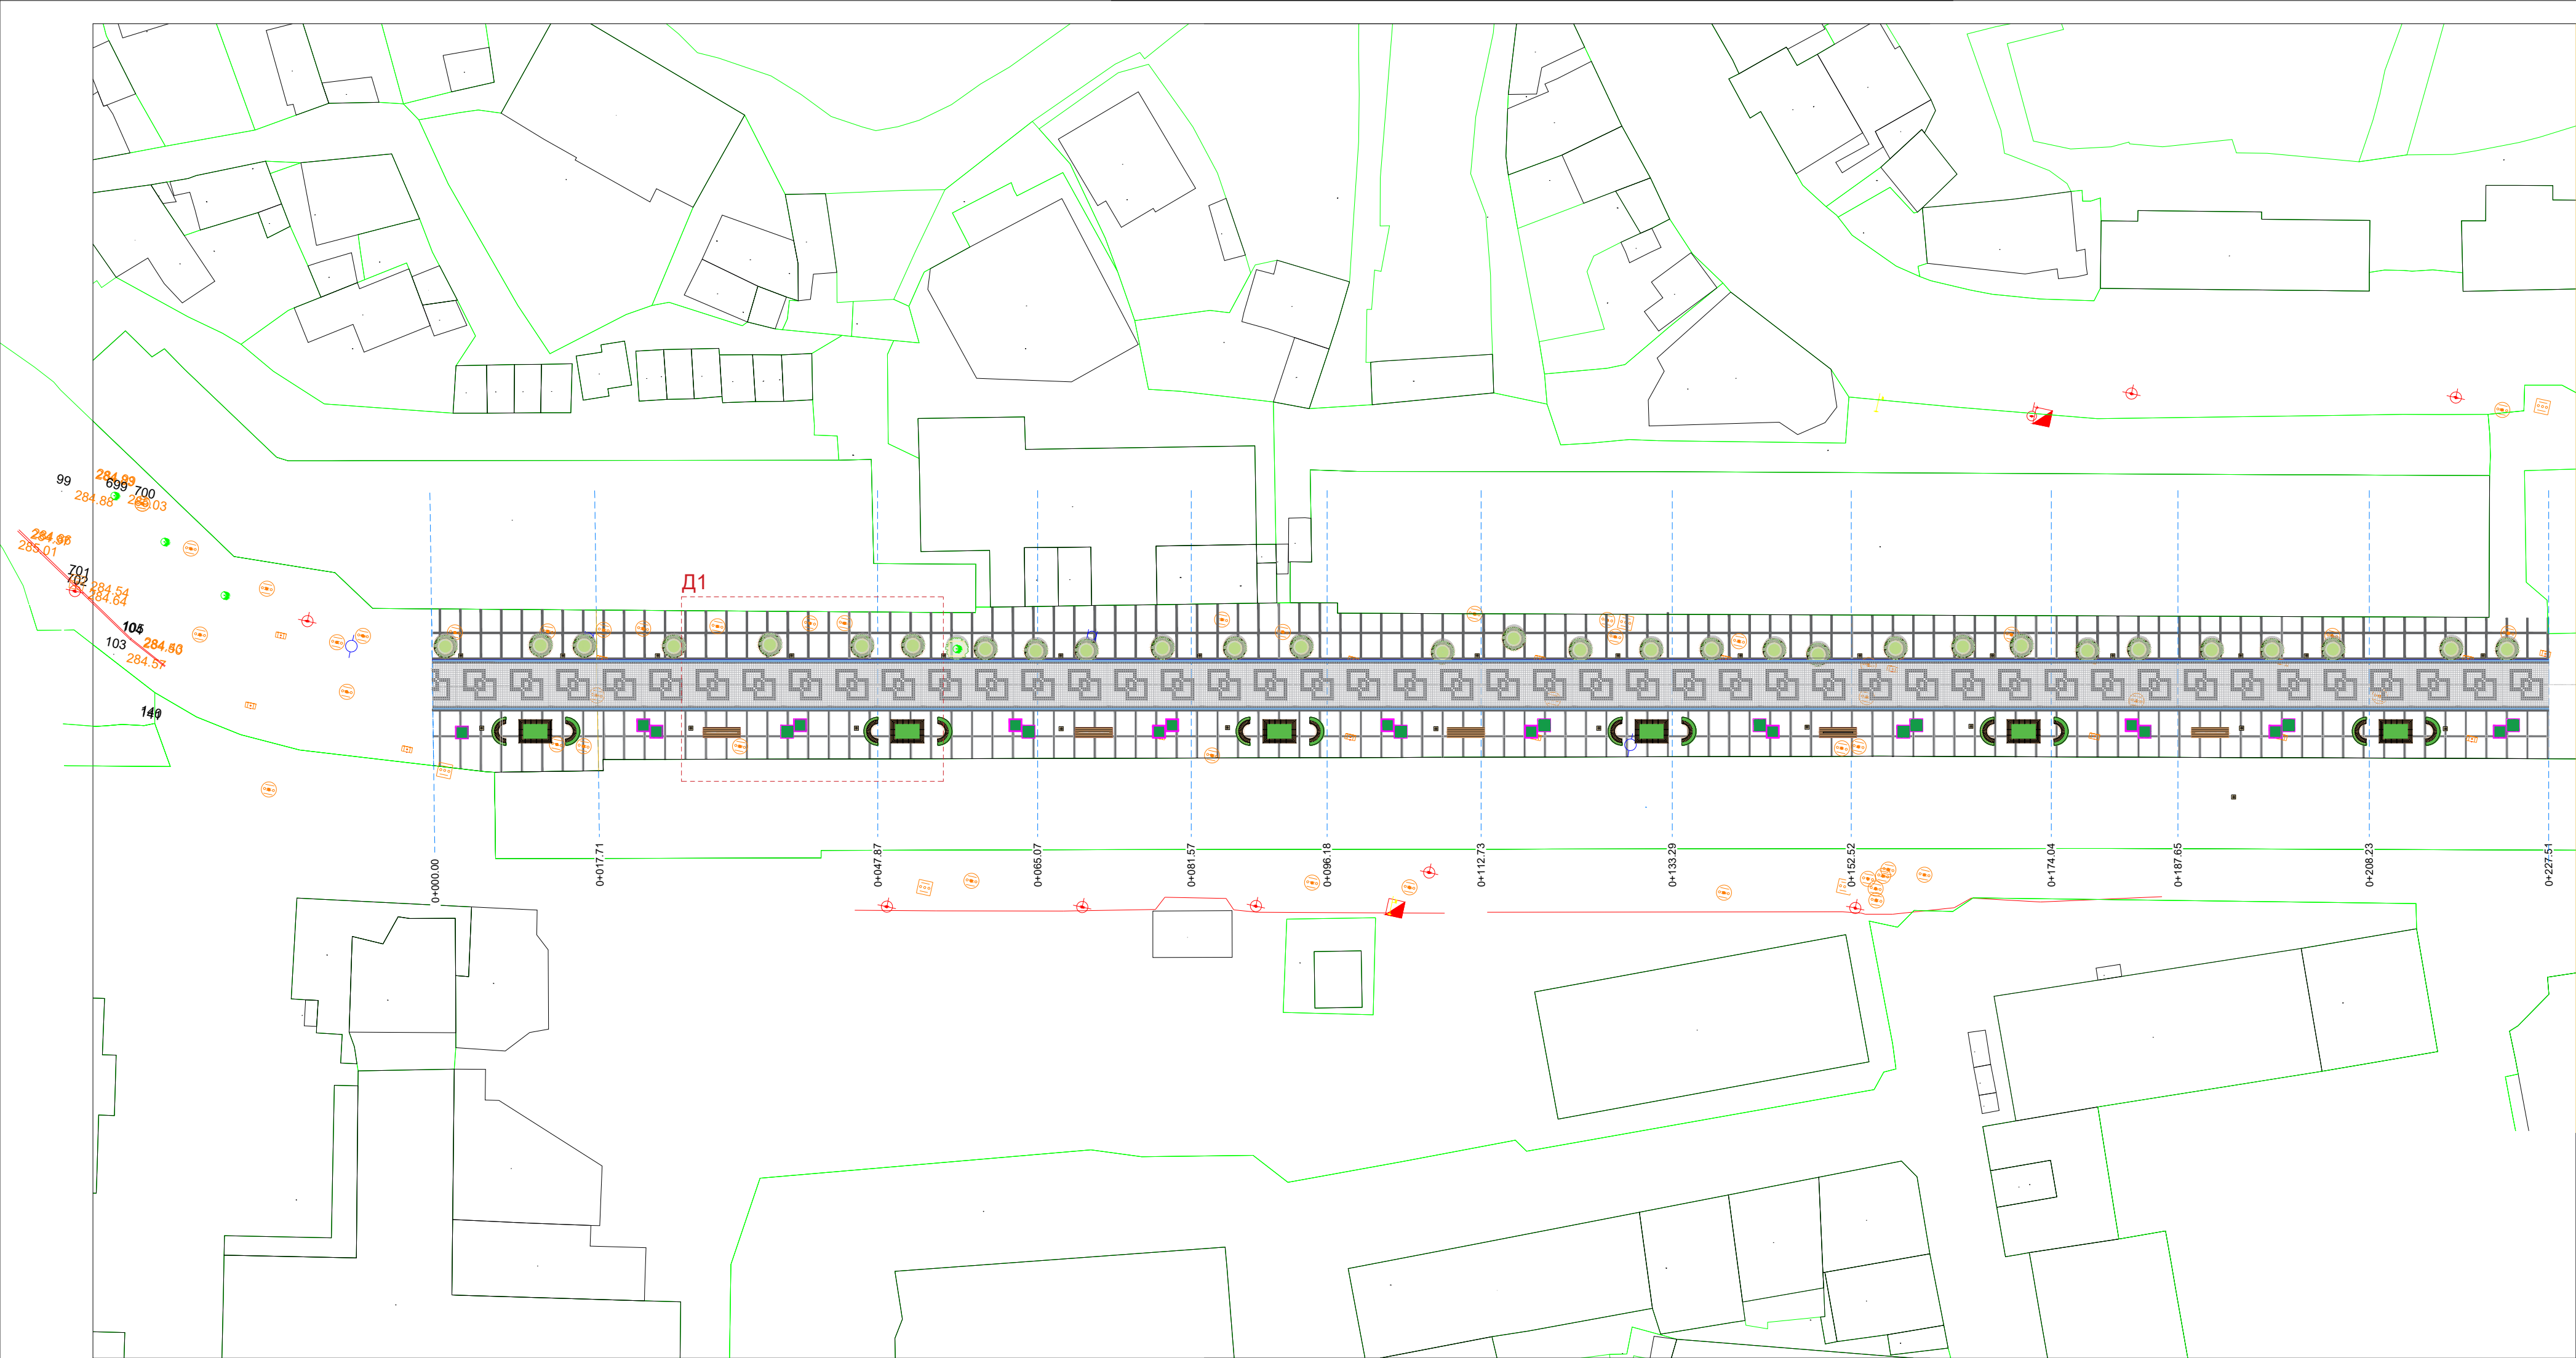

ЛЕГЕНДА:

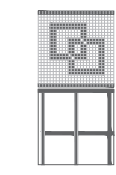 -  Поплочена површина Плочки 20/20см, дебелина д=8см, редени во 2 бои сива и антрацит сива боја, по дадена шема.
-  Решетка за атмосферски води, светол отвор 15см и висина 15см, со носивост до 250KN.
-  Бетонски жардињери (ДЕТАЛ 1)
-  Бетонски жардињери (ДЕТАЛ 2)
-  Парковски клупи (ДЕТАЛ 3)
-  Жардињера (ДЕТАЛ 4)
-  Парковски корпи за отпадоци (ДЕТАЛ 5)



МГ ПРОЕКТ ДООЕЛ СКОПЈЕ


ИНВЕСТИТОР	ОПШТИНА ШТИП		ОСНОВЕН ПРОЕКТ	ПРОЕКТАНТИ	А
	ОП ЗА ИЗГРАБА НА ПЕШАЧКА УЛИЦА ДЕЛ ОД УЛ.ВАНО ПРКЕ ДЕЛ ОД КП7595/1 И ДЕЛ ОД КП7153/1 КО ШТИП.5			ОДГОВОРЕН ПРОЕКТАНТ ММВ: КРИСТИНА ПАВЛЕСКА	
ОБЈЕКТ	НОВОПРЕДВИДЕНА СИТУАЦИЈА		СОРАБОТНИЦИ	ДИ: САШО ТЕРЗИОСКИ	
ЦРТЕЖ	ФАЗА	УЛИЦИ		ТЕХ.БР.	
ДАТА 2024	М 1:500	БР.НА ЦРТЕЖ	2	ОП -67/24	



ДІ

ДЕТАЛ НА ОСНОВА НА РЕДЕЊЕ НА БЕКАТОН

ДІ.1

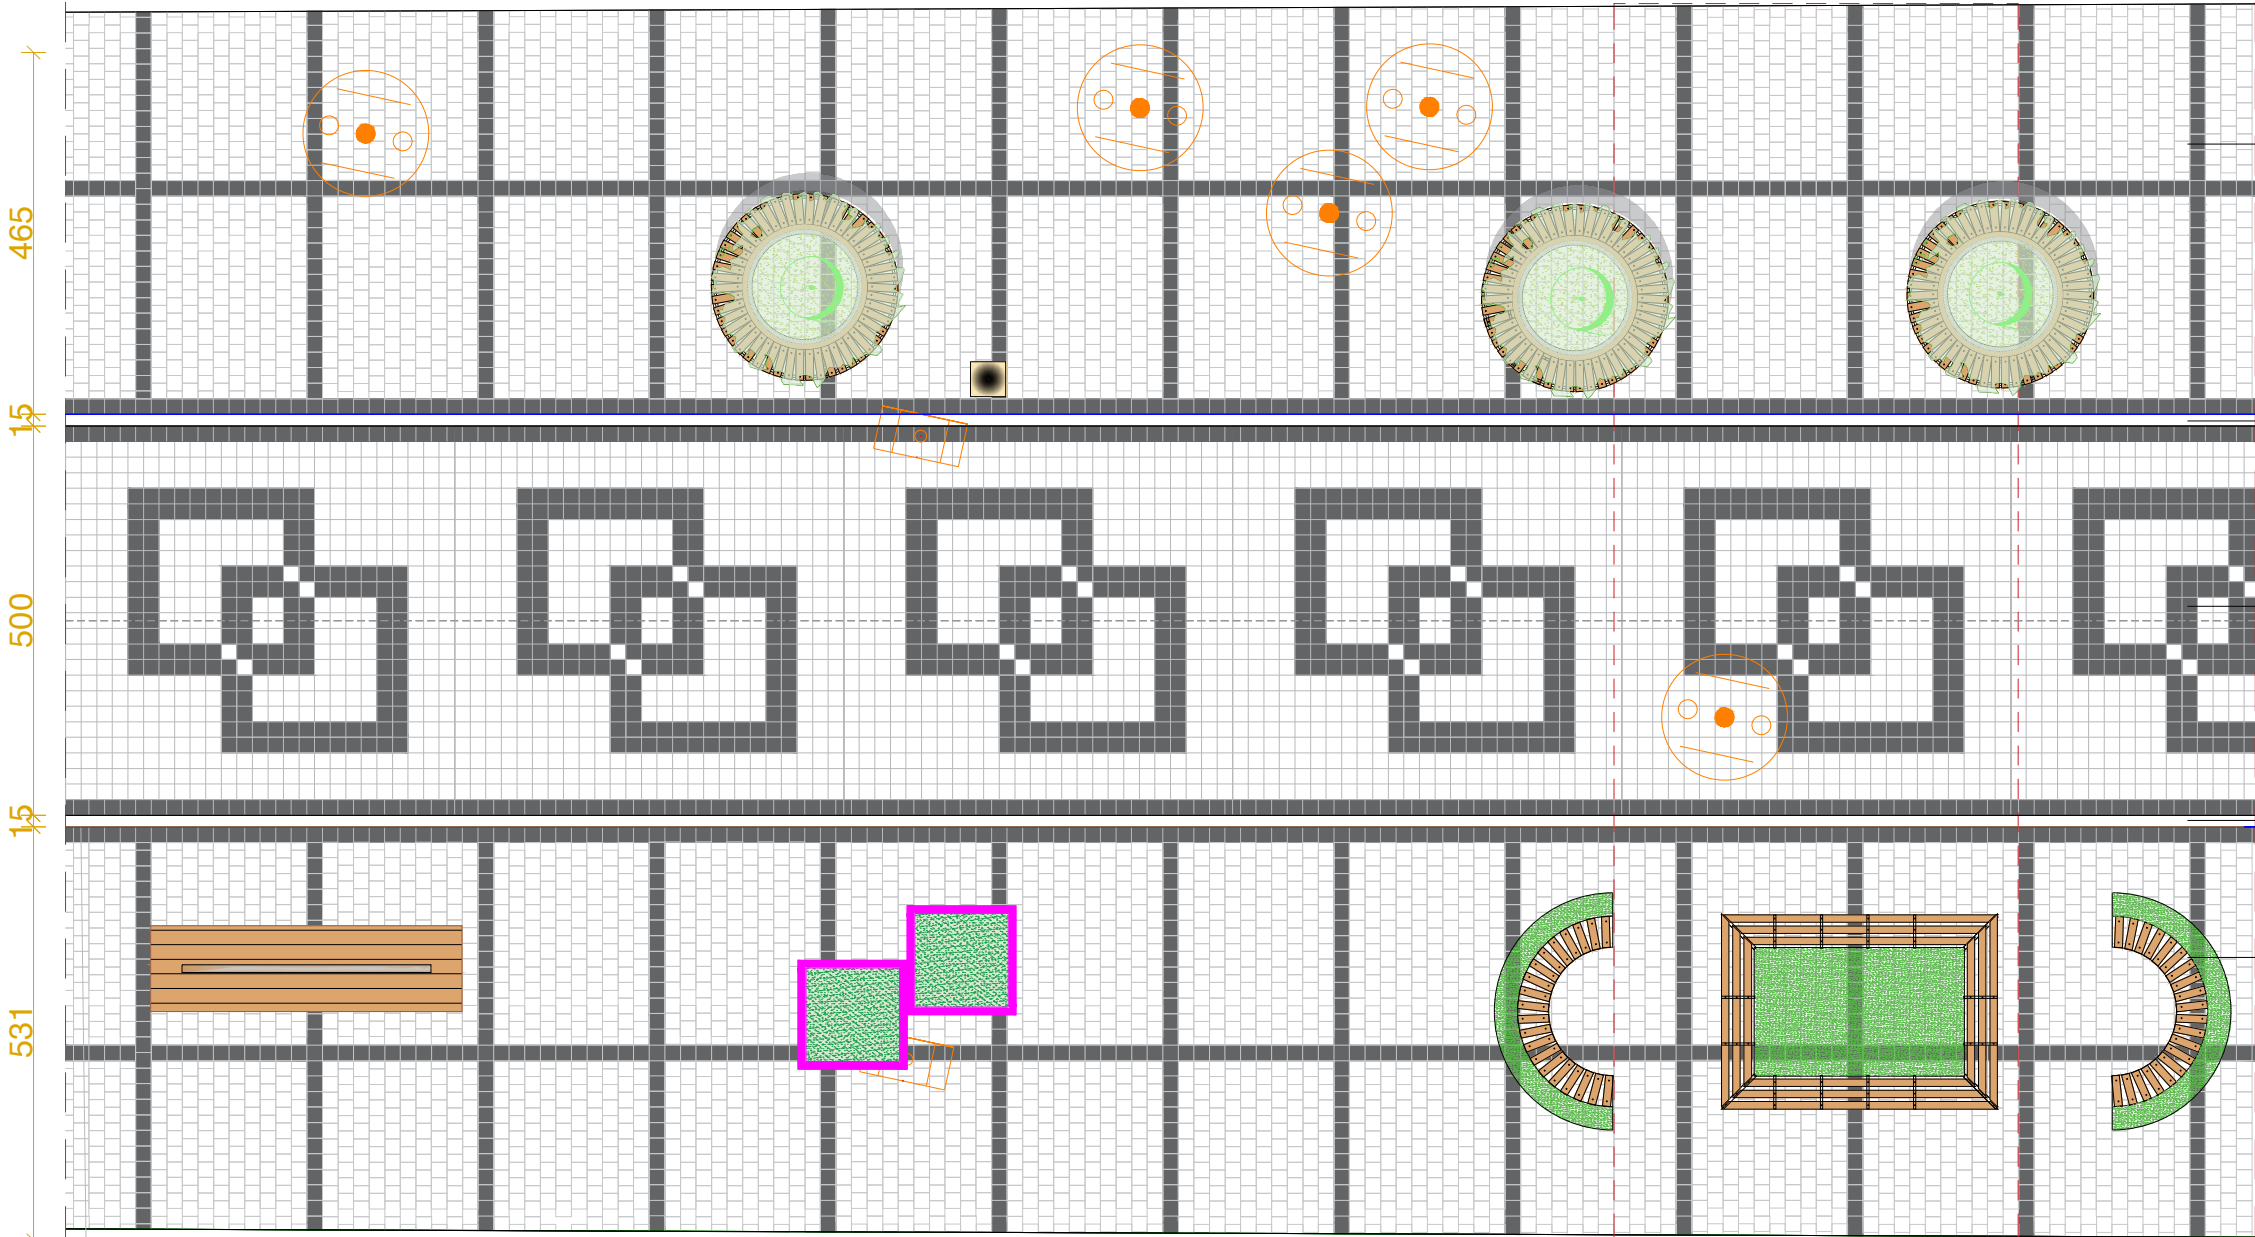

Плочки 20/20см, дебелина д=8см, редени во 2 бои сива и антрацит сива боја, по дадена шема.

Сливна решетка

Плочки 20/20см, дебелина д=8см, редени во 2 бои сива и антрацит сива боја, по дадена шема.

Сливна решетка

Плочки 20/20см, дебелина д=8см, редени во 2 бои сива и антрацит сива боја, по дадена шема.



1:100



МГ ПРОЕКТ ДООЕЛ СКОПЈЕ

ИНВЕСТИТОР	ОПШТИНА ШТИП		ПРОЕКТАНТИ	
	ОП ЗА ИЗГРАДБА НА ПЕШАЧКА УЛИЦА ДЕЛ ОД УЛ.ВАНЧО ПРКЕ ДЕЛ ОД КП7505/1 И ДЕЛ ОД КП7153/1 КО ШТИП 5		ОДГОВОРЕН ПРОЕКТАНТ	А
ОБЈЕКТ	ДЕТАЛ ОД СИТУАЦИОНО РЕШЕНИЕ		МИА: КРИСТИНА ПАВЛЕСКА	
ЦРТЕЖ	УЛИЦИ		ДГИ: САШО ТЕРЗИОСКИ	
ФАЗА	УЛИЦИ		ТЕХ.БР.	ОП -67/24
ДАТА 2024	М 1:100	БР.НА ЦРТЕЖ	3.1	

Д1.1

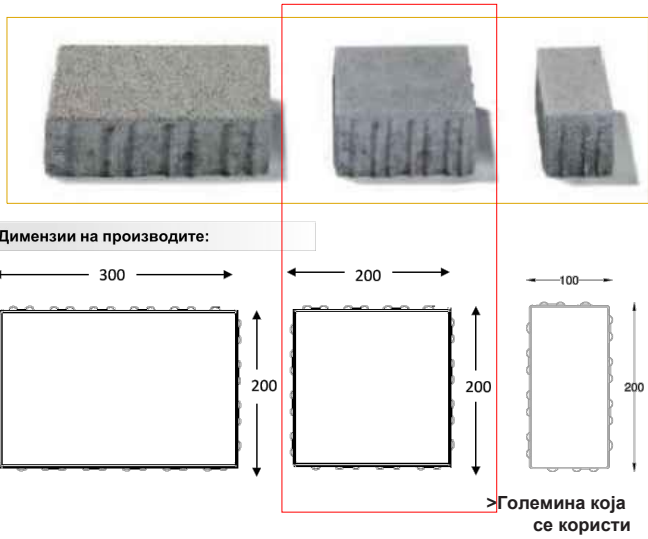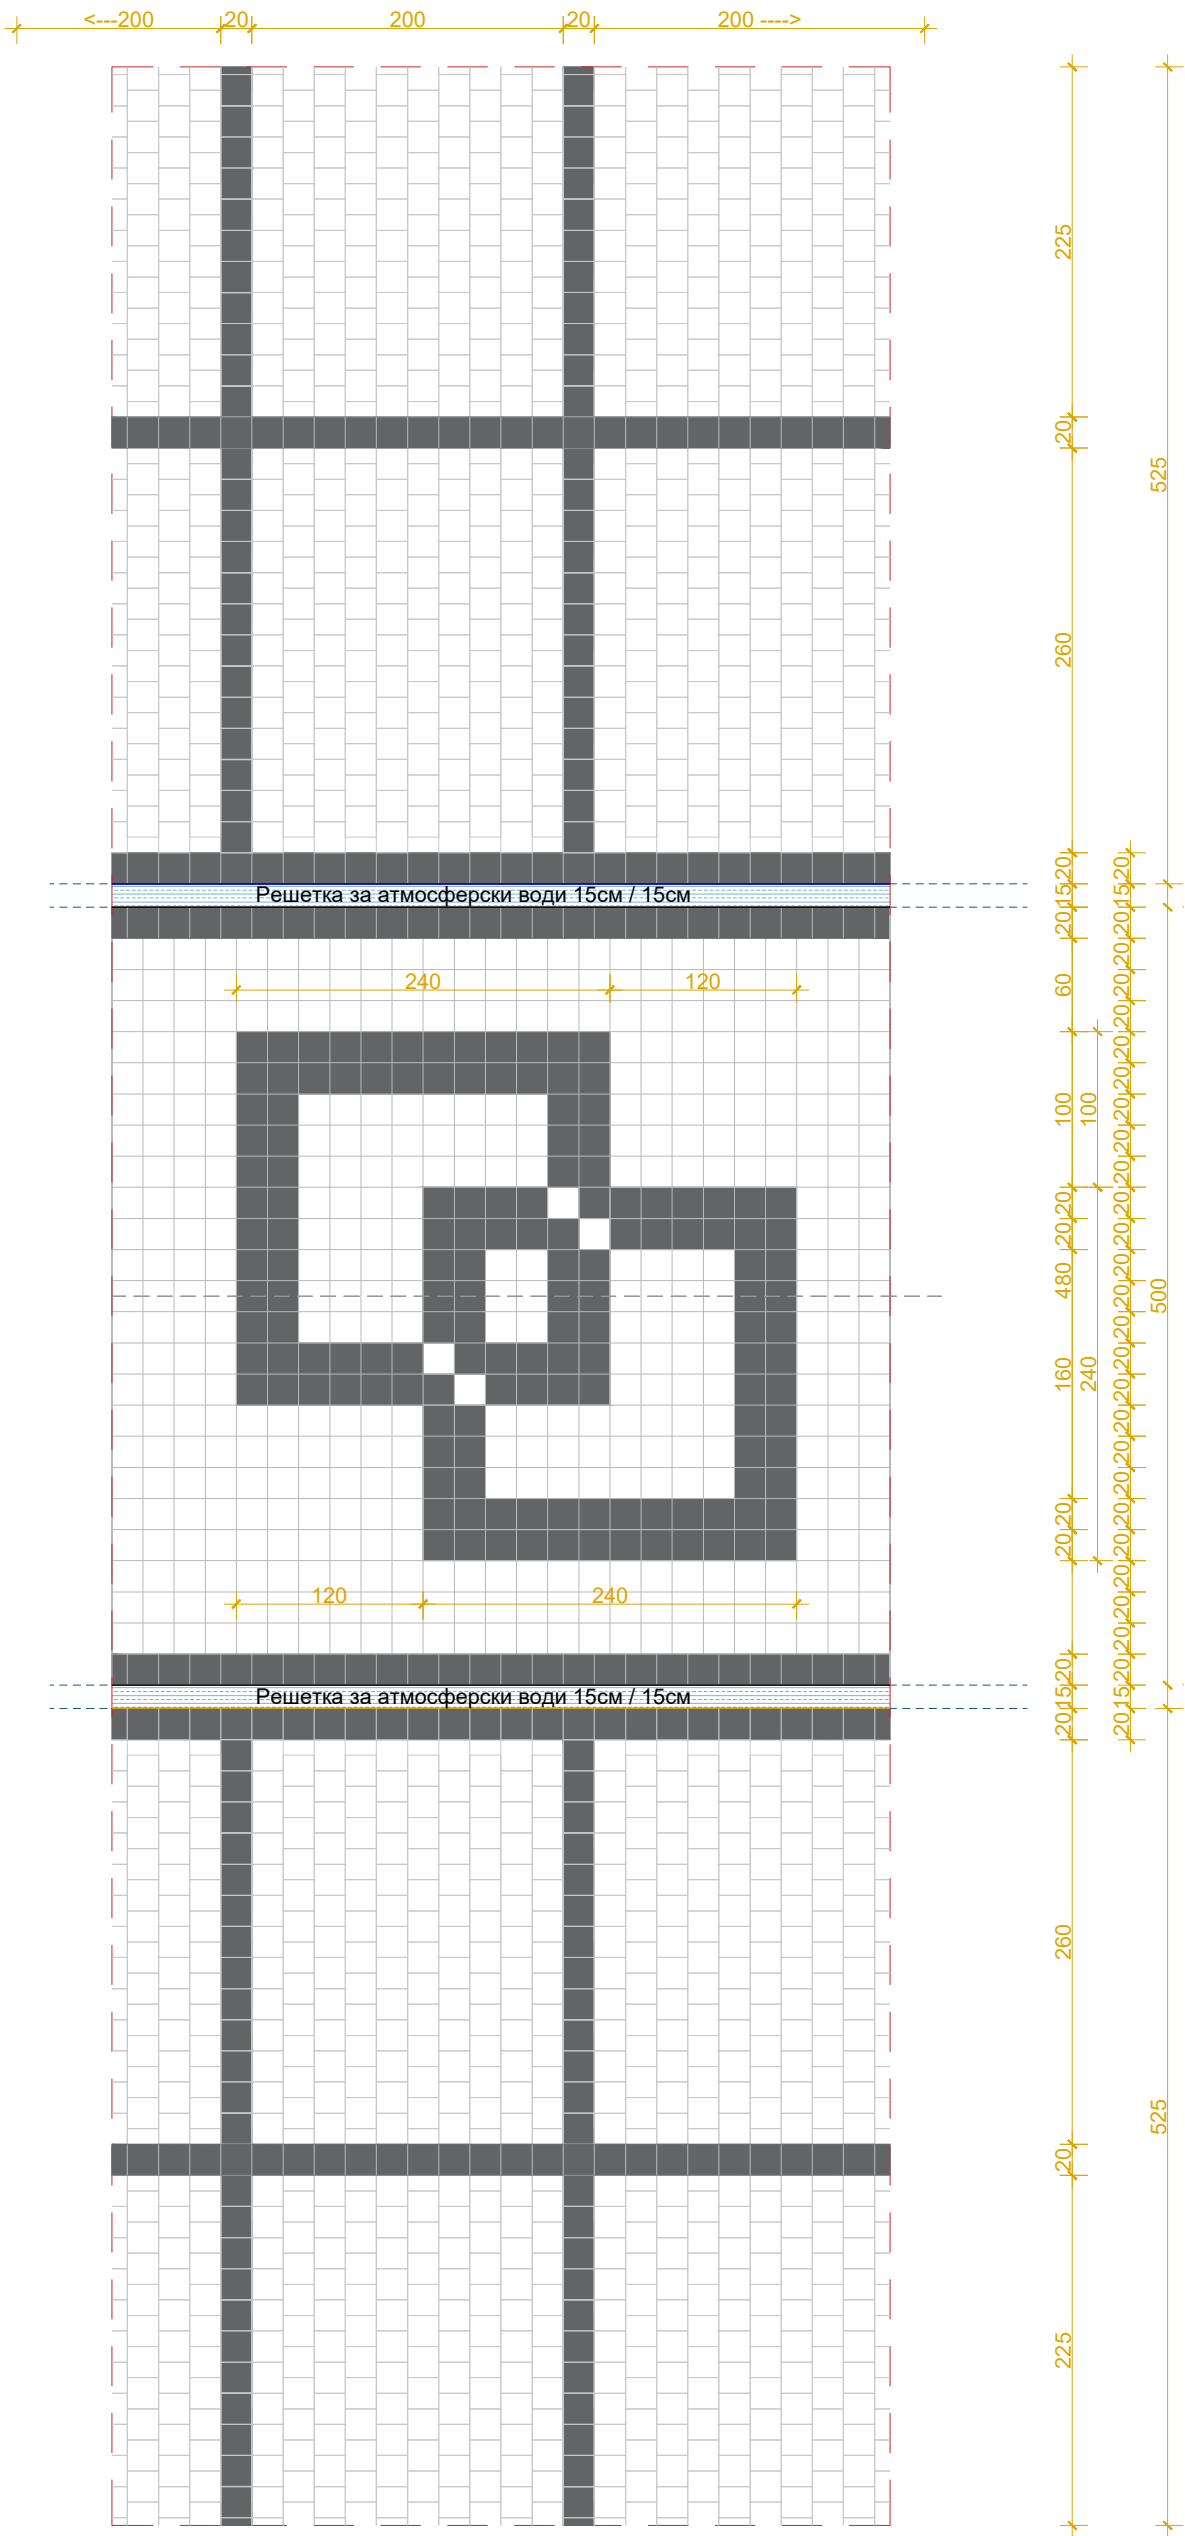

Барања и карактеристики на производите според стандардот EN 1339				
Барања за бетонски плочки за полочување				
Намена:	За изградба на тротоари, алеи, итн.		Облик и димензии на производите	Погледнете го цртежот погоре
Димензии: должина/ширина/висина во mm	Погледнете ја табелата подолу		Јачина на кршење (N / mm)	Задоволува
Толеранции во димензии: должина/ ширина/висина mm	+ 2 - 2	+ 2 - 2	+3 - 3	Отпорност на замрзнување-одмрзнување со соли против замрзнување
Отпорност на абене (mm3)	Класа 4, Ознака I		Абсорпција на вода (g/m2e)	Класа 2, Ознака B


Димензии на растер во cm	Работни димензии во mm	Висина во mm	Тип на раб	Закосување на горниот дел на работ	Препорачана fuga во mm	Приближен трошок за m² со fuga 5 mm
30 x 20	295 x 195					16,67 бр./m²
20 x 20	195 x 195	80	прав	со микрокосина	min.5 mm	25 бр./m²
20 x 10	195 x 95					50 бр./m²

- Особини на производот:
- Површина со изглед на бетон
 - Без разместување и деформации дури и при најтешки оптоварувања
 - Отпорен на УВ-зраци, замрзнување и сол
 - Гарантирана широчина на фугите во согласност со постојните стандарди
 - Специјално развиен за зони со интензивно оптоварување од тешки товарни возила

Карактеристики на производот:



Бои:

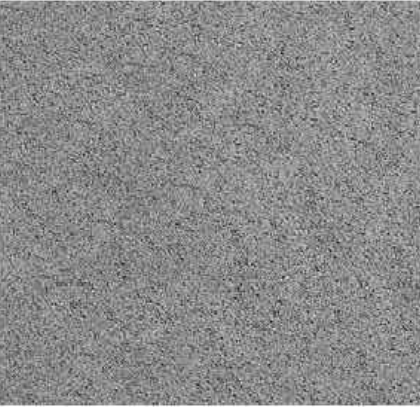

сива




антрацит




МГ ПРОЕКТ ДООЕЛ СКОПЈЕ

ИНВЕСТИТОР	ОПШТИНА ШТИП	ПРОЕКТАНТИ	
ОБЈЕКТ	ОП ЗА ИЗГРАДБА НА ПЕШАЧКА УЛИЦА ДЕЛ ОД УЛ.ВАНЧО ПРКЕ ДЕЛ ОД КП7505/1 И ДЕЛ ОД КП7153/1 КО ШТИП 5	ОДГОВОРЕН ПРОЕКТАНТ МИА: КРИСТИНА ПАВЛЕСКА	А
ЦРТЕЖ	ДЕТАЛ ОД РЕДЕЊЕ НА ПЛОЧКИ	СОРАБОТНИЦИ	ДГИ: САШО ТЕРЗИОСКИ
ФАЗА	УЛИЦИ	ТЕХ.БР.	ОП -67/24
ДАТА 2024	М 1:50	БР.НА ЦРТЕЖ	3.2


Надолжен профил

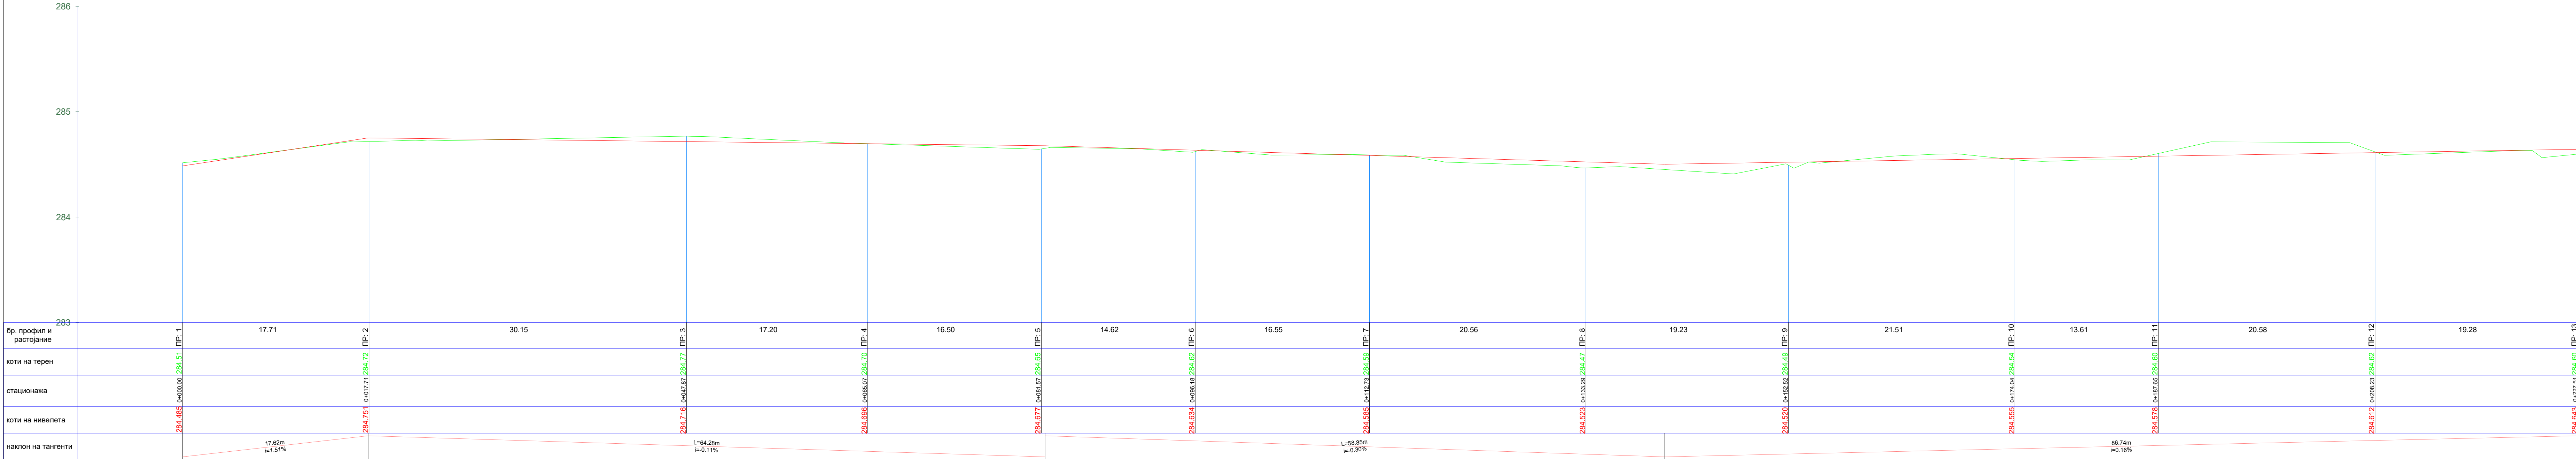


1
0+000.00

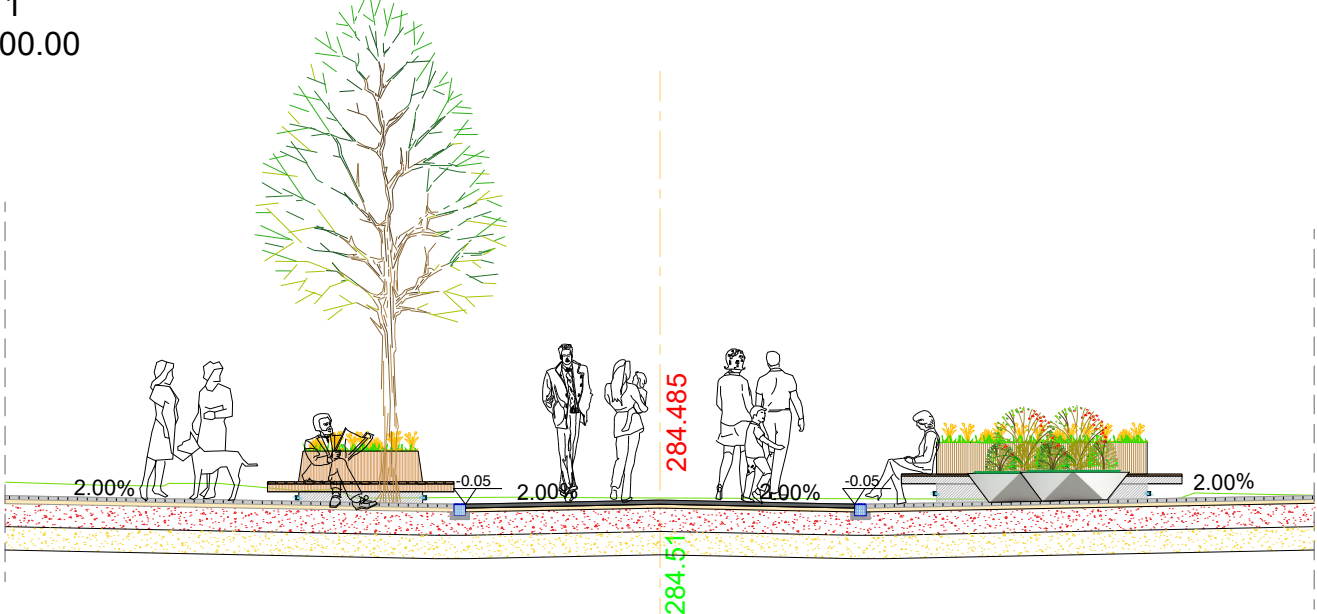


2
0+017.71

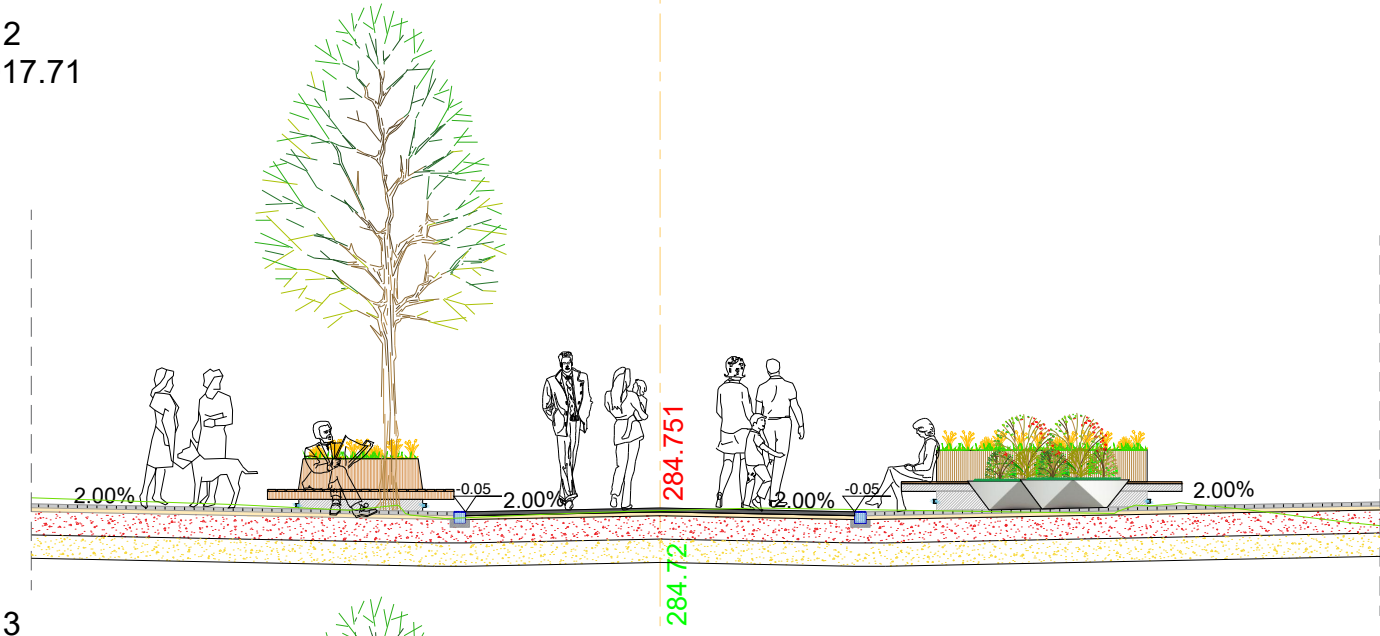


3
0+047.87

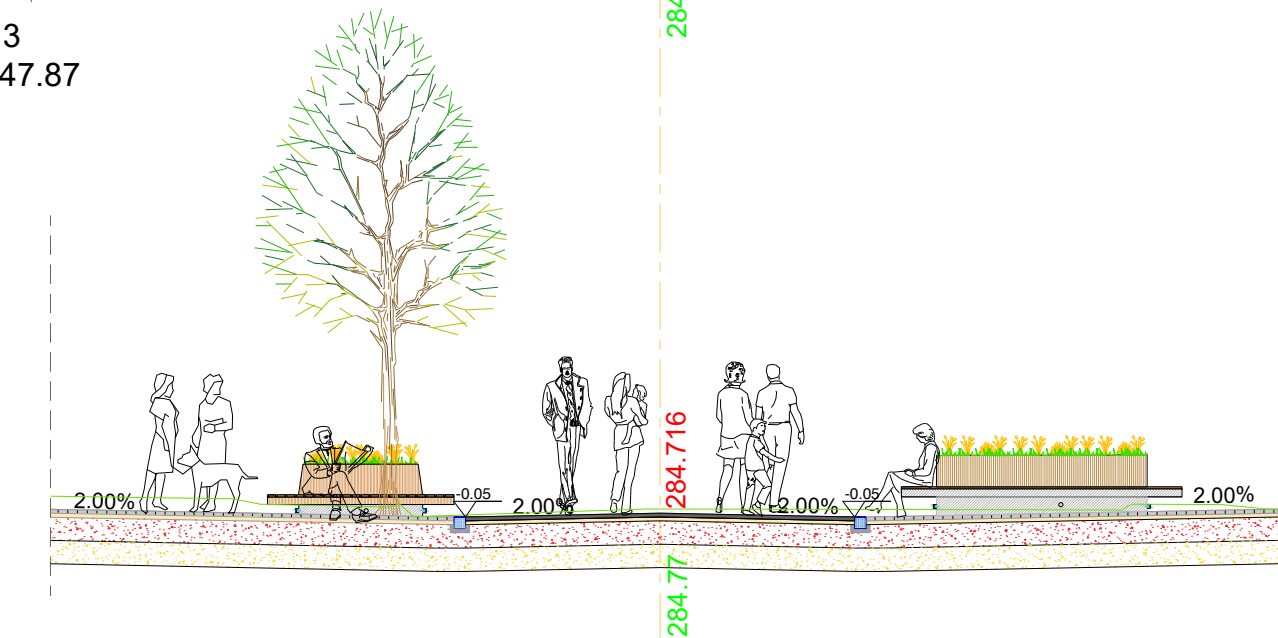


4
0+065.07

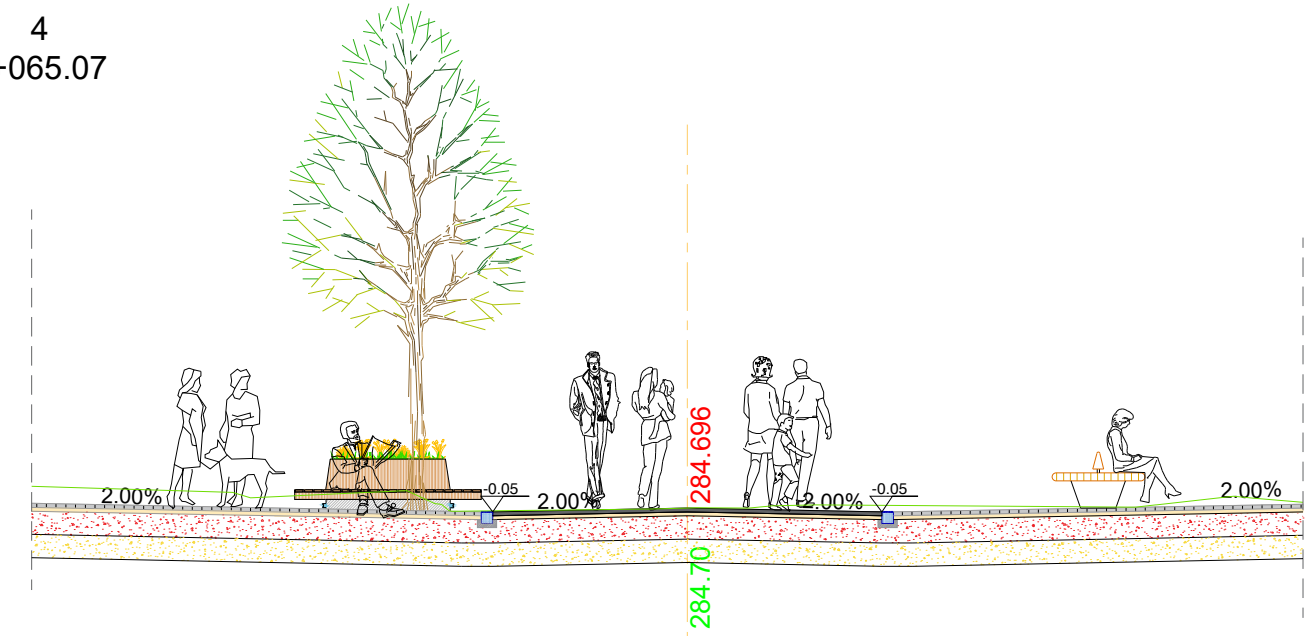

5
0+081.57

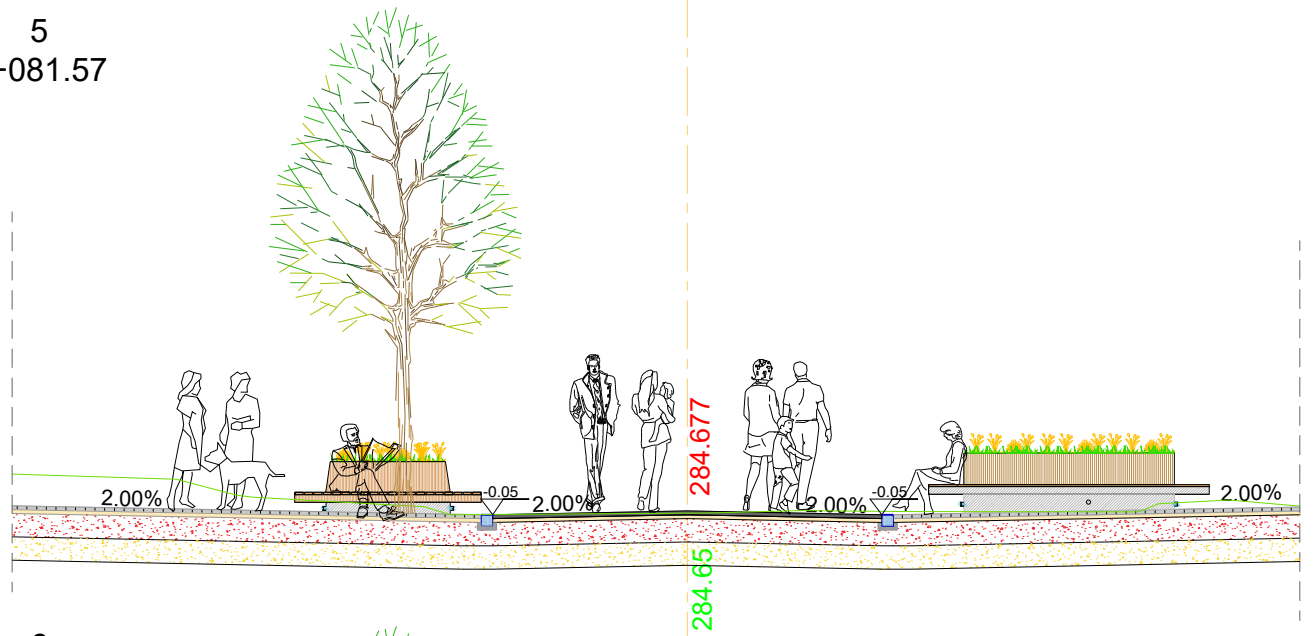



6
0+096.18

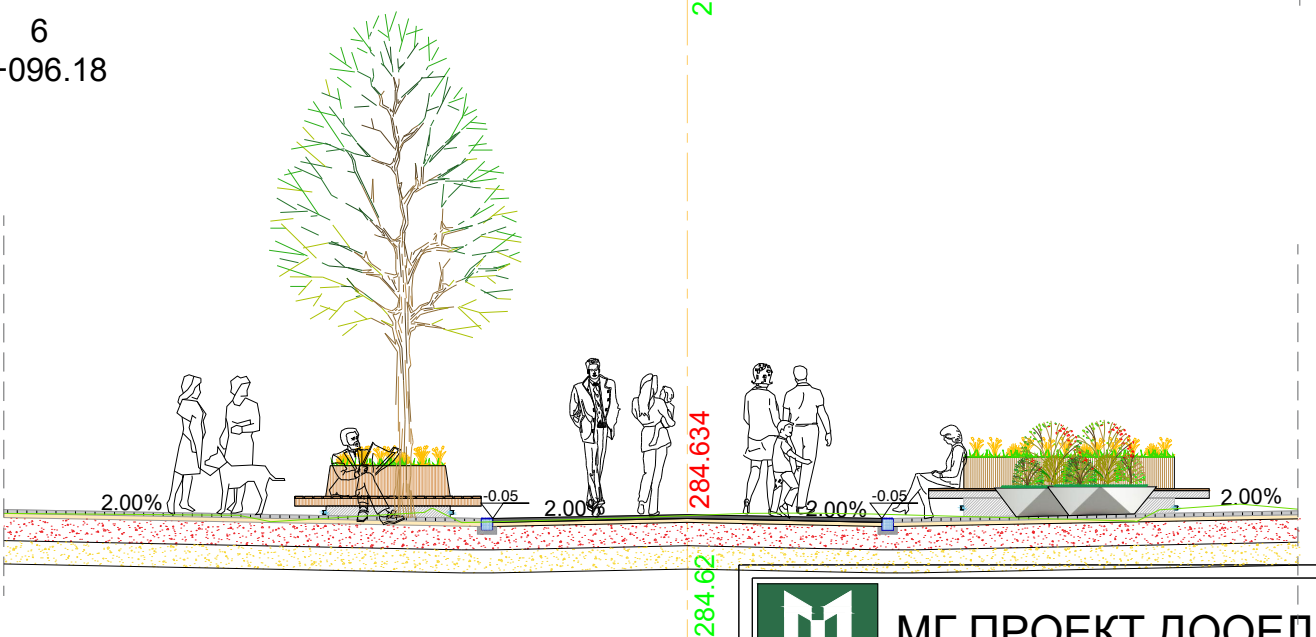

МГ ПРОЕКТ ДООЕЛ СКОПЈЕ


ИНВЕСТИТОР	ОПШТИНА ШТИП		
ОБЈЕКТ	ОП ЗА ИЗГРАДБА НА ПЕШАЧКА УЛИЦА ДЕЛ ОД УП.ВАНЧО ПРКЕ ДЕЛ ОД КП7505/1 И ДЕЛ ОД КП7153/1 КО ШТИП 5		
ЦРТЕЖ	ПОПРЕЧНИ ПРЕСЕЦИ		
ФАЗА	УЛИЦИ	5.1	
ДАТА 2024	М 1:100		
	БР.НА ЦРТЕЖ		

ОСНОВЕН ПРОЕКТ	ПРОЕКТАНТИ	А
	ОДГОВОРЕН ПРОЕКТАНТ МИА: КРИСТИНА ПАВЛЕСКА	
СОРАБОТНИЦИ	ДГИ: САШО ТЕРЗИОСКИ	
ТЕХ.БР.	ОП -67/24	

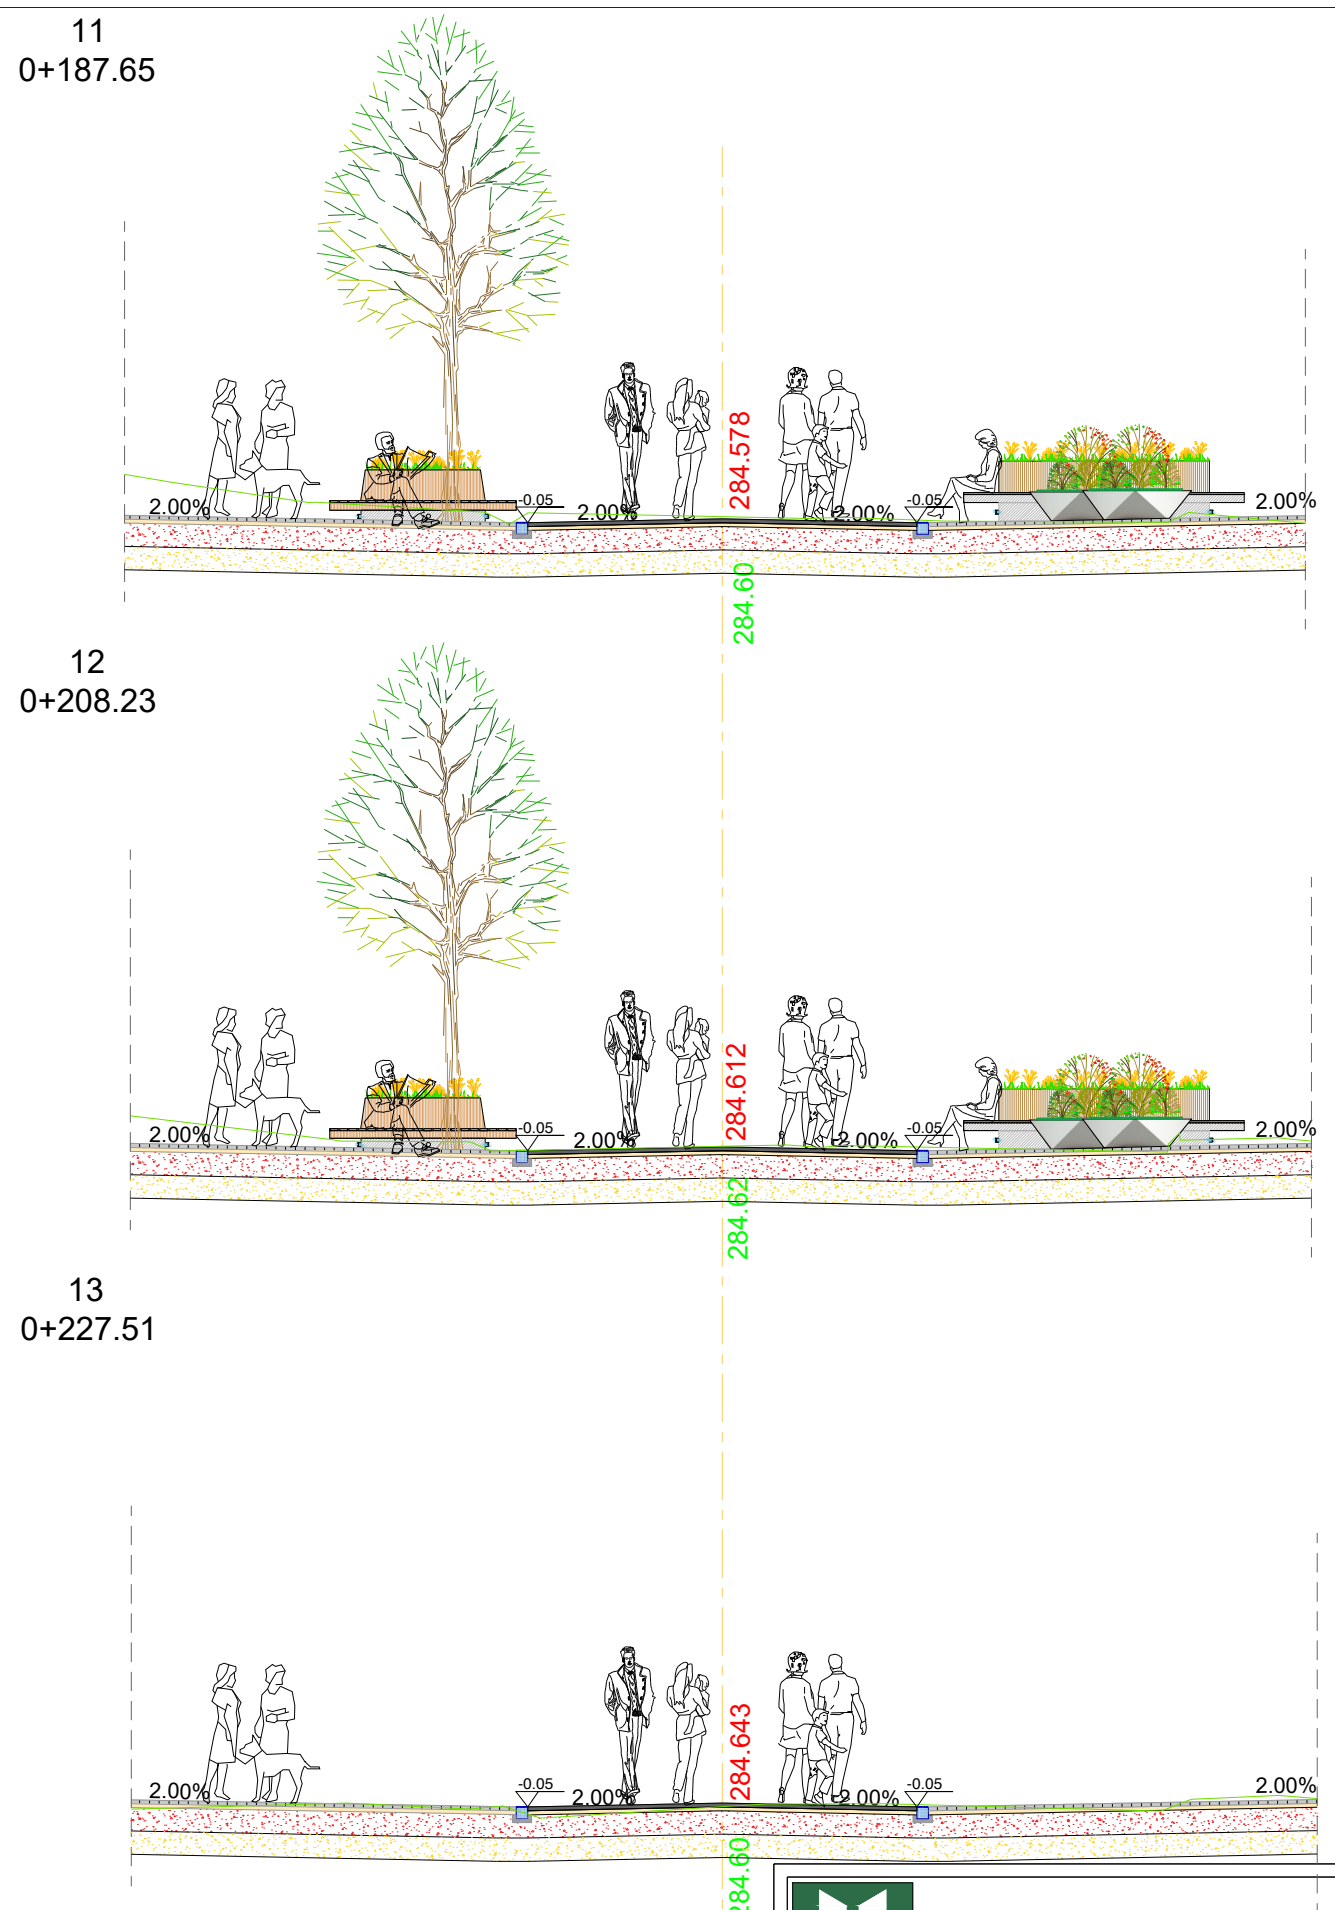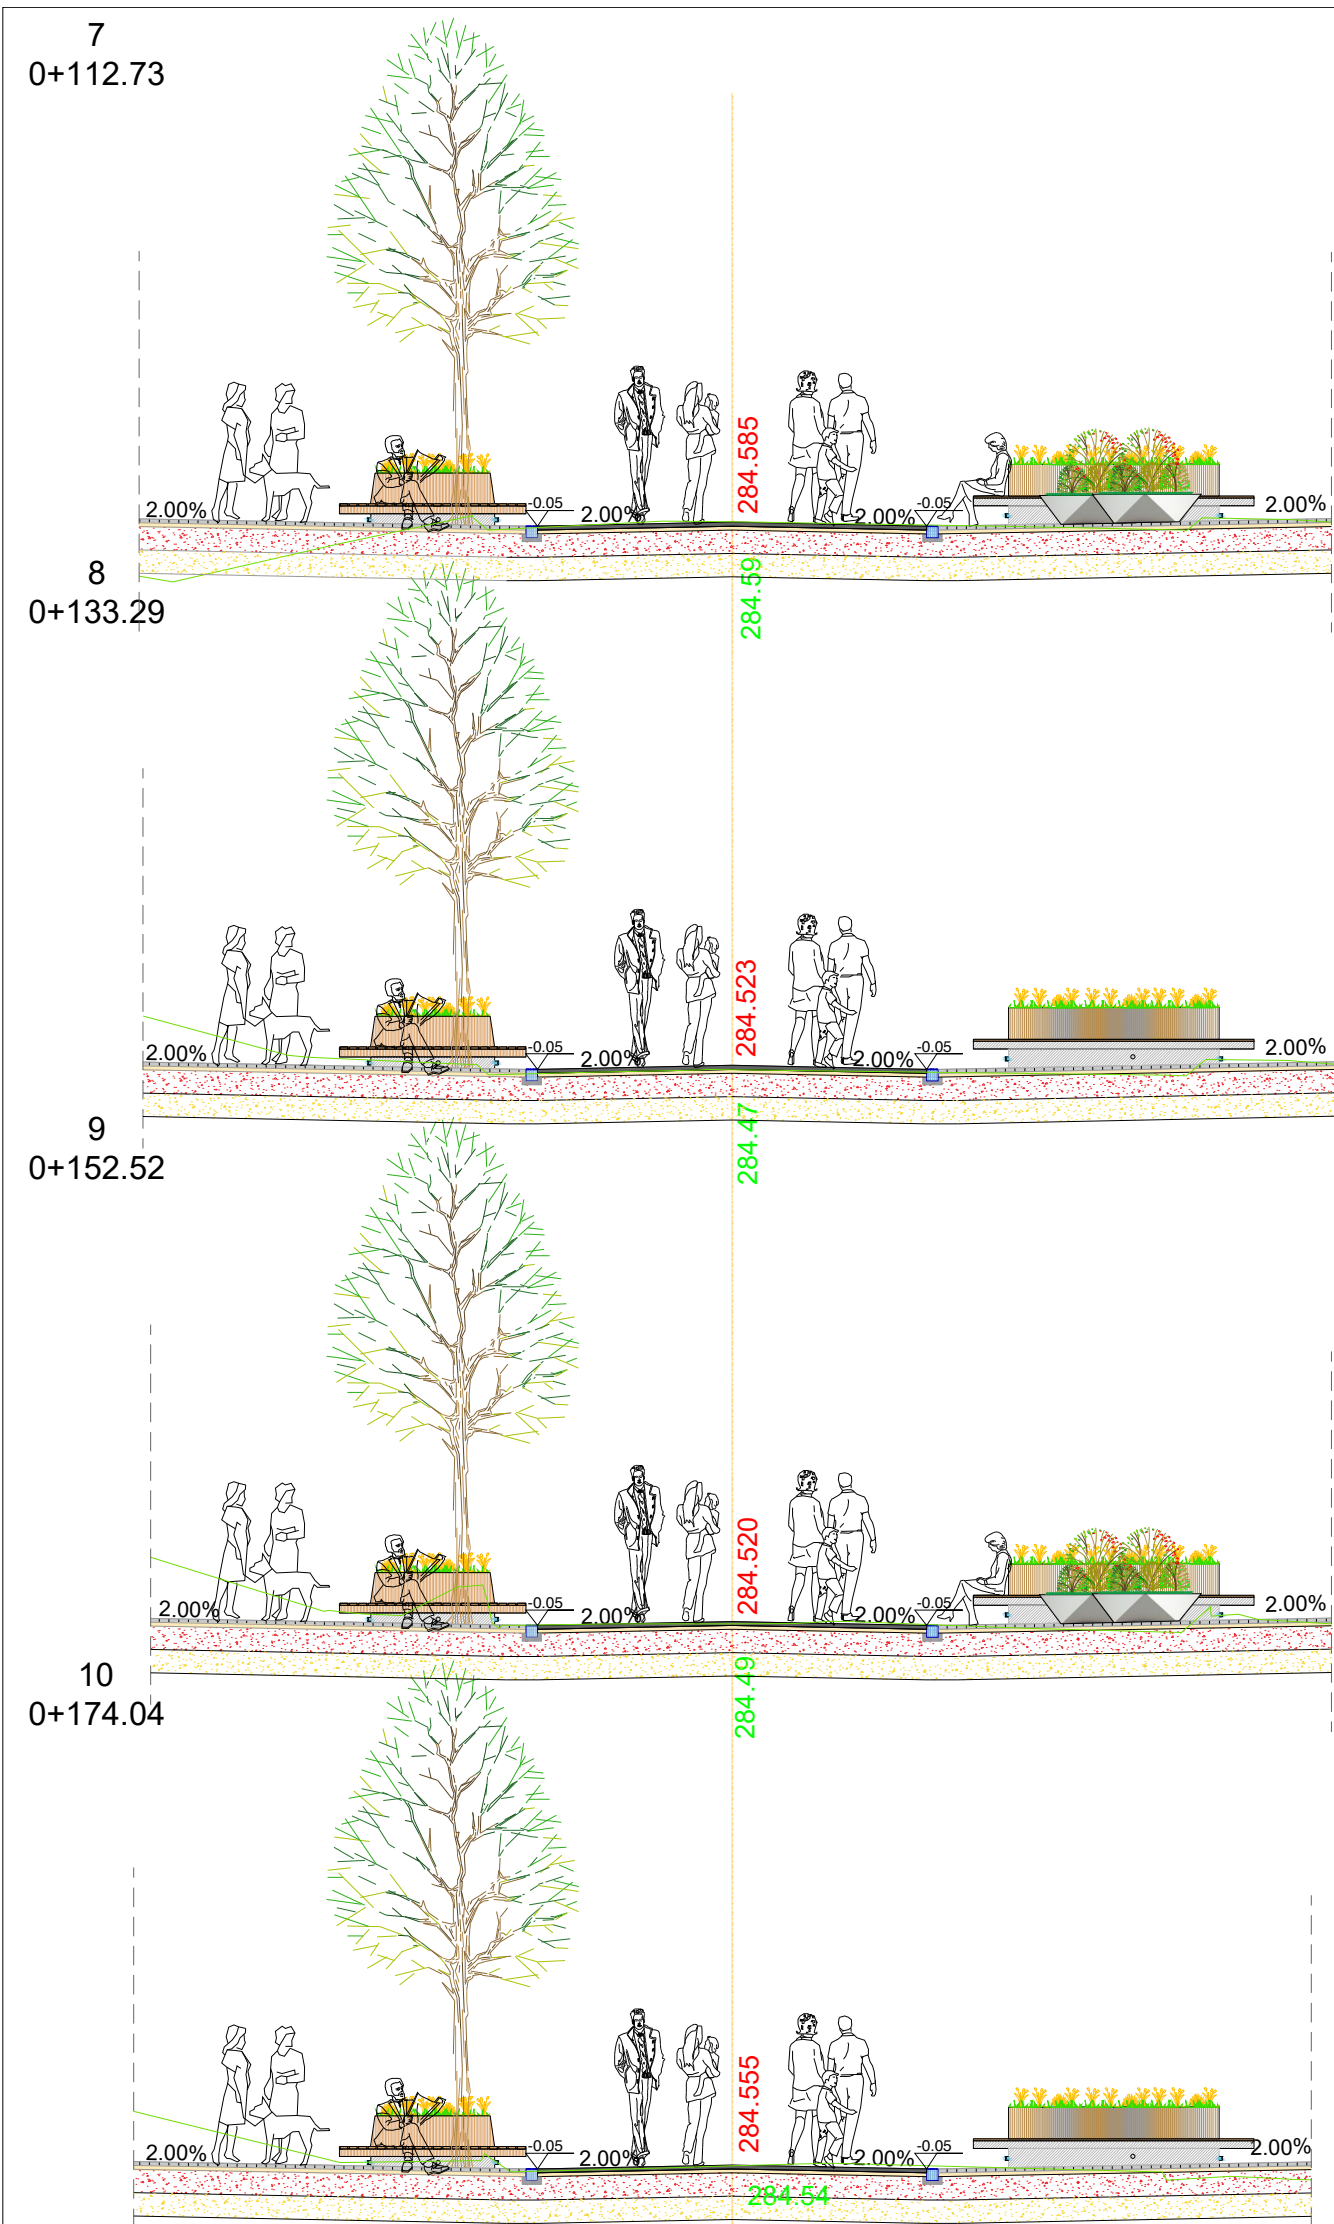

 МГ ПРОЕКТ ДООЕЛ СКОПЈЕ			
ИНВЕСТИТОР	ОПШТИНА ШТИП		
ОБЈЕКТ	ОП ЗА ИЗГРАДБА НА ПЕШАЧКА УЛИЦА ДЕЛ ОД УЛ. ВАНЧО ПРКЕ ДЕЛ ОД КП7505/1 И ДЕЛ ОД КП7153/1 КО ШТИП 5		
ЦРТЕЖ	ПОПРЕЧНИ ПРЕСЕЦИ		
ФАЗА	УЛИЦИ	5.2	
ДАТА 2024	М 1:100	БР НА ЦРТЕЖ	
ОСНОВЕН ПРОЕКТ		ПРОЕКТАНТИ	
		ОДГОВОРЕН ПРОЕКТАНТ	
		МИА:	А
		КРИСТИНА ПАВЛЕСКА	
СОРАБОТНИЦИ		ДГИ:	
		САШО ТЕРЗИОСКИ	
ТЕХ.БР.	ОП -67/24		

ПОПРЕЧЕН ПРЕСЕК НА ПЕШАЧКА ПАТЕКА

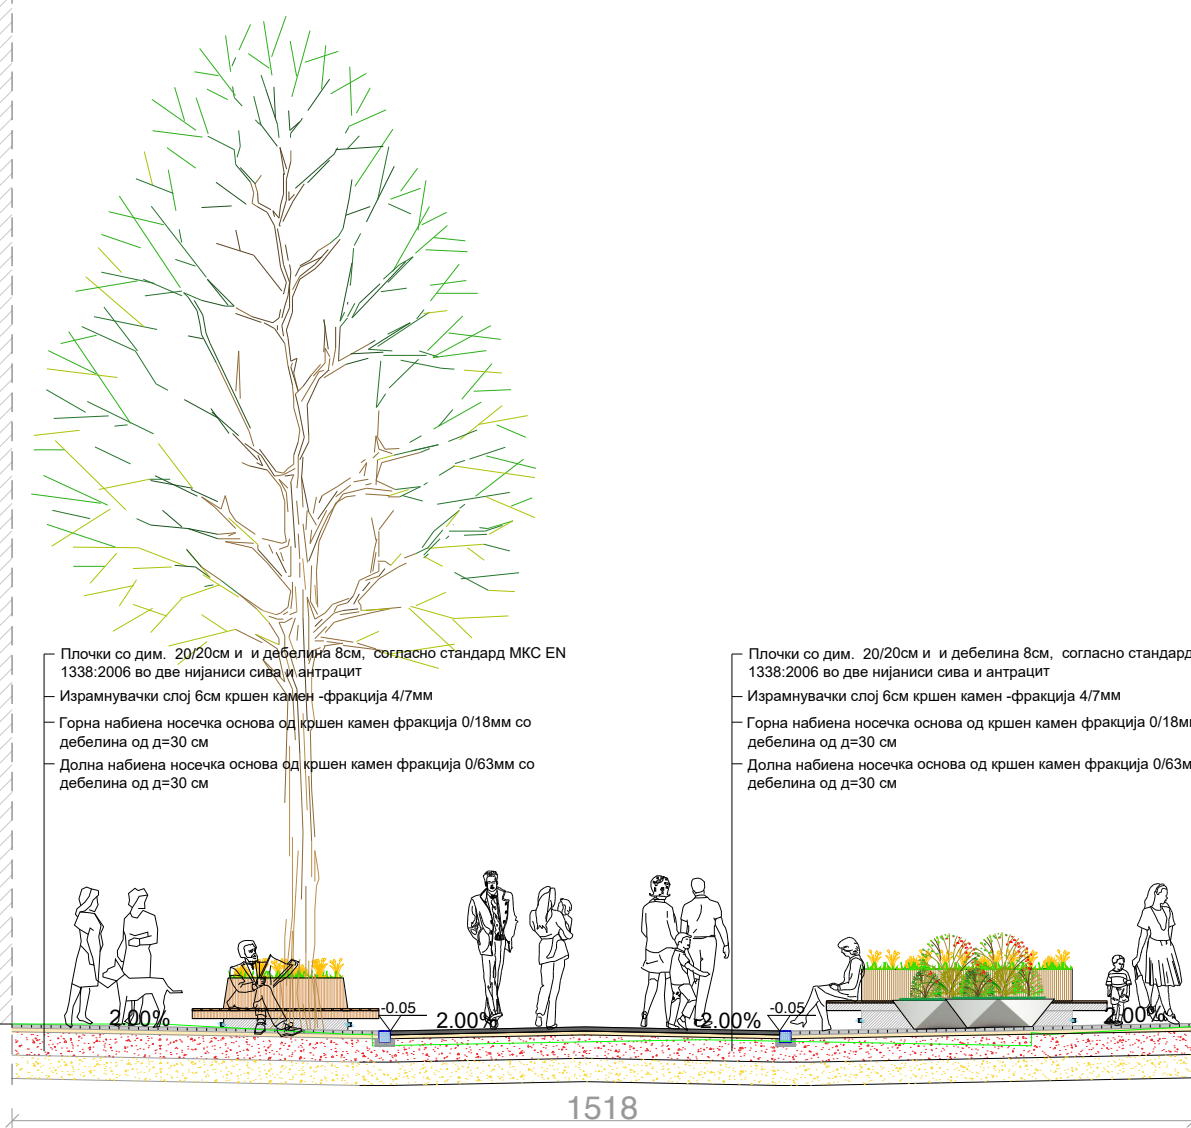


Плочки со дим. 20/20см и и дебелина 8см, согласно стандард MKC EN 1338:2006 во две нијаниси сива и антрацит
Израмнувачки слој 6см кршен камен - фракција 4/7мм
Горна набиена носечка основа од кршен камен фракција 0/18мм со дебелина од д=30 см
Долна набиена носечка основа од кршен камен фракција 0/63мм со дебелина од д=30 см

Плочки со дим. 20/20см и и дебелина 8см, согласно стандард MKC EN 1338:2006 во две нијаниси сива и антрацит
Израмнувачки слој 6см кршен камен - фракција 4/7мм
Горна набиена носечка основа од кршен камен фракција 0/18мм со дебелина од д=30 см
Долна набиена носечка основа од кршен камен фракција 0/63мм со дебелина од д=30 см

		МГ ПРОЕКТ ДООЕЛ СКОПЈЕ	
ИНВЕСТИТОР	ОПШТИНА ШТИП	ОСНОВЕН ПРОЕКТ	ПРОЕКТАНТ
ОБЈЕКТ	ОПШТИНА ШТИП - ПЕШАЧКА ПАТЕКА	ПРОЕКТАНТ	МИКЕ КРИСТИНА ПАВЛЕСКА
ЦРТЕЖ	КАРАКТЕРИСТИЧЕН ПОПРЕЧЕН ПРЕСЕК	СОРАБОТНИЦИ	ДИЖ. САНКО ТЕРЗИЌСКИ
ФАЗА	УПИЦИ	ТЕХ.БП.	ОП-67/24
ДАТА 2024	М 1:100	БР НА ЦРТЕЖ	5.3

ДЕТАЛ 1 - ЖАРДИЊЕРА

ОСНОВА

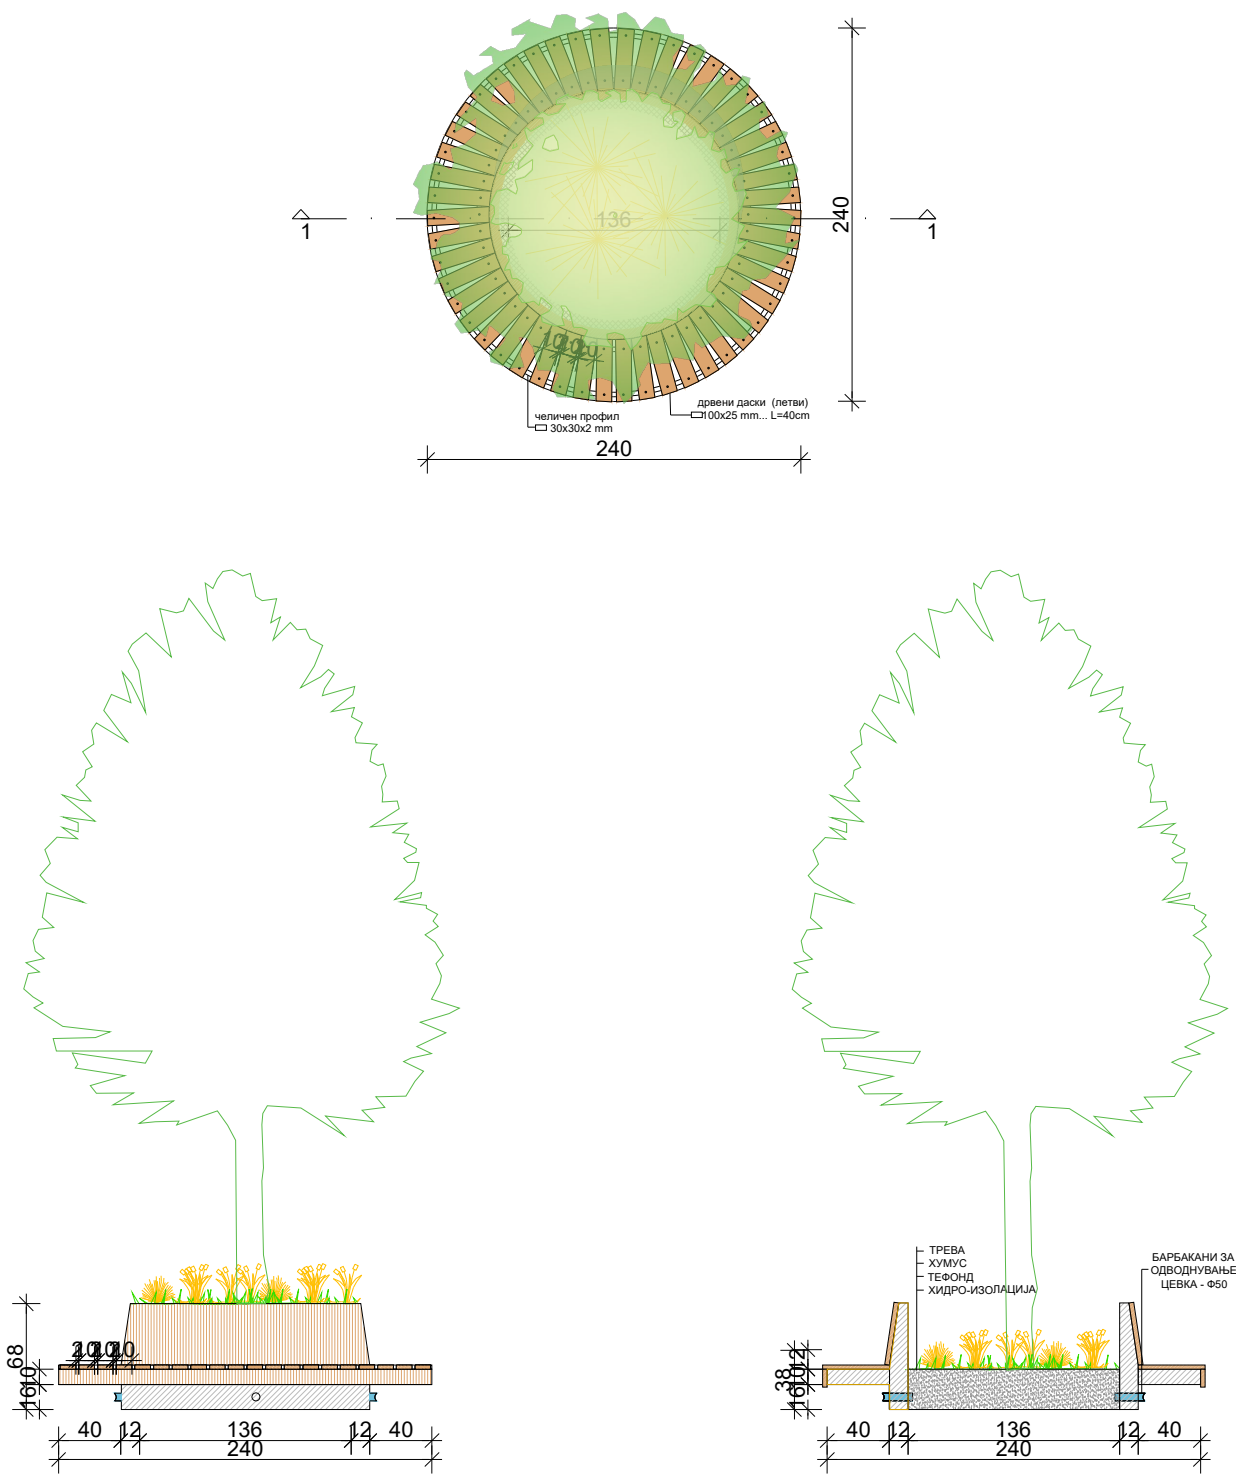




ИЗГЛЕД

ПРЕСЕК 1-1


МГ ПРОЕКТ ДООЕЛ СКОПЈЕ

ИНВЕСТИТОР	ОПШТИНА ШТИП		ОСНОВЕН ПРОЕКТ	ПРОЕКТАНТИ	А
ОБЈЕКТ	ОП ЗА ИЗГРАБДА НА ПЕШАЧКА УЛИЦА ДЕЛ ОД УЛ.ВАНЧО ПРКЕ			ОДГОВОРЕН ПРОЕКТАНТ	
	ДЕЛ ОД КП7505/1 И ДЕЛ ОД КП7153/1 КО ШТИП 5			МИА: КРИСТИНА ПАВЛЕСКА	
ЦРТЕЖ	ДЕТАЛ 1 - ЖАРДИЊЕРА КЛУПА ОКОЛУ СТЕБЛО		СОРАБОТНИЦИ	ДГИ: САШО ТЕРЗИОСКИ	
ФАЗА	УЛИЦИ			ТЕХ.БР.	ОП -67/24
ДАТА 2024	М 1:50	БР.НА ЦРТЕЖ	6		


ДЕТАЛ 2 - ЖАРДИЊЕРИ ОСНОВА

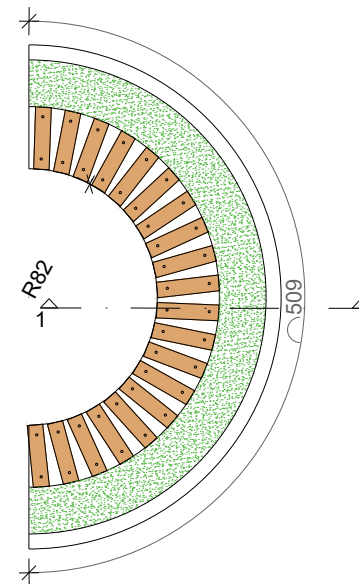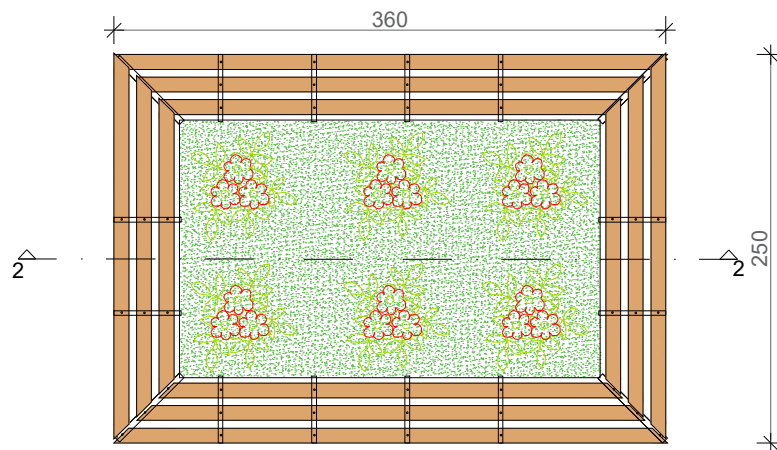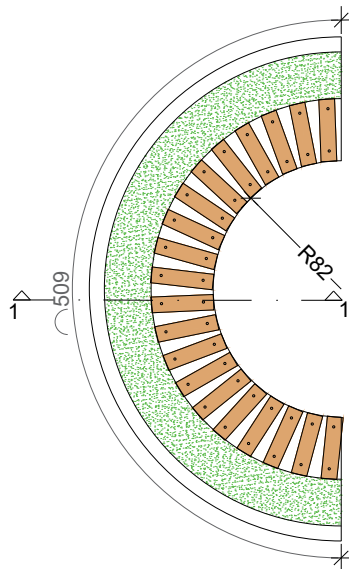


ПРЕСЕК 1-1

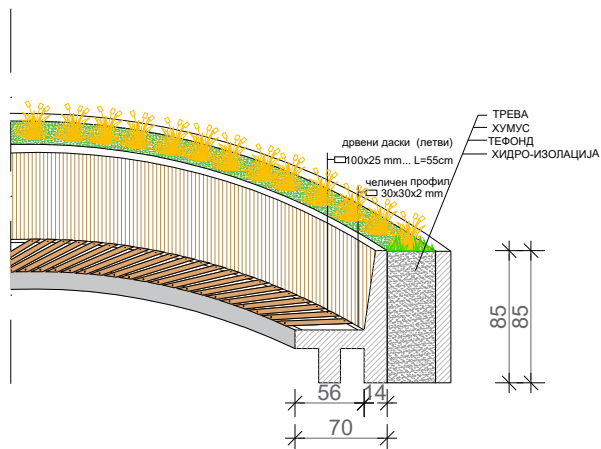

ИЗГЛЕД

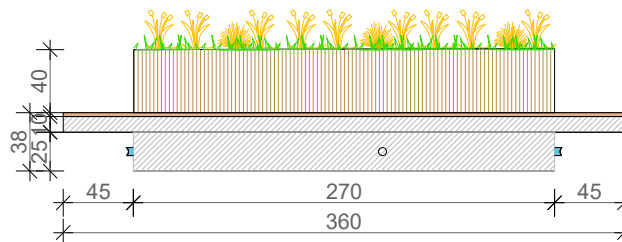

ПРЕСЕК 2-2

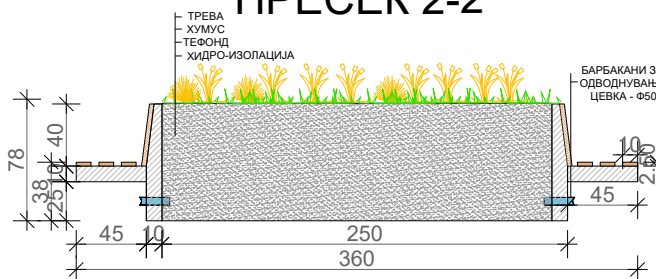

МГ ПРОЕКТ ДООЕЛ СКОПЈЕ

ИНВЕСТИТОР	ОПШТИНА ШТИП	ОСНОВЕН ПРОЕКТ	ПРОЕКТАНТИ	
ОБЈЕКТ	ОП ЗА ИЗГРАДБА НА ПЕШАЧКА УЛИЦА ДЕЛ ОД УЛ. ВАНЧО ПРКЕ ДЕЛ ОД КП7505/1 И ДЕЛ ОД КП7153/1 КО ШТИП 5		ОДГОВОРЕН ПРОЕКТАНТ	
ЦРТЕЖ	ДЕТАЛ 2 - ЖАРДИЊЕРИ ПРАВОАГОЛНА И ПОЛУКРУГ		МИА: КРИСТИНА ПАВЛЕСКА	A
ФАЗА	УЛИЦИ		ДГИ: САШО ТЕРЗИОСКИ	
ДАТА 2024	М 1:50	БР. НА ЦРТЕЖ	ТЕХ. БР.	ОП -67/24
		7		

ДЕТАЛ 3 НА КЛУПА

ОСНОВА

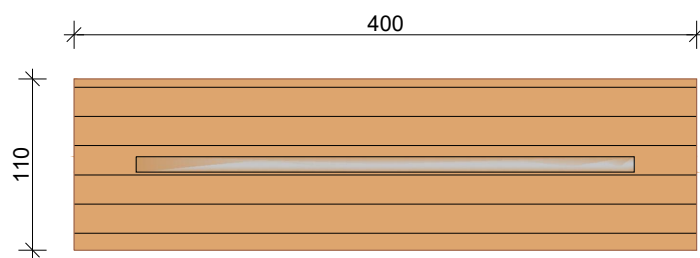


ФОТО ПРИКАЗ



Карактеристики:

Димензии: 400/110/78см

Материјали: челичен лим д=8мм

дрвени даски - егзотично дрво



МГ ПРОЕКТ ДООЕЛ СКОПЈЕ

ИНВЕСТИТОР	ОПШТИНА ШТИП		ОСНОВЕН ПРОЕКТ	ПРОЕКТАНТИ	А
ОБЈЕКТ	ОП ЗА ИЗГРАДБА НА ПЕШАЧКА УЛИЦА ДЕЛ ОД УЛ.ВАНЧО ПРКЕ			ОДГОВОРЕН ПРОЕКТАНТ	
	ДЕЛ ОД КП7505/1 И ДЕЛ ОД КП7153/1 КО ШТИП 5			миа: КРИСТИНА ПАВЛЕСКА	
ЦРТЕЖ	ДЕТАЛ 3 НА КЛУПИ ЗА СЕДЕЊЕ			СОРАБОТНИЦИ	
ФАЗА	УЛИЦИ	8		дги: САШО ТЕРЗИОСКИ	
ДАТА 2024	М 1:50		БР.НА ЦРТЕЖ	ТЕХ.БР.	
				ОП -67/24	

ДЕТАЛ 4 НА ЖАРДИЊЕРА

ОСНОВА


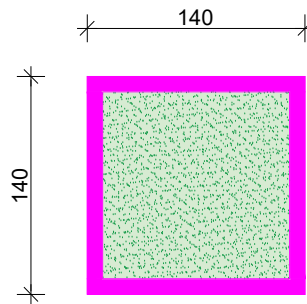


ФОТО ПРИКАЗ

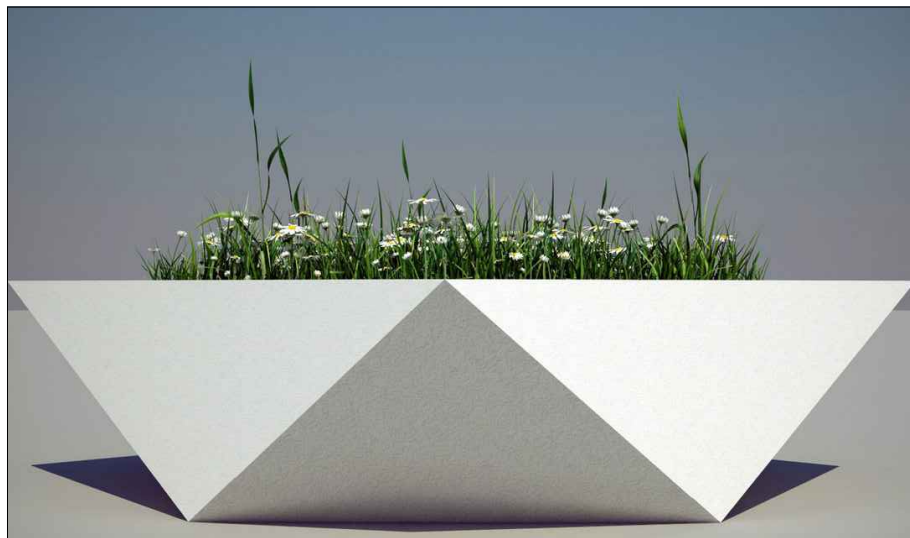

Карактеристики:


Димензии: 140/140см

Материјали: челичен лим д=5мм




МГ ПРОЕКТ ДООЕЛ СКОПЈЕ


ИНВЕСТИТОР	ОПШТИНА ШТИП			ОСНОВЕН ПРОЕКТ	ПРОЕКТАНТИ	А
ОБЈЕКТ	ОП ЗА ИЗГРАДБА НА ПЕШАЧКА УЛИЦА ДЕЛ ОД УЛ.ВАНЧО ПРКЕ ДЕЛ ОД КП7505/1 И ДЕЛ ОД КП7153/1 КО ШТИП 5				ОДГОВОРЕН ПРОЕКТАНТ МИА: КРИСТИНА ПАВЛЕСКА	
ЦРТЕЖ	ДЕТАЛ 4 НА МЕТАЛНИ ЖАРДИЊЕРИ			СОРАБОТНИЦИ		
ФАЗА	УЛИЦИ				ДИ: САШО ТЕРЗИОСКИ	
ДАТА 2024	М 1:50	БР.НА ЦРТЕЖ	9		ТЕХ.БР.	

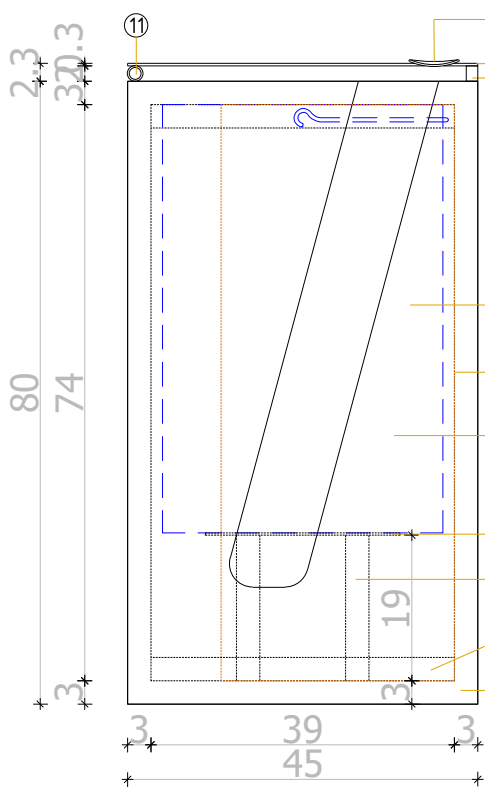

ПРЕДЕН ИЗГЛЕД

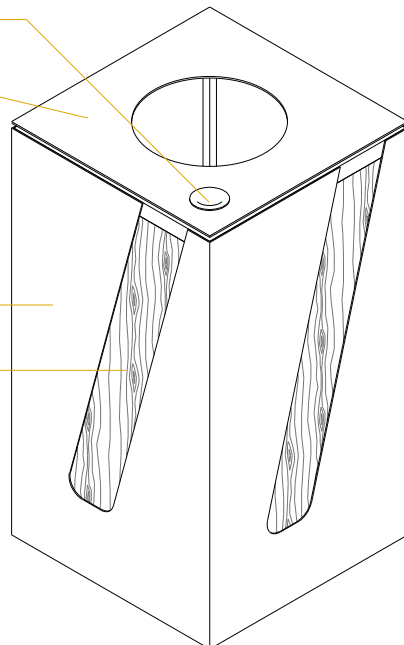

АКСОНОМЕТРИСКИ ПРИКАЗ

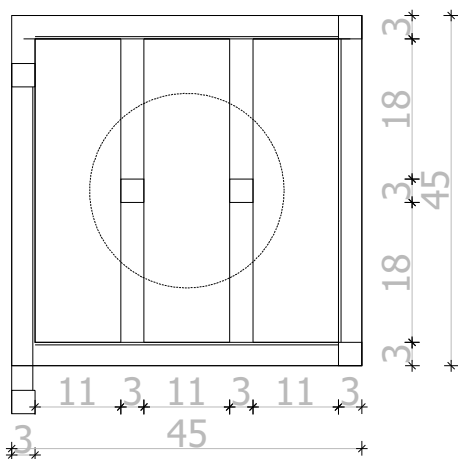

ОСНОВА

1. ЧЕЛИЧЕН ПРОФИЛ 30/30MM
2. ФЛАХ 390/30/3MM
3. НОГАРКА ЧЕЛИЧЕН ПРОФИЛ 30/30MM
4. ЧЕЛИЧЕН ЛИМ Д=3MM, Ø250
5. КОРИТО ОД ЧЕЛИЧЕН ЛИМ СО РАЧКА Д=0.8MM, Ø360/550MM
6. ДРВЕНА ДАСКА(ИРОКО) 20/100/740MM
7. МАСКА ОД ЧЕЛИЧЕН ЛИМ Д=2MM(ОБРАБОТКА НА СНС)
8. ДИСТАНЦЕР НА КАПАК, ЧЕЛИЧНА ШИПКА Ø15/20MM
9. КАПАК ОД ЧЕЛИЧЕН ЛИМ 450/450/3MM, ОТВОР Ø250
10. ПЕПЕЛНИК ОД ЧЕЛИЧЕН ЛИМ Д=1MM Ø60/12MM
11. ШАРКА ЗА КАПАК Ø20/100MM

КОНСТРУКЦИЈАТА Е:

-ПОЦИНКУВАНА И ЕЛЕКТРОСТАТСКИ БОЈАДИСАНА (ГРАФИТНА БОЈА)
-МИНИЗИРАНА И ДВОЈНО БОЈАДИСАНА(ГРАФИТНА-АНТИКА БОЈА)

ДРВОТО Е ТРЕТИРАНО СО ОСНОВНА ИМПРЕГНАЦИЈА ЗА ДРВО И ПРЕМАЗ ЗА ДРВО
НИЈАНСИРАН ВО ТИКА, ХРАСТ ИЛИ ОРЕВ.

НАПОМЕНА

ШРАФЕЊЕ НА ДРВО ОД ВНАТРЕШНА СТРАНА (САМОРЕЗНИ СО ФРЕЗИНГ ГЛАВА)



МГ ПРОЕКТ ДООЕЛ СКОПЈЕ

ИНВЕСТИТОР	ОПШТИНА ШТИП	ОСНОВЕН ПРОЕКТ	ПРОЕКТАНТИ	
			ОДГОВОРЕН ПРОЕКТАНТ	МИА:
ОБЈЕКТ	ОП ЗА ИЗГРАДБА НА ПЕШАЧКА УЛИЦА ДЕЛ ОД УЛ.ВАНЧО ПРКЕ ДЕЛ ОД КП7505/1 И ДЕЛ ОД КП7153/1 КО ШТИП 5		КРИСТИНА ПАВЛЕСКА	А
ЦРТЕЖ	ДЕТАЛ 5 НА КОРПИ ЗА ОТПАДОЦИ		ДГИ: САШО ТЕРЗИОСКИ	
ФАЗА	УЛИЦИ			
ДАТА 2024	М 1:100	БР.НА ЦРТЕЖ	ТЕХ.БР.	ОП -67/24
		10		


Полукружни полимерни бетонски каналчиња (решетка за атмосферски води) со
светол отвор 15см и висина 15см, со носивост до 250KN. (L=227.5m x2)
Заедно со монтажа на лиено железна решетка врз каналињата со класа на
носивост C250






МГ ПРОЕКТ ДООЕЛ СКОПЈЕ

ИНВЕСТИТОР	ОПШТИНА ШТИП		
ОБЈЕКТ	ОП ЗА ИЗГРАДБА НА ПЕШАЧКА УЛИЦА ДЕЛ ОД УЛ.ВАНЧО ПРКЕ ДЕЛ ОД КП7505/1 И ДЕЛ ОД КП7153/1 КО ШТИП 5		
ЦРТЕЖ	ДЕТАЛ НА РЕШЕТКА ЗА АТМ. ВОДИ		
ФАЗА	УЛИЦИ	11	
ДАТА 2024	М 1:100		
	БР.НА ЦРТЕЖ		

ОСНОВЕН ПРОЕКТ	ПРОЕКТАНТИ	А
	ОДГОВОРЕН ПРОЕКТАНТ МИА: КРИСТИНА ПАВЛЕСКА	
СОРАБОТНИЦИ	ДИ: САШО ТЕРЗИОСКИ	
ТЕХ.БР.	ОП -67/24	

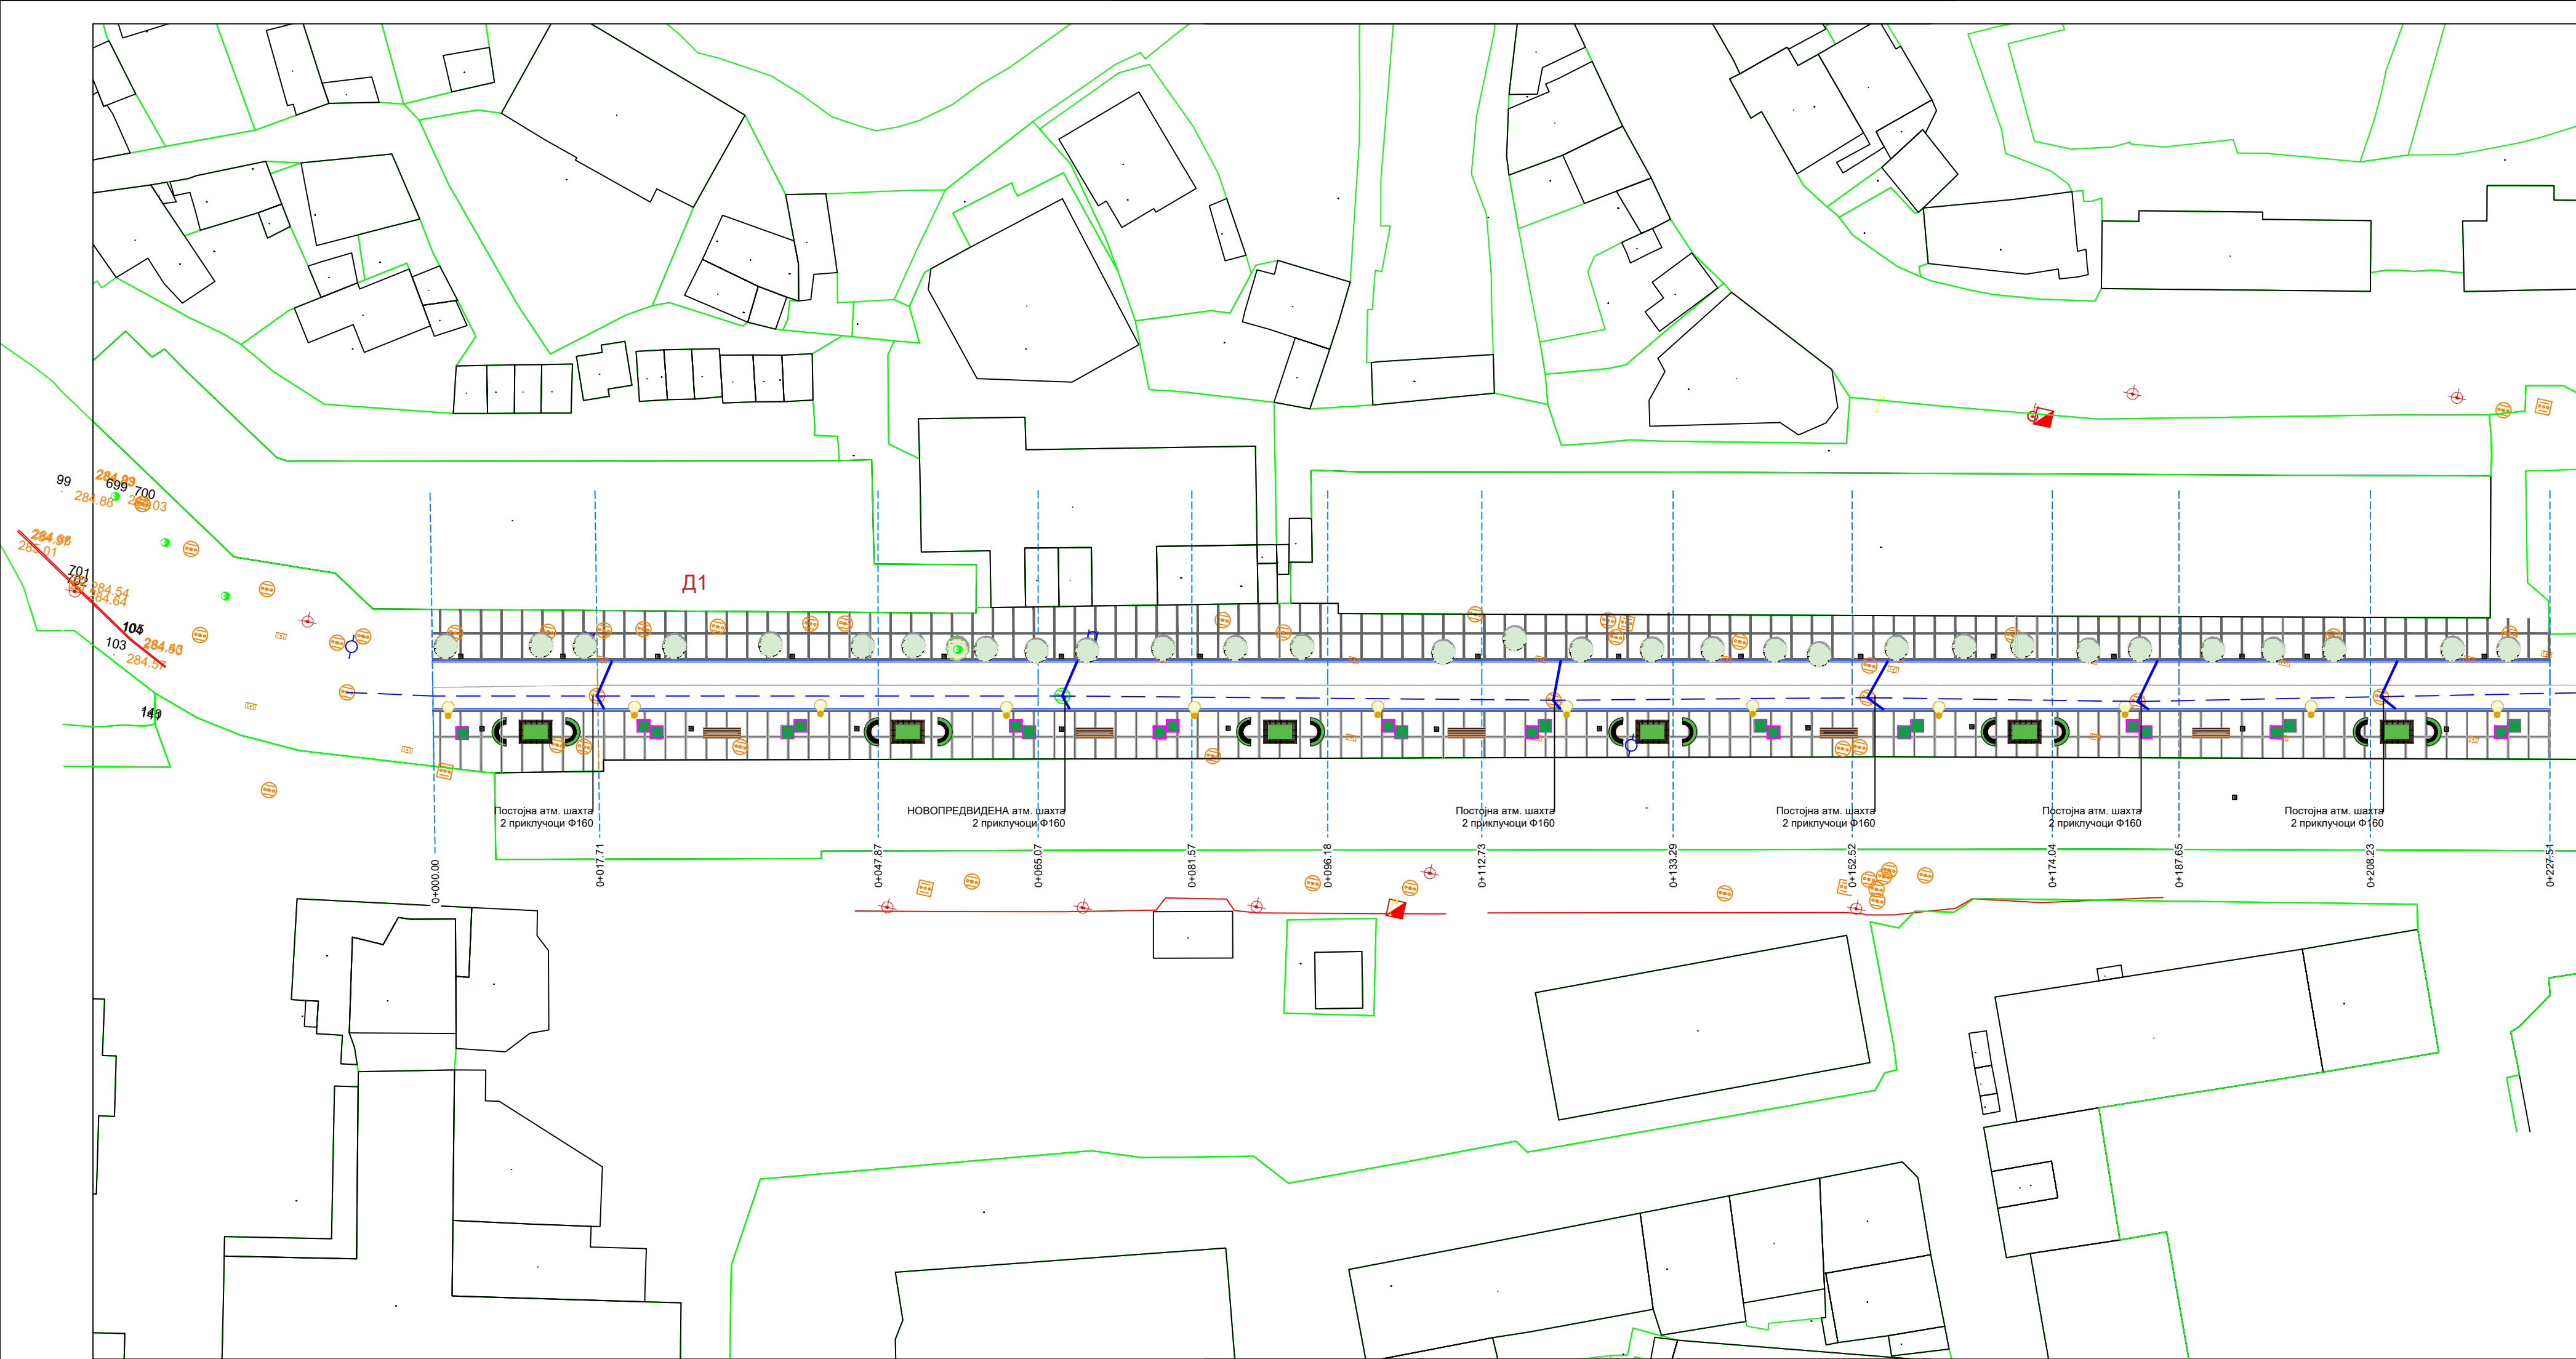

ЛЕГЕНДА:

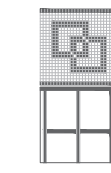 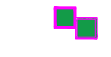-  Поплочена површина Плочки 20/20см, дебелина д=8см, редени во 2 бои сива и антрацит сива боја, по дадена шема.
-  Решетка за атмосферски води, светол отвор 15см и висина 15см, со носивост до 250KN.
-  Бетонски жардињери (ДЕТАЛ 1)
-  Бетонски жардињери (ДЕТАЛ 2)
-  Парковски клупи (ДЕТАЛ 3)
-  Жардињера (ДЕТАЛ 4)
-  Парковски корпи за отпадоци (ДЕТАЛ 5)
-  ПОЗИЦИЈА НА СВЕТИЛКА
-  НОВА АТМОСФЕРСКА ШАХТА ЗА ПРИФАЌАЊЕ НА АТМОСФЕРСКИТЕ ВОДИ ОД СЛИВНИТЕ КАНАЛИ
-  ПОСТОЕЧКИ АТМОСФЕРСКИ ШАХТИ
-  ПРИКЛУЧНИ ЦЕВКИ Ф160 ОД СЛИВНИ КАНАЛИЧИЊА ДО НАЈБЛИСКА АТМОСФЕРСКА ШАХТА



ИНВЕСТИТОР	ОПШТИНА ШТИП	ОСНОВЕН ПРОЕКТ	ПРОЕКТАНТИ
ОБЈЕКТ	ОП ЗА ИЗГРАДБА НА ПЕШАЧКА УЛИЦА ДЕЛ ОД УЛ.ВАНЧО ПРКЕ ДЕЛ ОД КЛП7596/1 И ДЕЛ ОД КЛП7153/1 КО ШТИП Б.	ОДГОВОРЕН ПРОЕКТАНТ	МИА: КРИСТИНА ПАВЛЕСКА
ЦРТЕЖ	СИТУАЦИЈА СО СЛИВНИ ПРИКЛУЧОЦИ ЗА АТМ. КАЊ.	СОРАБОТНИЦИ	ДЛГ: САШО ТЕРЗИОСКИ
ФАЗА	УЛИЦИ	ТЕХ.БР.	ОП-67/24
ДАТА 2024	М 1:500 БР НА ЦРТЕЖ		