

НАРАЧАТЕЛ:

Општина Центар - Скопје

ЛОКАЦИЈА:

Општина Центар, Скопје

ПРОЕКТ:

Основен проект за реконструкција (рехабилитација) на постоечка улична мрежа за улици „Донбас“, „Андон Дуков“, „Алберт Ајнштајн“, Општина Центар - Скопје

ПРОЕКТ:

ПАТИШТА


Г

ТЕХНИЧКИ БРОЈ:

ИНГ. 006 - 02 - 19

ДАТУМ:

Февруари, 2019

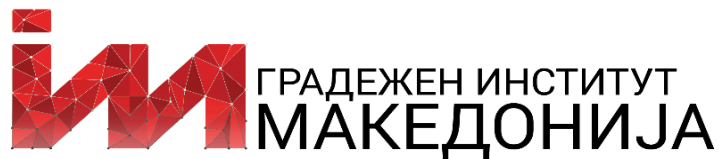


**ул. Дрезденска бр.52, 1000 Скопје
Република Македонија**

тел: +389 2 3066 836 / +389 2 3066 816
факс: 02 3066 828

web: www.gim.com.mk
e-mail: giminz@gim.com.mk

ГРАФИЧКИ ПРИЛОЗИ

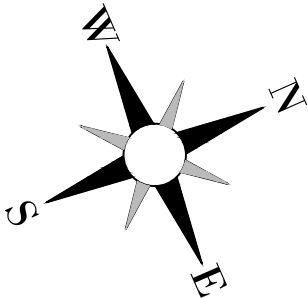

■ електро ормар

● вововод приклучок

шахта со четириаголен капак

шахта со кружен капак

сливник

■ асфалтна подлога

⊕ бетонска сл. бандера

⊕ дрвена сл. бандера

⊕ канделабра



рампа за влез

— Улици

— Објекти

— Ограда

△ 227.190
PRI

Полигонска точка

• 266.66
1137

Детална точка

— Изохипси

Полигонски точки			
Број на точка	Y	X	Z
P1002	7535198.161	4651016.147	248.441
P1508	7535010.604	4650747.525	249.469
P1000	7535047.671	4561080.611	248.02
P1001	7535085.595	4651152.056	248.297
P1106	7535024.968	4651174.348	248.056
P1399	7535001.602	4651112.587	248.242


РЕВИЗИЈА / РЕВИДЕНТ:	ДАТУМ:	ПОТПИС НА РЕВИДЕНТ:	ПЕЧАТ НА РЕВИДЕНТ:
ГРАДЕЖЕН ИНСТИТУТ "МАКЕДОНИЈА" А.Д. Ул. "Дрезденска" бр.52, 1000 Скопје, Република Македонија ЊСБ: ЊЊЊ.ГИМ.ЦОМ.МК			
ИНВЕСТИТОР: ОПШТИНА ЦЕНТАР		ОБЈЕКТ: ОСНОВЕН ПРОЕКТ ЗА РЕКОНСТРУКЦИЈА (РЕХАБИЛИТАЦИЈА) НА ПОСТОЕЧКА УЛИЧНА МРЕЖА ЗА УЛИЦИ „ДОНБАС“, „АНДОН ДУКОВ“, „АЛБЕРТ АЈНШТАЈН“, ОПШТИНА ЦЕНТАР - СКОПЈЕ	ПЕЧАТ НА ОДГОВОРЕН ПРОЕКТАНТ:
ПРОЕКТ: ОСНОВЕН ПРОЕКТ		ОДГОВОРЕН ПРОЕКТАНТ: м-р Драганчо Волчески дипл.град.инж	ПОТПИС НА ОДГОВОРЕН ПРОЕКТАНТ:
ФАЗА НА ПРОЕКТИРАЊЕ: ПАТИШТА	Г	ПРОЕКТАНТИ: м-р Драганчо Волчески дипл.град.инж	ПОТПИС:
СОДРЖИНА НА ЛИСТ: СИТУАЦИЈА - ПОСТОЕЧКА СОСТОЈБА		СОРАБОТНИЦИ: м-р Ивона Недевска, дипл.град.инж. Бејан Моукоч, дипл.град.инж. м-р Андреј Матевски, дипл.град.инж. Александра Делова, дипл.град.инж	ПОТПИС:
ТЕХНИЧКИ БРОЈ НА ПРОЕКТОТ: ИНГ: 006 - 02 - 19		ДАТУМ: ФЕВРУАРИ 2019	РАЗМЕР: М = 1 : 500
ФОРМАТ: 297/580		БРОЈ НА ЛИСТ: 01	



РЕВИЗИЈА / РЕВИДЕНТ:		ДАТУМ:		ПОТПИС НА РЕВИДЕНТ:		ПЕЧАТ НА РЕВИДЕНТ:		
 ГРАДЕЖЕН ИНСТИТУТ "МАКЕДОНИЈА" А.Д. Ул. "Дрезденска" бр.52, 1000 Скопје, Република Македонија ЊСБ: ЊЊЊ.ГИМ.ЦОМ.МК								
ИНВЕСТИТОР: ОПШТИНА ЦЕНТАР			ОБЈЕКТ: ОСНОВЕН ПРОЕКТ ЗА РЕКОНСТРУКЦИЈА (РЕХАБИЛИТАЦИЈА) НА ПОСТОЕЧКА УЛИЧНА МРЕЖА ЗА УЛИЦИ „ДОНБАС“, „АНДОН ДУКОВ“, „АЛБЕРТ АЈНШТАЈН“, ОПШТИНА ЦЕНТАР - СКОПЈЕ			ПЕЧАТ НА ОДГОВОРЕН ПРОЕКТАНТ:		
ПРОЕКТ: ОСНОВЕН ПРОЕКТ			ОДГОВОРЕН ПРОЕКТАНТ: м-р Драганчо Волчески дипл.град.инж			ПОТПИС НА ОДГОВОРЕН ПРОЕКТАНТ: 		
ФАЗА НА ПРОЕКТИРАЊЕ: ПАТИШТА		Г		ПРОЕКТАНТИ: м-р Драганчо Волчески дипл.град.инж		ПОТПИС: 		
СОДРЖИНА НА ЛИСТ: СИТУАЦИЈА - ХОРИЗОНТАЛНО РЕШЕНИЕ			СОРАБОТНИЦИ: м-р Ивона Недевска , дипл.град.инж. Бејан Моукоч , дипл.град.инж. м-р Андреј Матевски , дипл.град.инж. Александра Делова, дипл.град.инж			ПОТПИС:		
ТЕХНИЧКИ БРОЈ НА ПРОЕКТОТ: ИНГ: 006 - 02 - 19			ДАТУМ: ФЕВРУАРИ 2019		РАЗМЕР: М = 1 : 500		ФОРМАТ: 297/580	БРОЈ НА ЛИСТ: 02




РЕВИЗИЈА / РЕВИДЕНТ:		ДАТУМ:	ПОТПИС НА РЕВИДЕНТ:	ПЕЧАТ НА РЕВИДЕНТ:
ГРАДЕЖЕН ИНСТИТУТ „МАКЕДОНИЈА“ А.Д. Ул. „Дрезденска“ бр.52, 1000 Скопје, Република Македонија web: www.gim.com.mk				
ИНВЕСТИТОР: ОПШТИНА ЦЕНТАР		ОБЈЕКТ: ОСНОВЕН ПРОЕКТ ЗА РЕКОНСТРУКЦИЈА (РЕХАБИЛИТАЦИЈА) НА ПОСТОЕЧКА УЛИЧНА МРЕЖА ЗА УЛИЦИ „ДОНБАС“, „АНДОН ДУКОВ“, „АЛБЕРТ АЈНШТАЈН“, ОПШТИНА ЦЕНТАР - СКОПЈЕ		ПЕЧАТ НА ОДГОВОРЕН ПРОЕКТАНТ:
ПРОЕКТ: ОСНОВЕН ПРОЕКТ		ОДГОВОРЕН ПРОЕКТАНТ: м-р Драганчо Волчески дипл.град.инж		ПОТПИС НА ОДГОВОРЕН ПРОЕКТАНТ:
ФАЗА НА ПРОЕКТИРАЊЕ: ПАТИШТА	Г	ПРОЕКТАНТИ: м-р Драганчо Волчески дипл.град.инж		ПОТПИС:
СОДРЖИНА НА ЛИСТ: СИТУАЦИЈА - НИВЕЛАЦИОНО РЕШЕНИЕ		СОРАБОТНИЦИ: м-р Ивона Недевска , дипл.град.инж. Бејан Моукоч , дипл.град.инж. м-р Андреј Матевски , дипл.град.инж. Александра Делова, дипл.град.инж		ПОТПИС:
ТЕХНИЧКИ БРОЈ НА ПРОЕКТОТ: ИНГ: 006 - 02 - 19	ДАТУМ: ФЕВРУАРИ 2019	РАЗМЕР: М = 1 : 500	ФОРМАТ: 297/580	БРОЈ НА ЛИСТ: 03

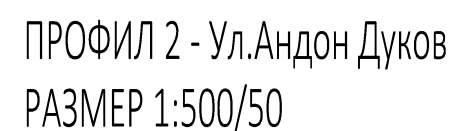





РЕВИЗИЈА / РЕВИДЕНТ:	ДАТУМ:	ПОТПИС НА РЕВИДЕНТ:	ПЕЧАТ НА РЕВИДЕНТ:
 ГРАДЕЖЕН ИНСТИТУТ "МАКЕДОНИЈА" А.Д. Ул. "Дрезденска" бр.52, 1000 Скопје, Република Македонија Њ.Њ.Њ. ГИМ.ЦОМ.МК			
ИНВЕСТИТОР: ОПШТИНА ЦЕНТАР		ОБЈЕКТ: ОСНОВЕН ПРОЕКТ ЗА РЕКОНСТРУКЦИЈА (РЕХАБИЛИТАЦИЈА) НА ПОСТОЕЧКА УЛИЧНА МРЕЖА ЗА УЛИЦИ „ДОНБАС“, „АНДОН ДУКОВ“, „АЛБЕРТ АЈНШТАЈН“, ОПШТИНА ЦЕНТАР - СКОПЈЕ	ПЕЧАТ НА ОДГОВОРЕН ПРОЕКТАНТ:
ПРОЕКТ: ОСНОВЕН ПРОЕКТ		ОДГОВОРЕН ПРОЕКТАНТ: м-р Драганчо Волчески дипл.град.инж	ПОТПИС НА ОДГОВОРЕН ПРОЕКТАНТ: 
ФАЗА НА ПРОЕКТИРАЊЕ: ПАТИШТА	Г	ПРОЕКТАНТИ: м-р Драганчо Волчески дипл.град.инж	ПОТПИС: 
СОДРЖИНА НА ЛИСТ: НАДОЛЖЕН ПРОФИЛ УЛ.АНДОН ДУКОВ		СОРАБОТНИЦИ: м-р Ивана Невевска, дипл.град.инж. Божан Моучок, дипл.град.инж. м-р Андреј Матевски, дипл.град.инж. Александра Делова, дипл.град.инж	ПОТПИС:
ТЕХНИЧКИ БРОЈ НА ПРОЕКТОТ: ИНГ: 006 - 02 - 19		ДАТУМ: ФЕВРУАРИ 2019	РАЗМЕР: М = 1 : 500/50
		ФОРМАТ:	БРОЈ НА ЛИСТ:
		420/580	04-02

ПРОФИЛ 3 - Ул.Донбас
РАЗМЕР 1:500/50

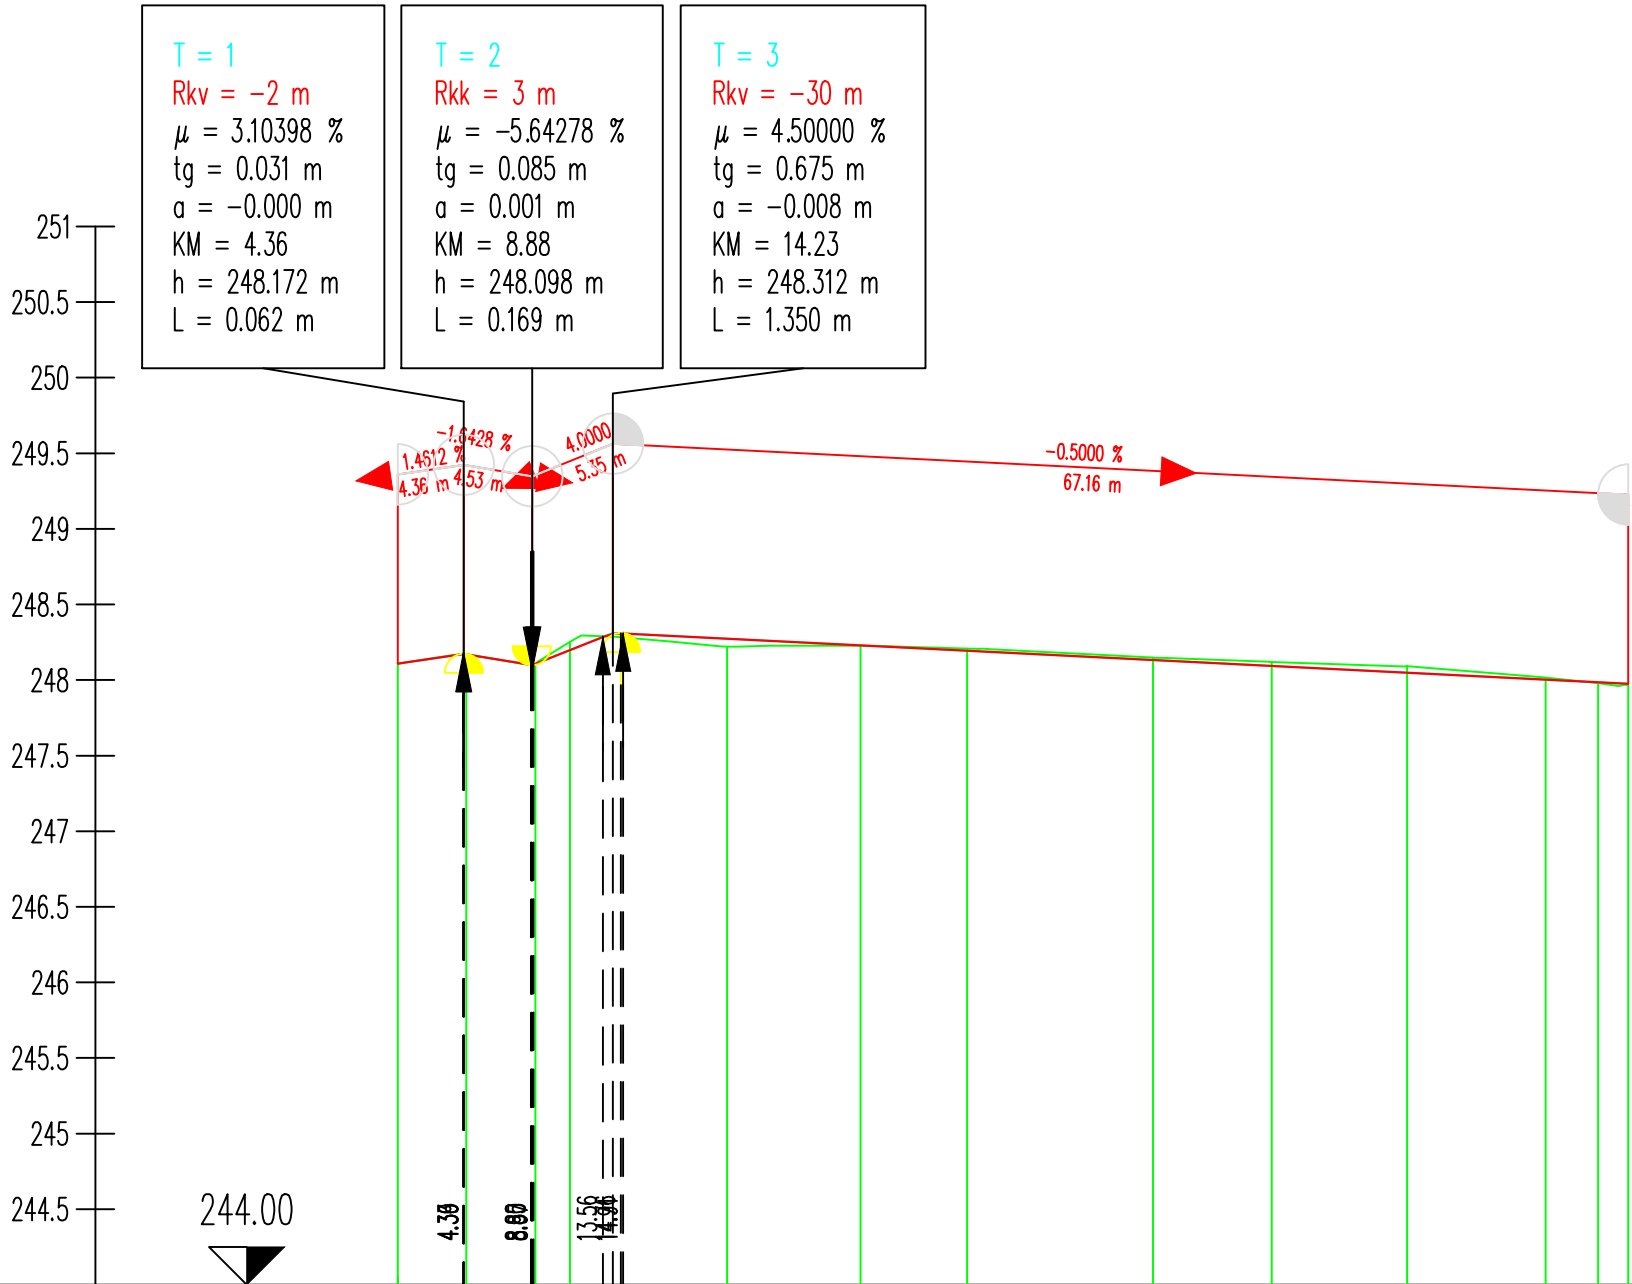


ОЗНАКИ НА ПРОФИЛОТ	1 4.536 2 4.576 2.279 10.394 5 8.824 6 7.048 7 12.302 8 7.846 9 8.950 10 9.170 13.467.999
СТАЦИОНАЖИ	0.00 4.53 9.11 11.39 21.78 30.60 37.65 49.96 57.80 66.75 75.92 79.39 81.39
КОТИ НА ТЕРЕНОТ	248.102 248.169 248.106 248.252 248.222 248.228 248.209 248.148 248.119 248.091 248.016 247.979 247.965
КОТИ НА ЛЕВИТЕ ИВИЦИ	Л_ЛЕНТА 248.109 248.179 248.119 248.233 248.324 248.280 248.245 248.183 248.144 248.099 248.024 247.972 247.962
КОТИ НА НИВЕЛЕТАТА	248.109 248.169 248.107 248.198 248.274 248.230 248.195 248.133 248.094 248.049 248.003 247.986 247.976
КОТИ НА ДЕСНИТЕ ИВИЦИ	Д_ЛЕНТА 248.099 248.162 248.095 248.163 248.224 248.180 248.145 248.083 248.044 247.999 247.983 248.000 247.990
ПРАВЦИ И КРИВИНИ	Десно Лево -- Кривина Правец d=81.39
ПОПРЕЧНИ НАКЛОНИ	Лев роб Десен роб Л роб Д роб 0.00 4.54 4.58 9.11 12.94 72.99 79.39 0.00% 0.00% 0.00% 0.00% 0.00% 0.00% 0.00% -0.46% -0.39% -0.38% -2.50% 2.50% 1.0000% 0.7000% 4.54 4.58 3.78 6.40
ШИРИНИ НА ПАТОТ	Л_ЛЕНТА Д_ЛЕНТА 2.00 2.00 2.00 2.00 2.00 2.00 2.00 2.00 2.00 2.00 2.00 2.00 2.00
ПОПРЕЧНИ НАКЛОНИ	0.02% 0.51% 0.58% 2.50% 2.50% 1.0000% 0.7000% -0.46% -0.39% -0.38% -2.50% -2.50% 1.0000% 0.7000%


РЕВИЗИЈА / РЕВИДЕНТ:	ДАТУМ:	ПОТПИС НА РЕВИДЕНТ:	ПЕЧАТ НА РЕВИДЕНТ:
ГРАДЕЖЕН ИНСТИТУТ "МАКЕДОНИЈА" А.Д. Ул. "Дрезденска" бр.52, 1000 Скопје, Република Македонија ИБСБ: ИБНБ.ГИМ.ЦОМ.МК			
ИНВЕСТИТОР: ОПШТИНА ЦЕНТАР	ОБЈЕКТ: ОСНОВЕН ПРОЕКТ ЗА РЕКОНСТРУКЦИЈА (РЕХАБИЛИТАЦИЈА) НА ПОСТЕОЧКА УЛИЧНА МРЕЖА ЗА УЛИЦИ „ДОНБАС“, „АНДОН ДУКОВ“, „АЛБЕРТ АЈНШТАЈН“, ОПШТИНА ЦЕНТАР - СКОПЈЕ	ПЕЧАТ НА ОДГОВОРЕН ПРОЕКТАНТ:	
ПРОЕКТ: ОСНОВЕН ПРОЕКТ	ОДГОВОРЕН ПРОЕКТАНТ: м-р Драганчо Волчески дипл.град.инж	ПОТПИС НА ОДГОВОРЕН ПРОЕКТАНТ: <i>[Signature]</i>	
ФАЗА НА ПРОЕКТИРАЊЕ: ПАТИШТА	ПРОЕКТАНТИ: м-р Драганчо Волчески дипл.град.инж	ПОТПИС: <i>[Signature]</i>	
СОДРЖИНА НА ЛИСТ: НАДОЛЖЕН ПРОФИЛ УЛ.ДОНБАС		СОРАБОТНИЦИ: м-р Ивана Недевска , дипл.град.инж. Бејан Моукоч , дипл.град.инж. м-р Андреј Матевски , дипл.град.инж. Александра Делова, дипл.град.инж	
ТЕХНИЧКИ БРОЈ НА ПРОЕКТОТ: ИНГ: 006 - 02 - 19		ДАТУМ: ФЕВРУАРИ 2019	РАЗМЕР: М = 1 : 500/50
		ФОРМАТ: 420/580	БРОЈ НА ЛИСТ: 04-03

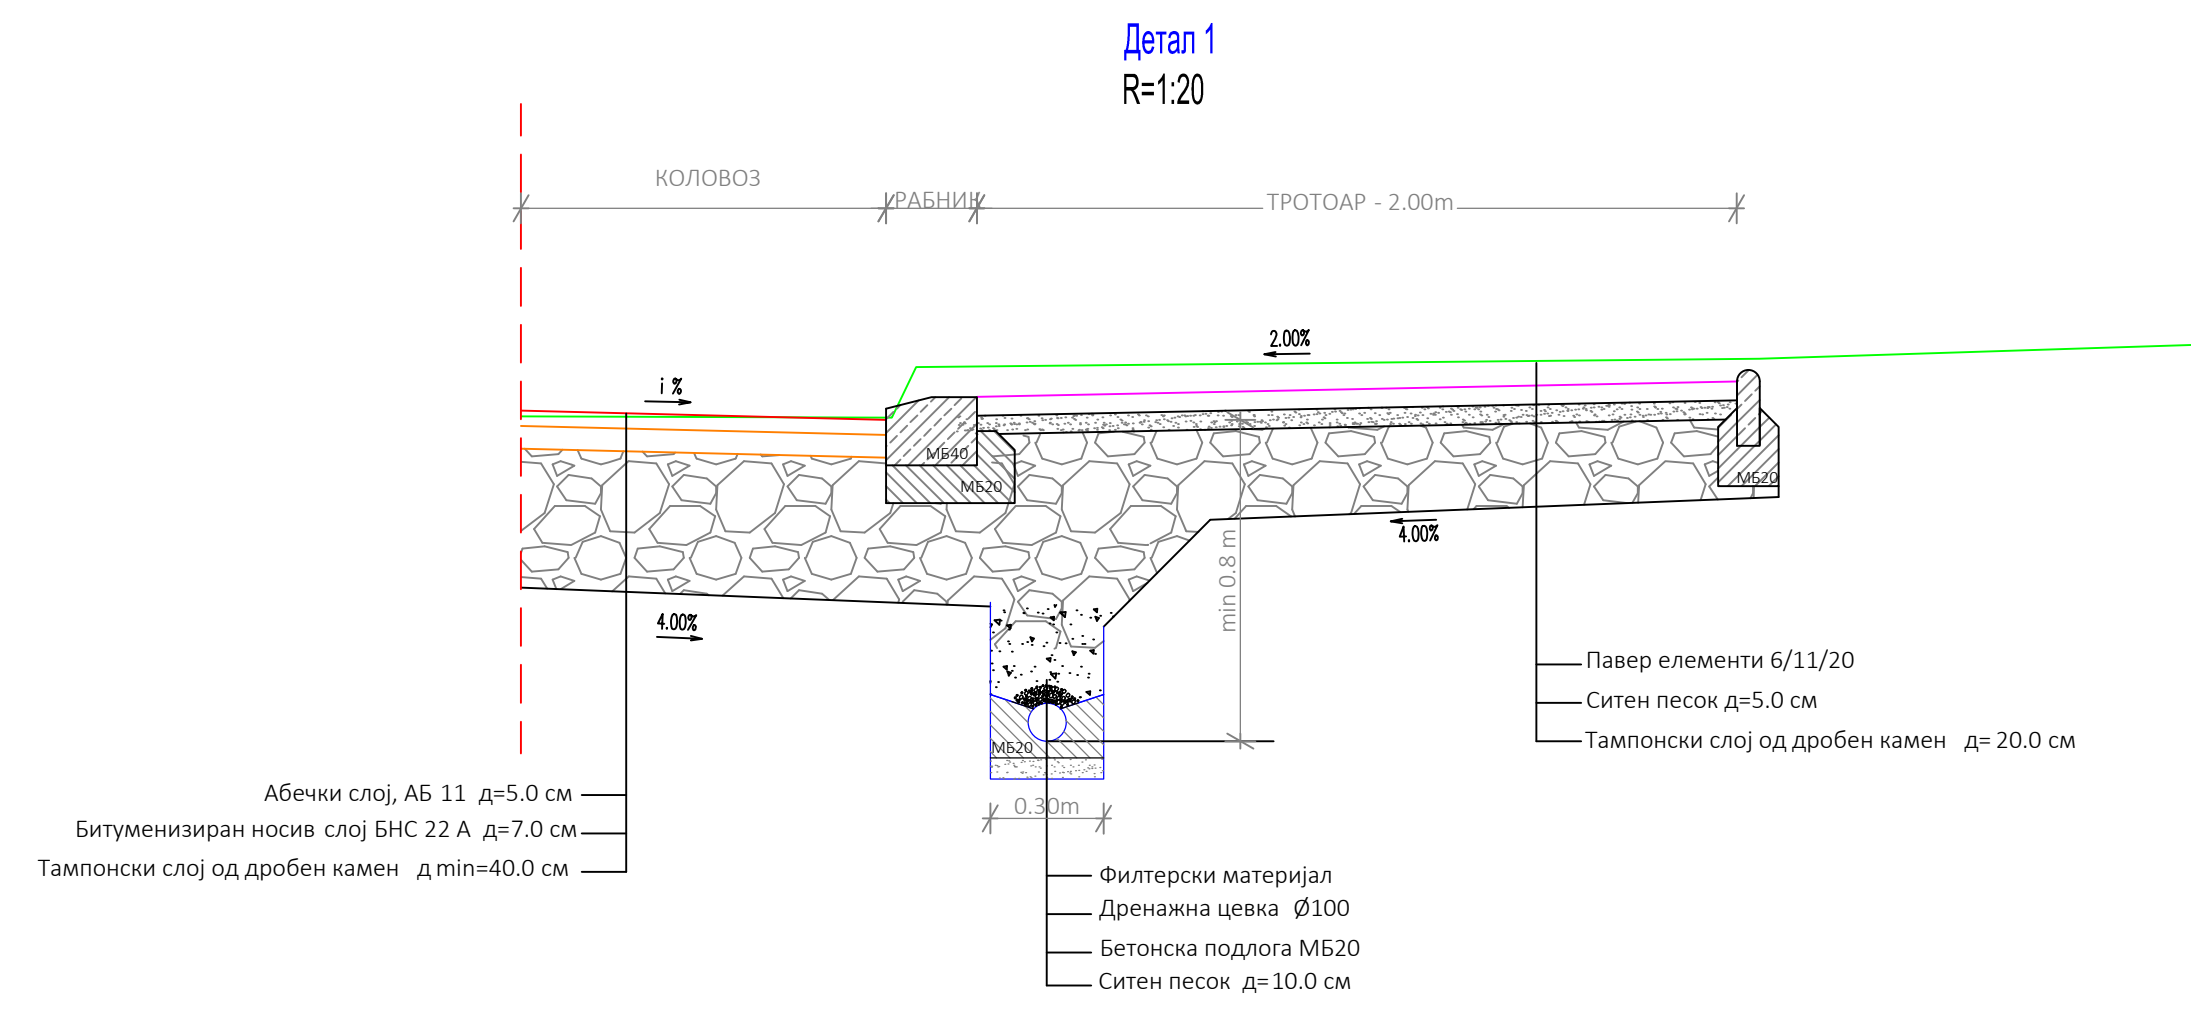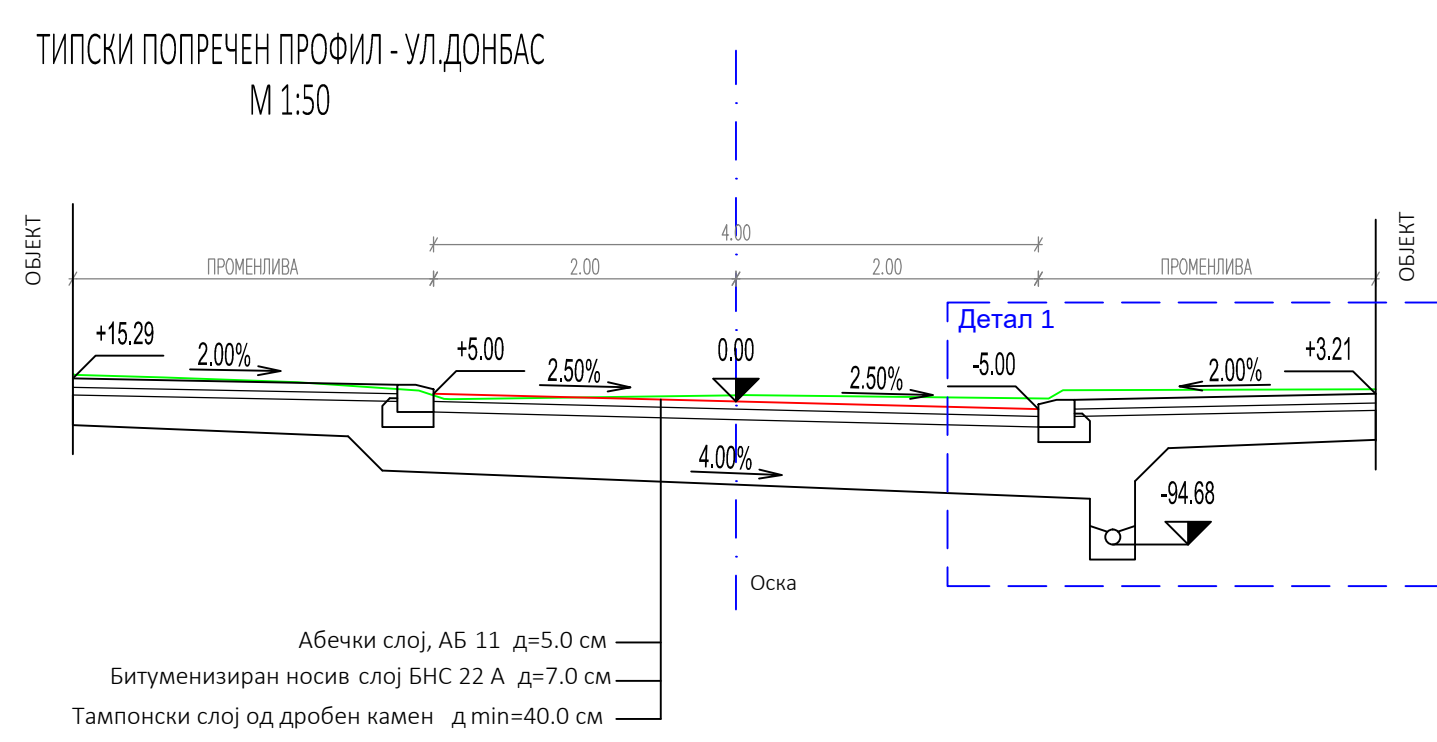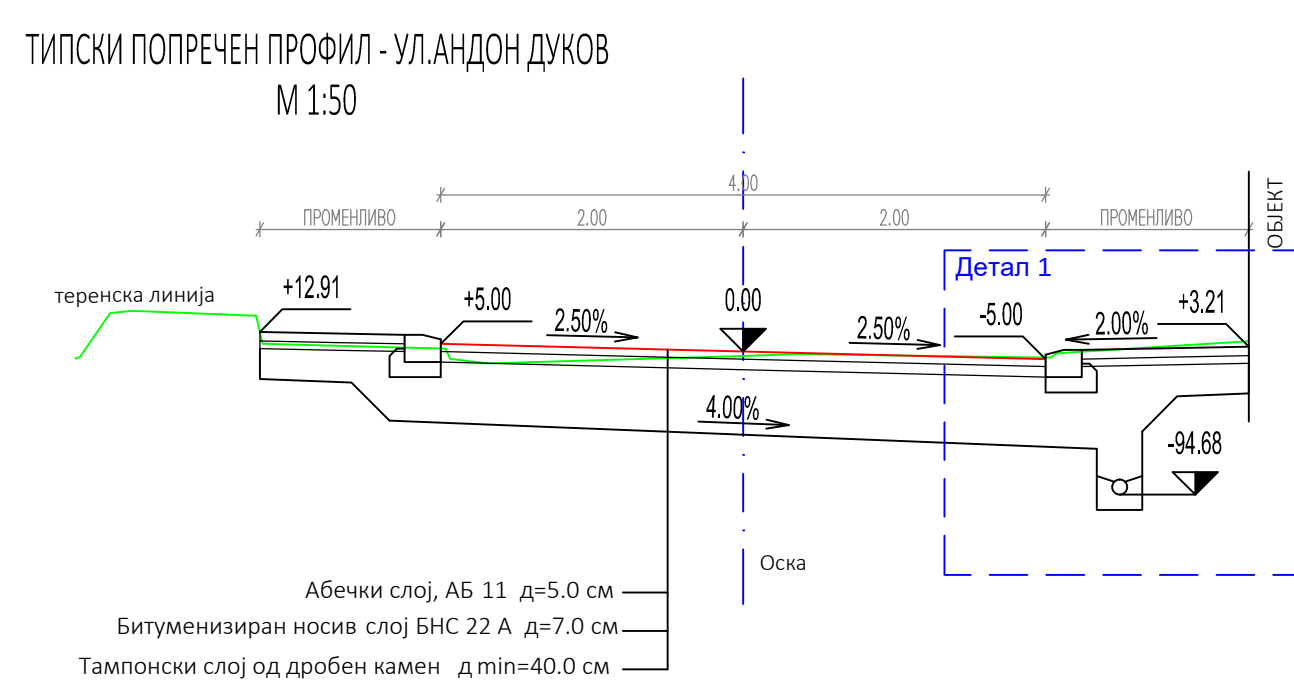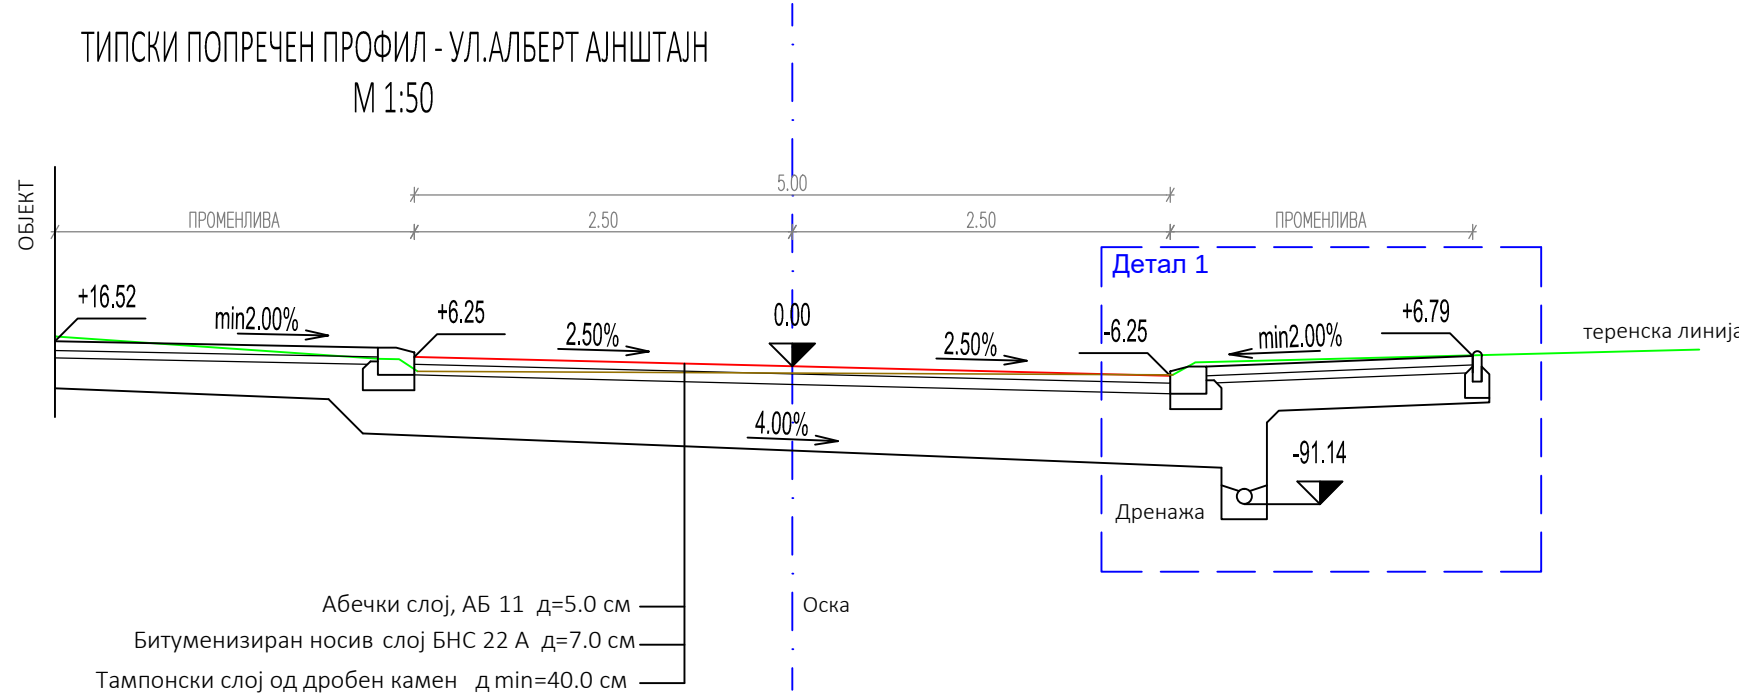


БЕТОНСКИ РАБНИК 18/24 МВ-40
М = 1:10 (sm)

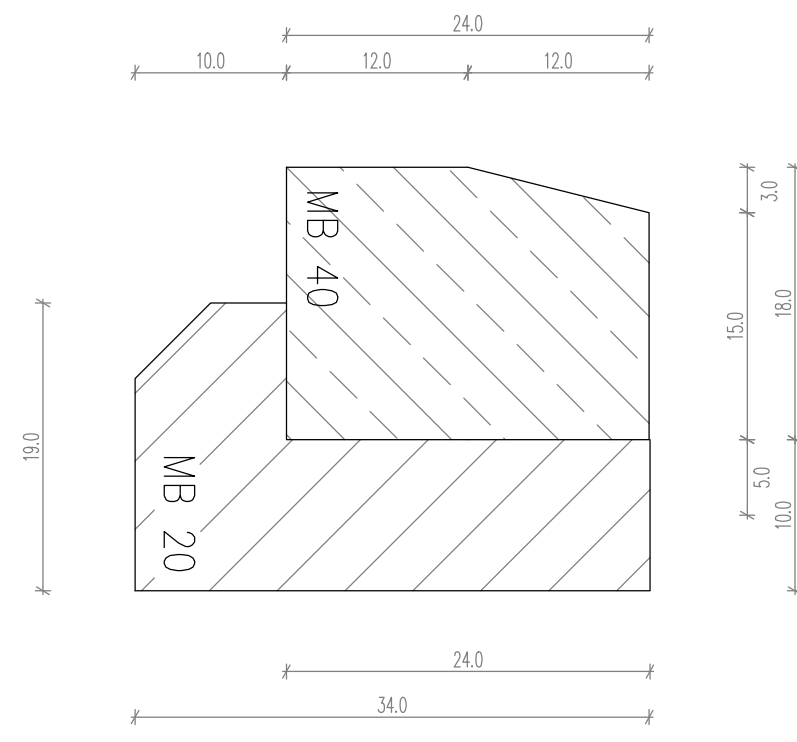






РАБНИК ТИП ПАВЕР 6/20/100
М = 1:10 (sm)

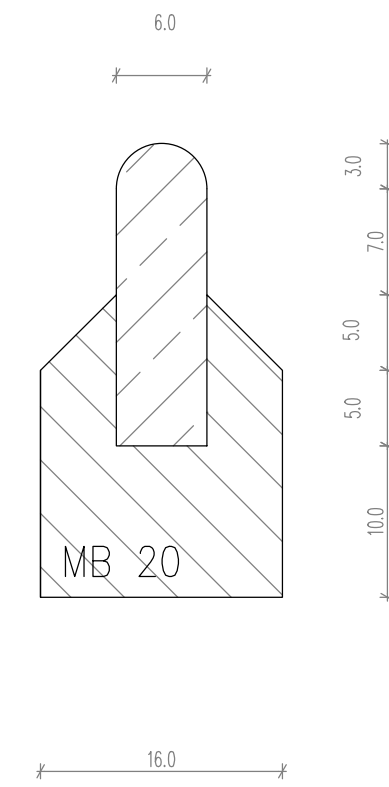



РЕВИЗИЈА / РЕВИДЕНТ:	ДАТУМ:	ПОТПИС НА РЕВИДЕНТ:	ПЕЧАТ НА РЕВИДЕНТ:
Г ГРАДЕЖЕН ИНСТИТУТ "МАКЕДОНИЈА" А.Д. Ул. "Дрезденска" бр.52, 1000 Скопје, Република Македонија УСБ: ЫНБ, ГИМ, ЦОМ, МК			
ИНВЕСТИТОР: ОПШТИНА ЦЕНТАР	ОБЈЕКТ: ОСНОВЕН ПРОЕКТ ЗА РЕКОНСТРУКЦИЈА (РЕХАБИЛИТАЦИЈА) НА ПОСТЕОЧКА УЛИЧНА МРЕЖА ЗА УЛИЦИ „ДОНБАС“, „АНДОН ДУКОВ“, „АЛБЕРТ АЈНШТАЈН“, ОПШТИНА ЦЕНТАР - СКОПЈЕ	ПЕЧАТ НА ОДГОВОРЕН ПРОЕКТАНТ:	
ПРОЕКТ: ОСНОВЕН ПРОЕКТ	ОДГОВОРЕН ПРОЕКТАНТ: м-р Драганчо Волчески дипл.град.инж	ПОТПИС НА ОДГОВОРЕН ПРОЕКТАНТ: 	
ФАЗА НА ПРОЕКТИРАЊЕ: ПАТИШТА	ПРОЕКТАНТИ: м-р Драганчо Волчески дипл.град.инж	ПОТПИС: 	
СОДРЖИНА НА ЛИСТ: ТИПСКИ ПОПРЕЧНИ ПРОФИЛИ СО КОНСТРУКТИВНИ ДЕТАЛИ	СОРАБОТНИЦИ: м-р Ивона Недевска , дипл.град.инж. Бејан Моукоч, дипл.град.инж. м-р Андреј Матовски , дипл.град.инж. Александра Делова, дипл.град.инж	ПОТПИС:	
ТЕХНИЧКИ БРОЈ НА ПРОЕКТОТ: ИНГ: 006 - 02 - 19	ДАТУМ: ФЕВРУАРИ 2019	РАЗМЕР: М = 1 : 50, 20, 10	ФОРМАТ: 297/950
		БРОЈ НА ЛИСТ:	05

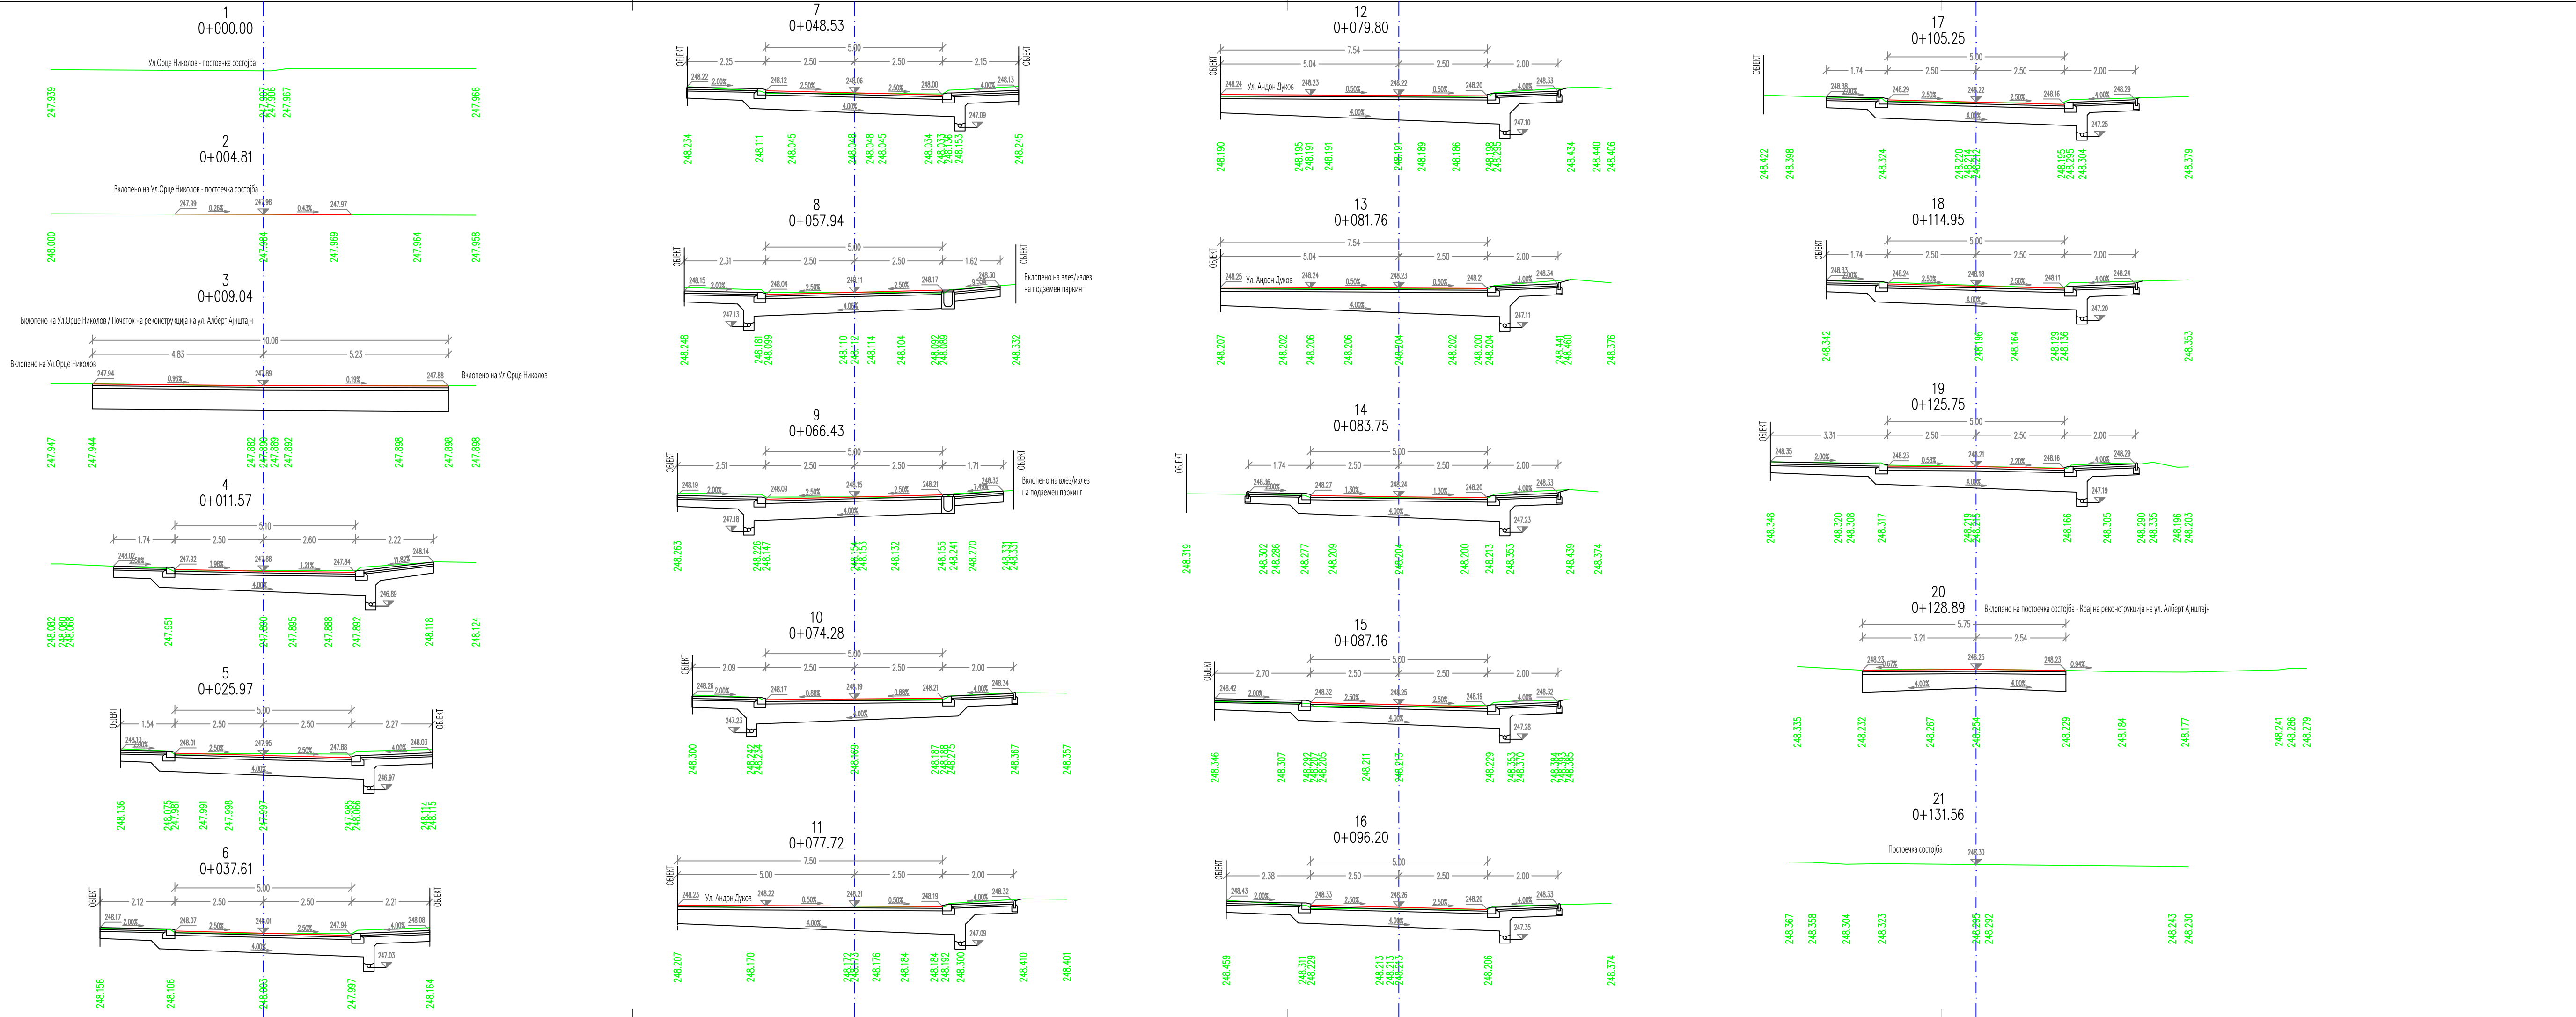

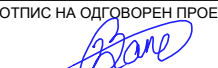РЕВИЗИЈА / РЕВИДЕНТ:	ДАТУМ:	ПОТПИС НА РЕВИДЕНТ:	ПЕЧАТ НА РЕВИДЕНТ:
ГРАДЕЖЕН ИНСТИТУТ "МАКЕДОНИЈА" А.Д. Ул. "Дрезденска" бр.52, 1000 Скопје, Република Македонија ЅСБ: ЫНБ, ГИМ, ЦОМ, МК			
ИНВЕСТИТОР: ОПШТИНА ЦЕНТАР	ОБЈЕКТ: ОСНОВЕН ПРОЕКТ ЗА РЕКОНСТРУКЦИЈА (РЕХАБИЛИТАЦИЈА) НА ПОСТОЕЧКА УЛИЧНА МРЕЖА ЗА УЛИЦИ „ДОНБАС“, „АНДОН ДУКОВ“, „АЛБЕРТ АЈНШТАЈН“, ОПШТИНА ЦЕНТАР - СКОПЈЕ	ПЕЧАТ НА ОДГОВОРЕН ПРОЕКТАНТ:	
ПРОЕКТ: ОСНОВЕН ПРОЕКТ	ОДГОВОРЕН ПРОЕКТАНТ: м-р Драганчо Волчески дипл.град.инж	ПОТПИС НА ОДГОВОРЕН ПРОЕКТАНТ: 	
ФАЗА НА ПРОЕКТИРАЊЕ: ПАТИШТА	ПРОЕКТАНТИ: м-р Драганчо Волчески дипл.град.инж	ПОТПИС: 	
СОДРЖИНА НА ЛИСТ: КАРАКТЕРИСТИЧНИ ПОПРЕЧНИ ПРОФИЛИ УЛ.АЛБЕРТ АЈНШТАЈН	СОРАБОТНИЦИ: м-р Ивона Недевска , дипл.град.инж. Бејан Моукоч, дипл.град.инж. м-р Андреј Матовски , дипл.град.инж. Александра Делова, дипл.град.инж	ПОТПИС:	
ТЕХНИЧКИ БРОЈ НА ПРОЕКТОТ: ИНГ: 006 - 02 - 19	ДАТУМ: ФЕВРУАРИ 2019	РАЗМЕР: М = 1 : 100	ФОРМАТ: 297/950
		БРОЈ НА ЛИСТ: 06-01	

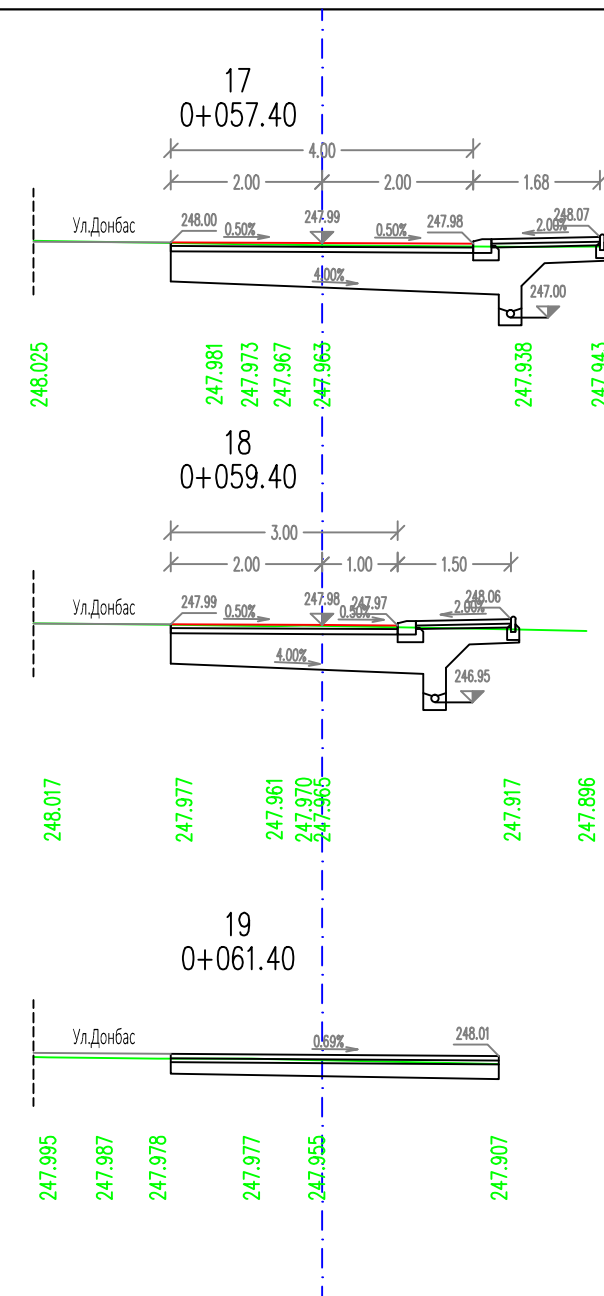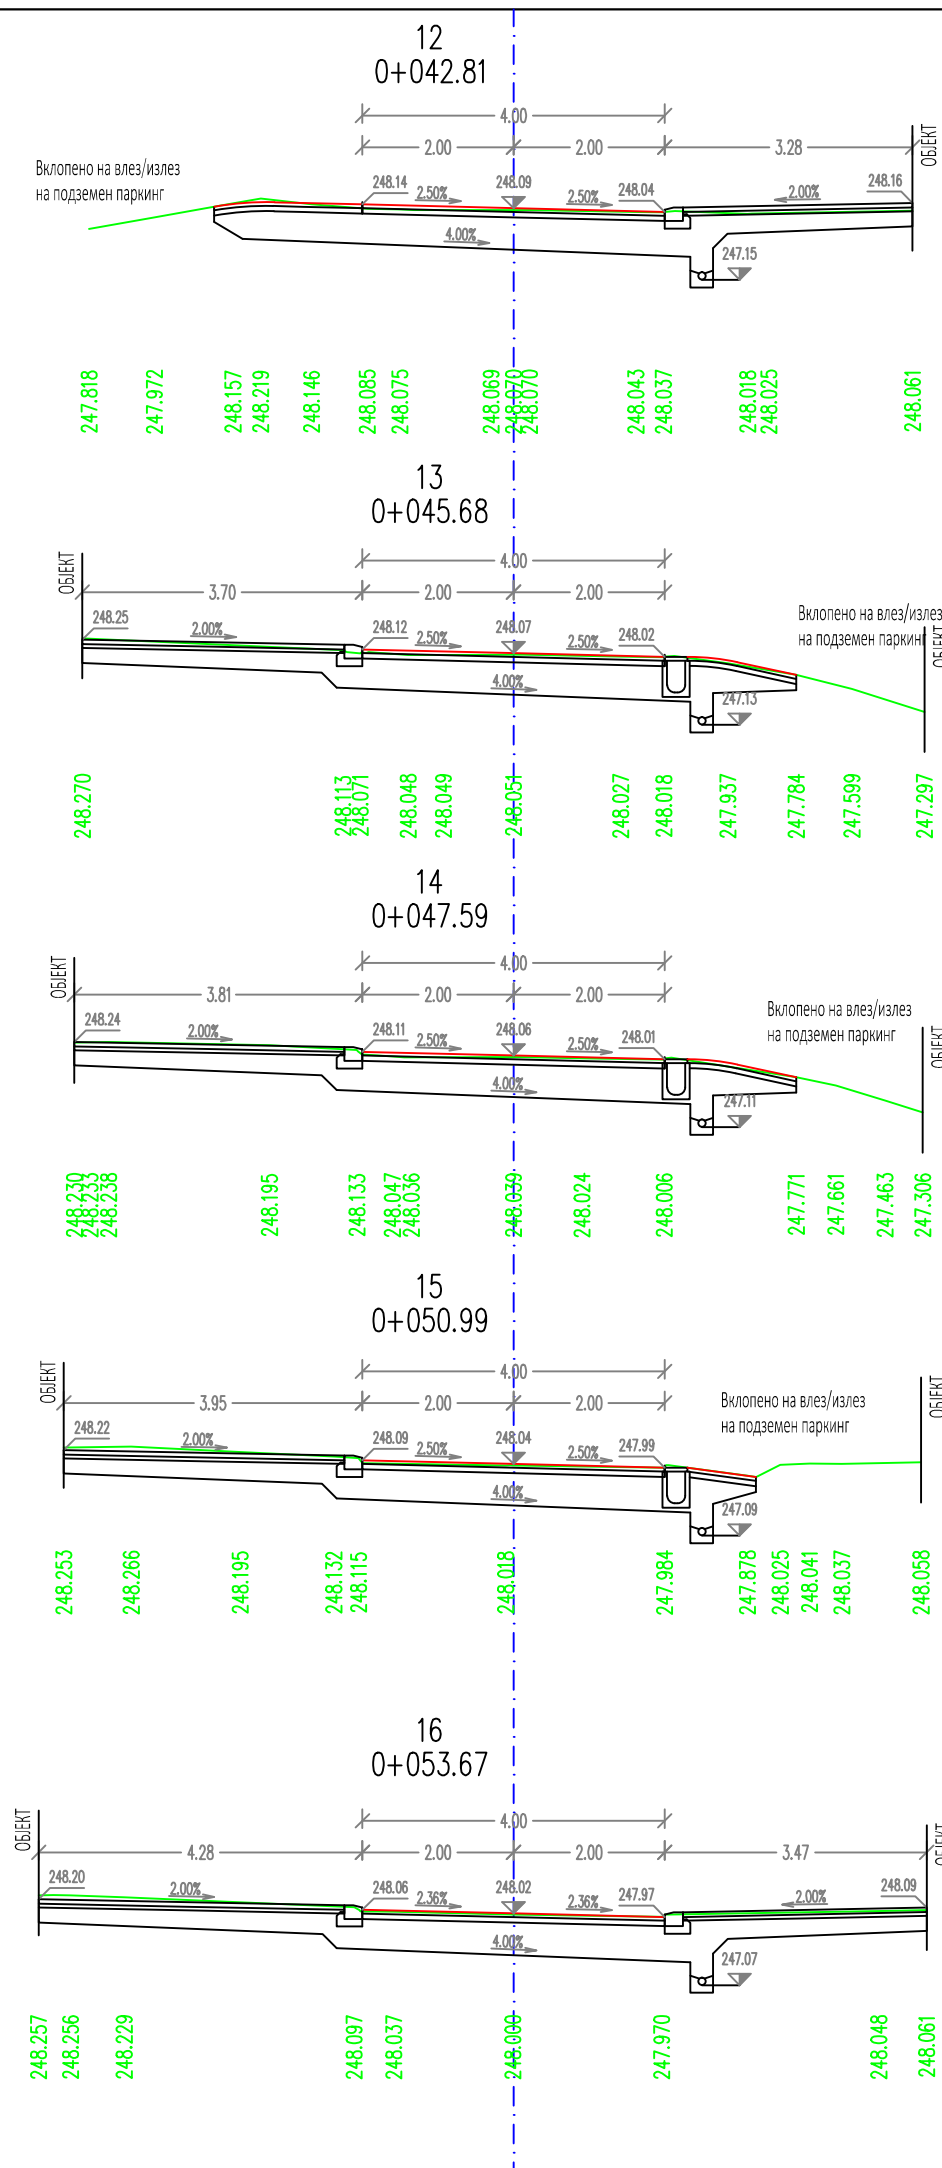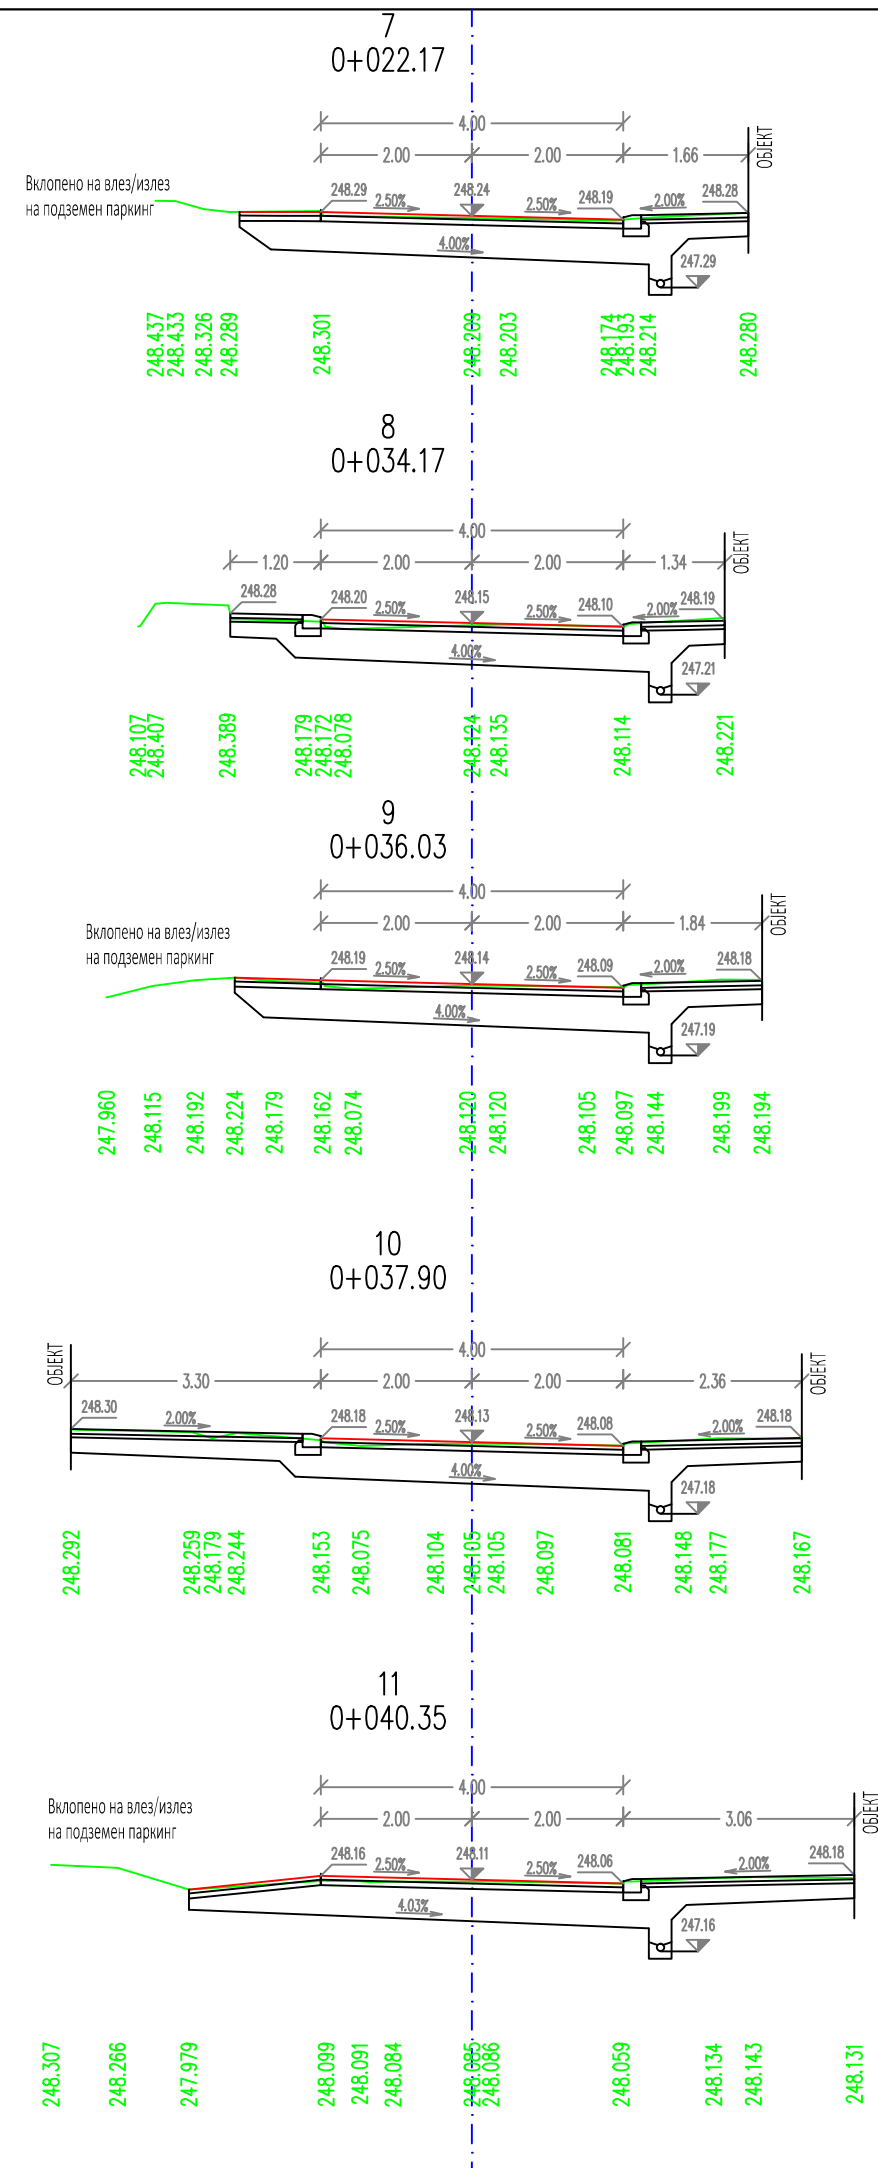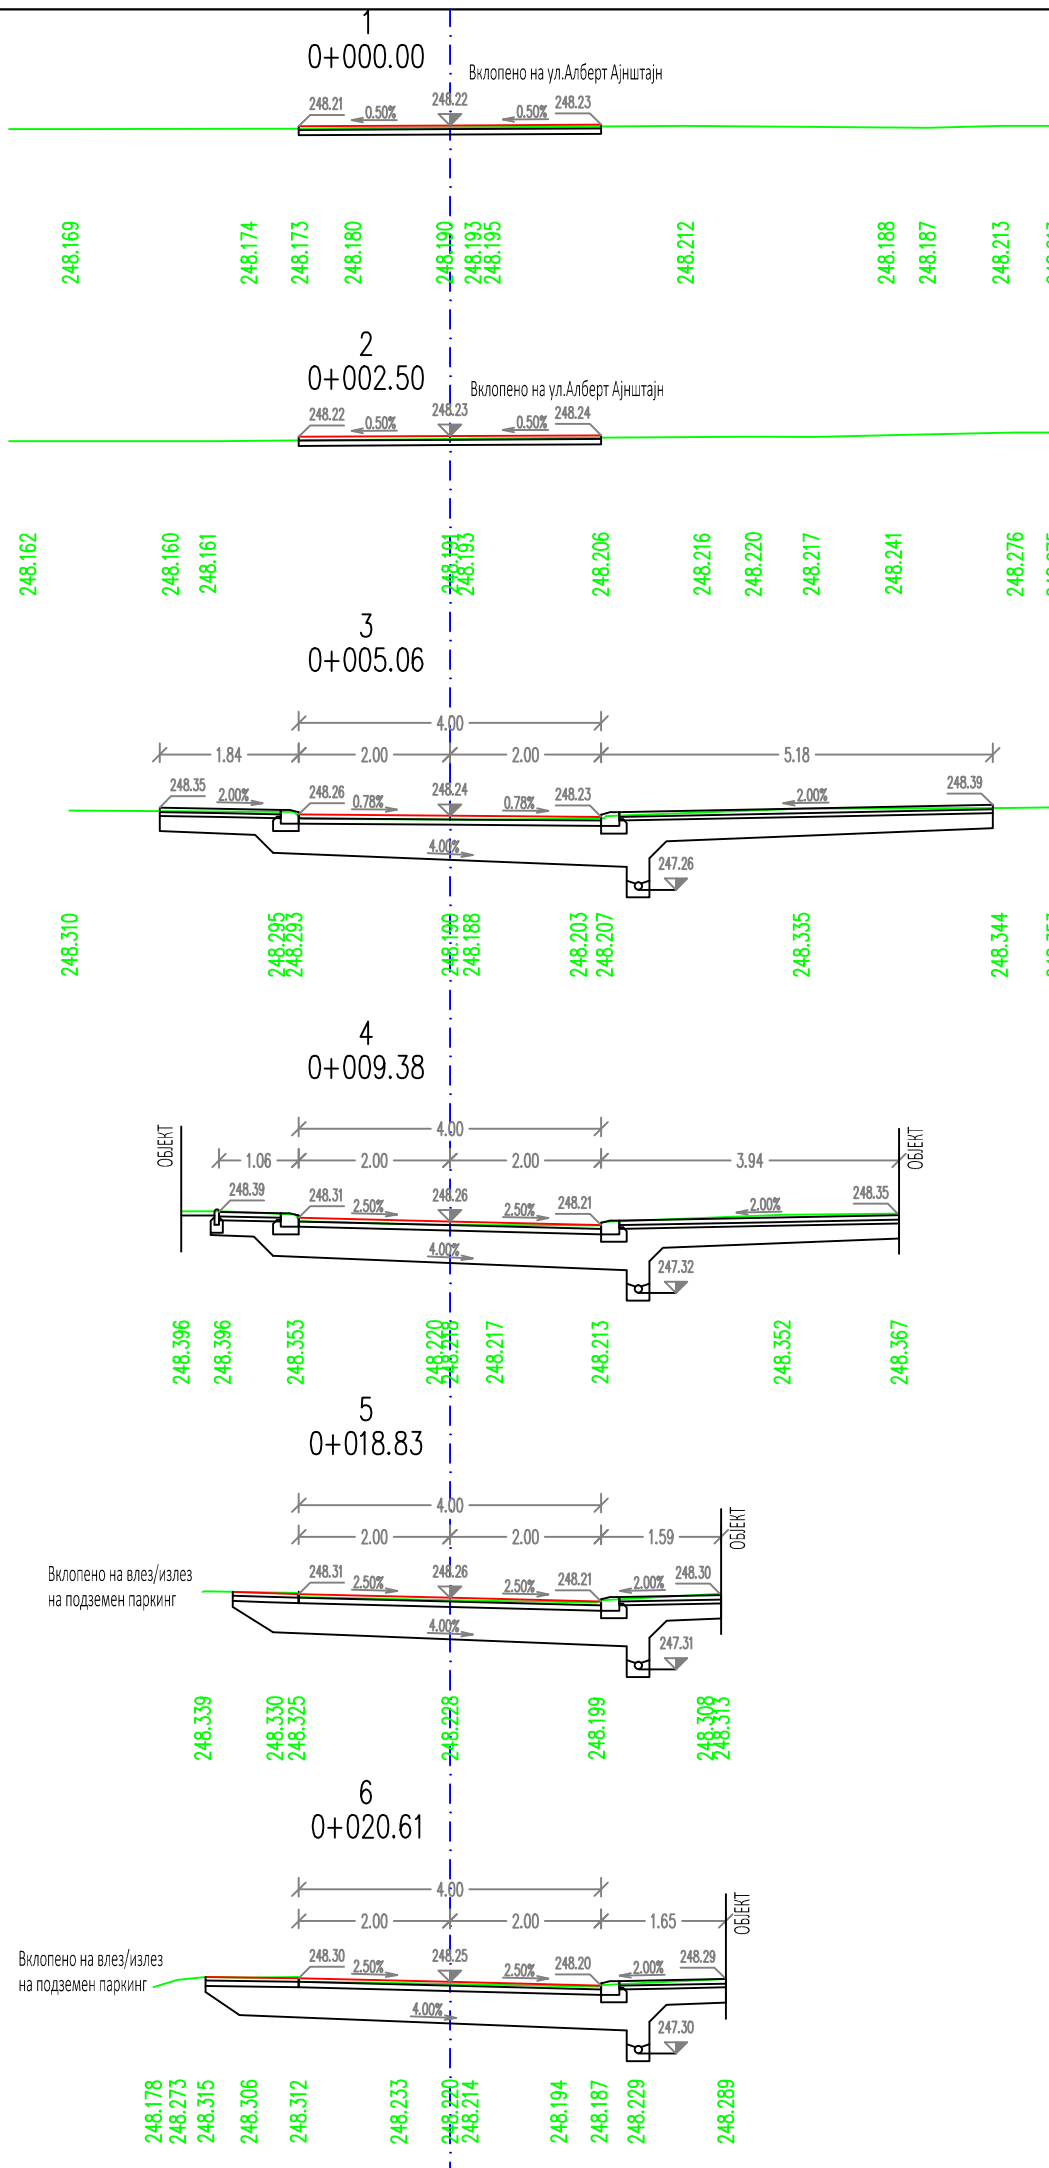

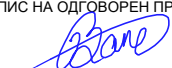РЕВИЗИЈА / РЕВИДЕНТ:	ДАТУМ:	ПОТПИС НА РЕВИДЕНТ:	ПЕЧАТ НА РЕВИДЕНТ:
ГРАДЕЖЕН ИНСТИТУТ "МАКЕДОНИЈА" А.Д. Ул. "Дрезденска" бр.52, 1000 Скопје, Република Македонија ЊСБ: ЊНБ,ГИМ,ДОМ,МК			
ИНВЕСТИТОР: ОПШТИНА ЦЕНТАР	ОБЈЕКТ: ОСНОВЕН ПРОЕКТ ЗА РЕКОНСТРУКЦИЈА (РЕХАБИЛИТАЦИЈА) НА ПОСТОЕЧКА УЛИЧНА МРЕЖА ЗА УЛИЦИ „ДОНБАС“, „АНДОН ДУКОВ“, „АЛБЕРТ АЈНШТАЈН“, ОПШТИНА ЦЕНТАР - СКОПЈЕ	ПЕЧАТ НА ОДГОВОРЕН ПРОЕКТАНТ:	
ПРОЕКТ: ОСНОВЕН ПРОЕКТ	ОДГОВОРЕН ПРОЕКТАНТ: м-р Драганчо Волчески дипл.град.инж	ПОТПИС НА ОДГОВОРЕН ПРОЕКТАНТ: 	
ФАЗА НА ПРОЕКТИРАЊЕ: ПАТИШТА	ПРОЕКТАНТИ: м-р Драганчо Волчески дипл.град.инж	ПОТПИС: 	
СОДРЖИНА НА ЛИСТ: КАРАКТЕРИСТИЧНИ ПОПРЕЧНИ ПРОФИЛИ УЛ.АНДОН ДУКОВ	СОРАБОТНИЦИ: м-р Ивона Недевска , дипл.град.инж. Бејан Моукоч, дипл.град.инж. м-р Андреј Матовски , дипл.град.инж. Александра Делова, дипл.град.инж	ПОТПИС:	
ТЕХНИЧКИ БРОЈ НА ПРОЕКТОТ: ИНГ: 006 - 02 - 19	ДАТУМ: ФЕВРУАРИ 2019	РАЗМЕР: М = 1 : 100	ФОРМАТ: 297/950
			БРОЈ НА ЛИСТ: 06-02

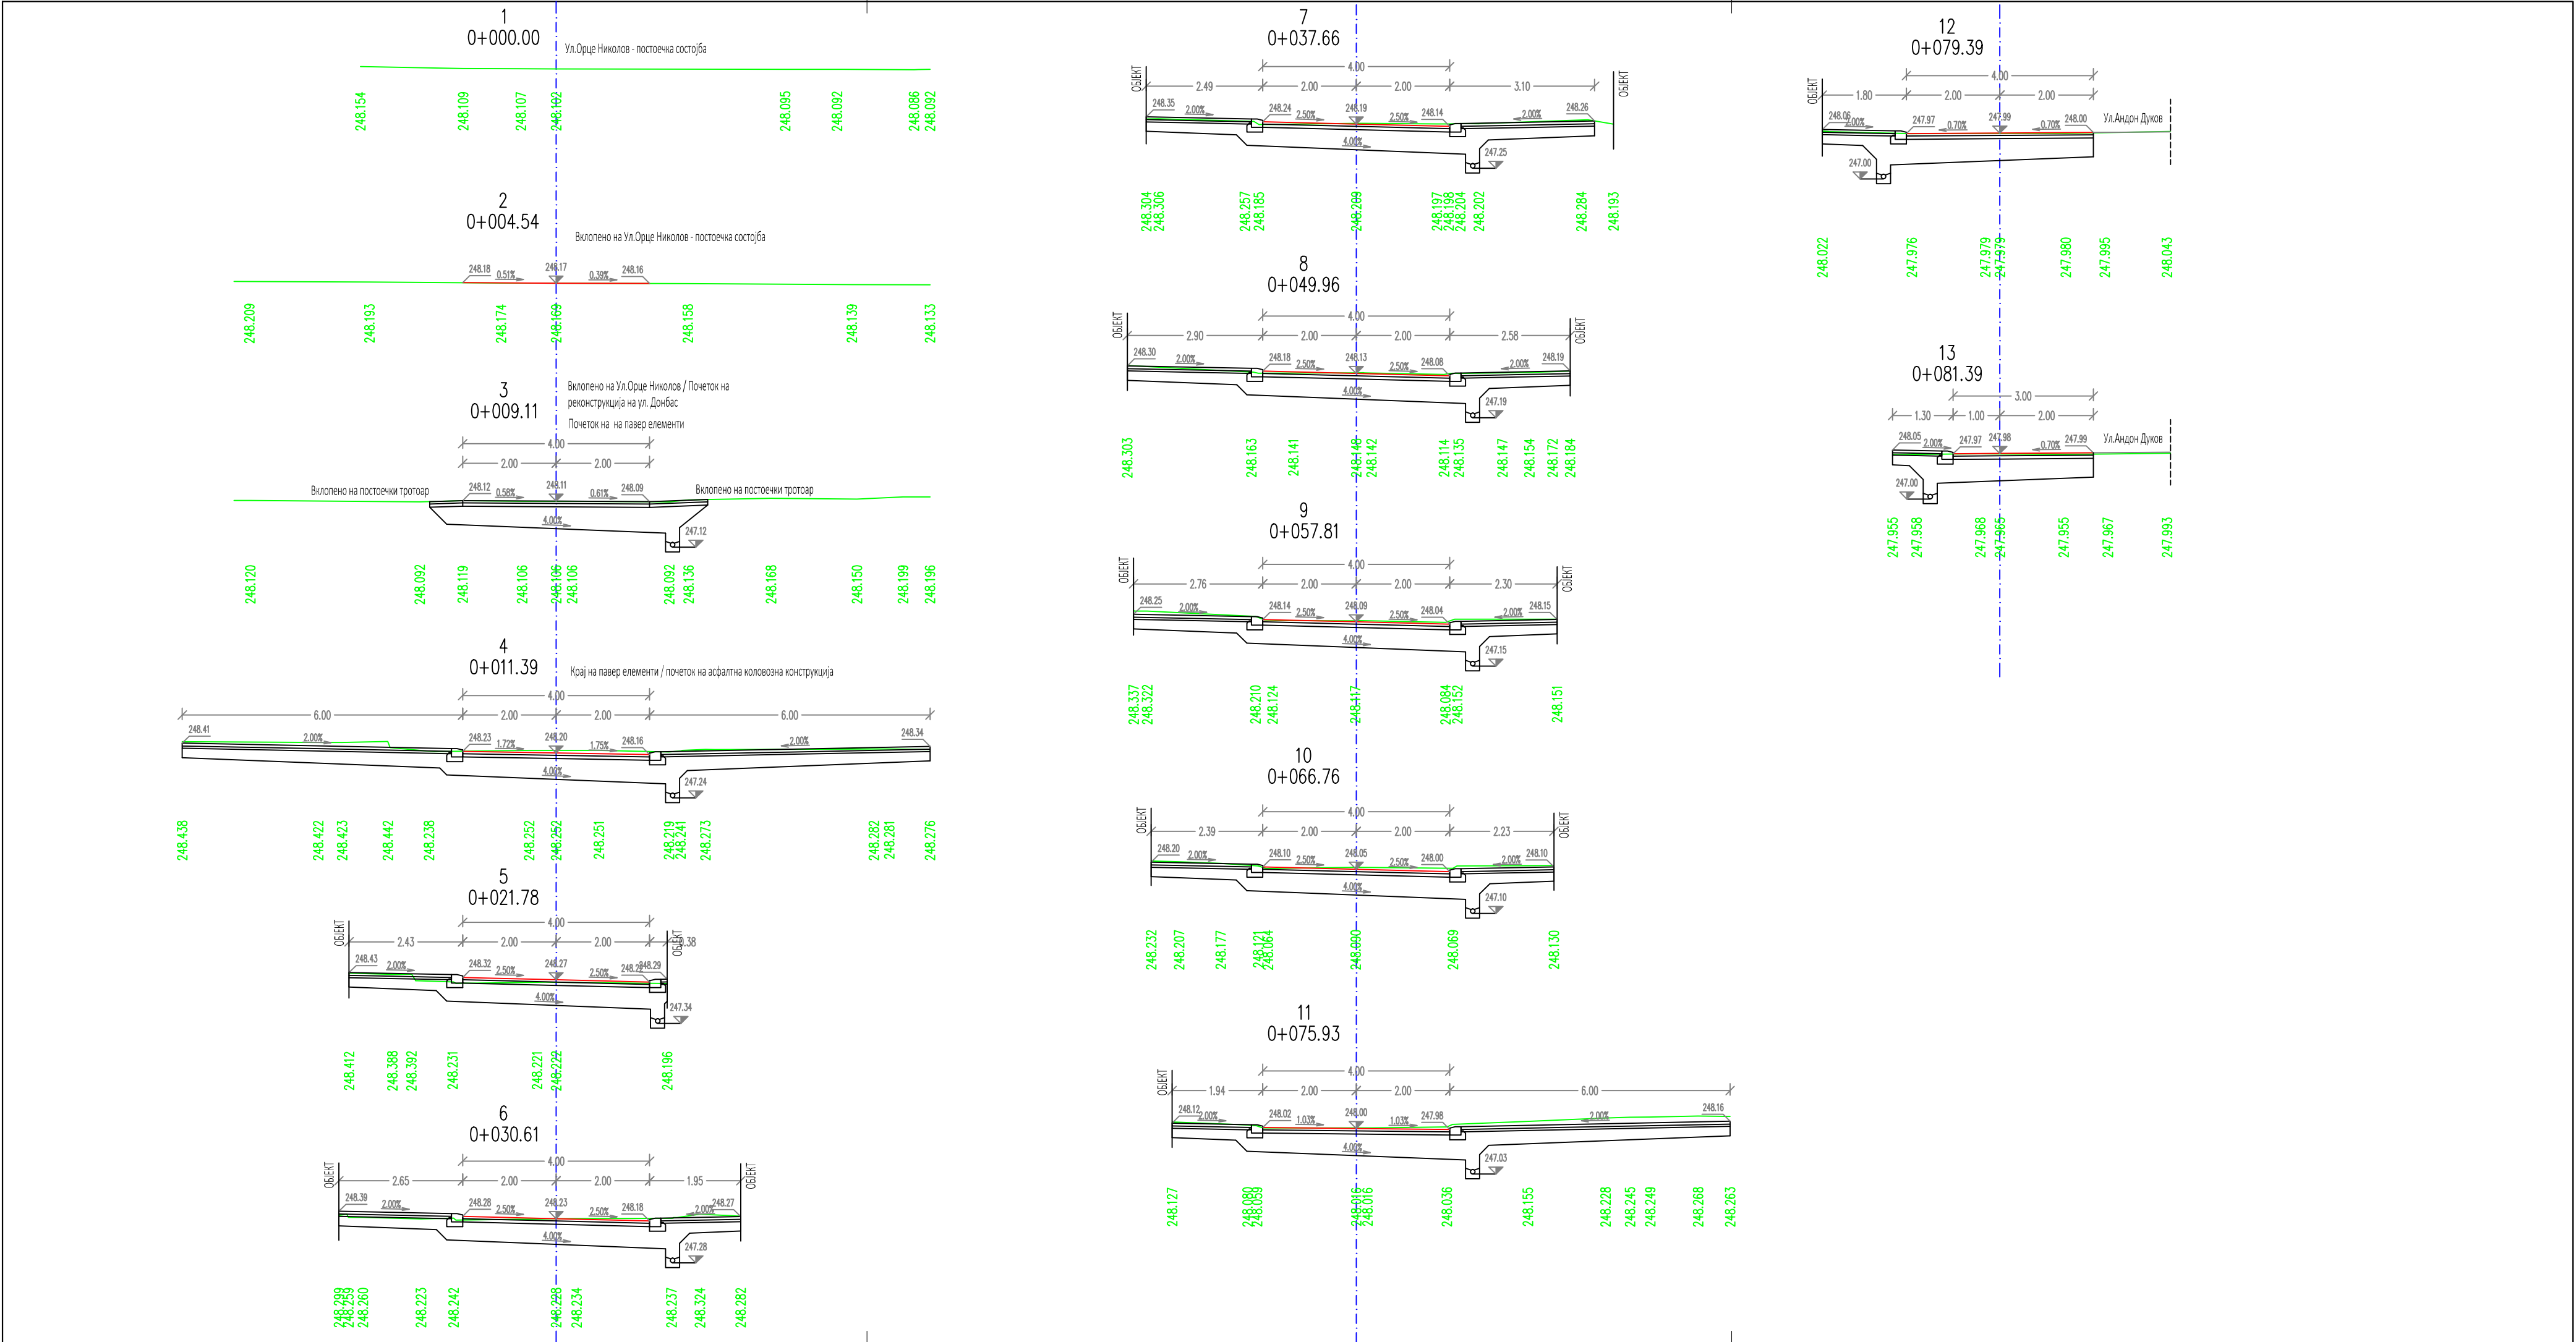

РЕВИЗИЈА / РЕВИДЕНТ:		ДАТУМ:		ПОТПИС НА РЕВИДЕНТ:		ПЕЧАТ НА РЕВИДЕНТ:		
 ГРАДЕЖЕН ИНСТИТУТ "МАКЕДОНИЈА" А.Д. Ул. "Дрезденска" бр.52, 1000 Скопје, Република Македонија ЊСБ: ЊЊЊ.ГИМ.ЦОМ.МК								
ИНВЕСТИТОР: ОПШТИНА ЦЕНТАР			ОБЈЕКТ: ОСНОВЕН ПРОЕКТ ЗА РЕКОНСТРУКЦИЈА (РЕХАБИЛИТАЦИЈА) НА ПОСТОЕЧКА УЛИЧНА МРЕЖА ЗА УЛИЦИ „ДОНБАС“, „АНДОН ДУКОВ“, „АЛБЕРТ АЈНШТАЈН“, ОПШТИНА ЦЕНТАР - СКОПЈЕ			ПЕЧАТ НА ОДГОВОРЕН ПРОЕКТАНТ:		
ПРОЕКТ: ОСНОВЕН ПРОЕКТ			ОДГОВОРЕН ПРОЕКТАНТ: м-р Драганчо Волчески дипл.град.инж			ПОТПИС НА ОДГОВОРЕН ПРОЕКТАНТ: 		
ФАЗА НА ПРОЕКТИРАЊЕ: ПАТИШТА			ПРОЕКТАНТИ: м-р Драганчо Волчески дипл.град.инж			ПОТПИС: 		
СОДРЖИНА НА ЛИСТ: КАРАКТЕРИСТИЧНИ ПОПРЕЧНИ ПРОФИЛИ УЛ.ДОНБАС			СОРАБОТНИЦИ: м-р Ивона Недевска , дипл.град.инж. Бејан Моукоч , дипл.град.инж. м-р Андреј Матевски , дипл.град.инж. Александра Делова, дипл.град.инж			ПОТПИС:		
ТЕХНИЧКИ БРОЈ НА ПРОЕКТОТ: ИНГ: 006 - 02 - 19			ДАТУМ: ФЕВРУАРИ 2019		РАЗМЕР: М = 1 : 100		ФОРМАТ: 297/765	БРОЈ НА ЛИСТ: 06-03