


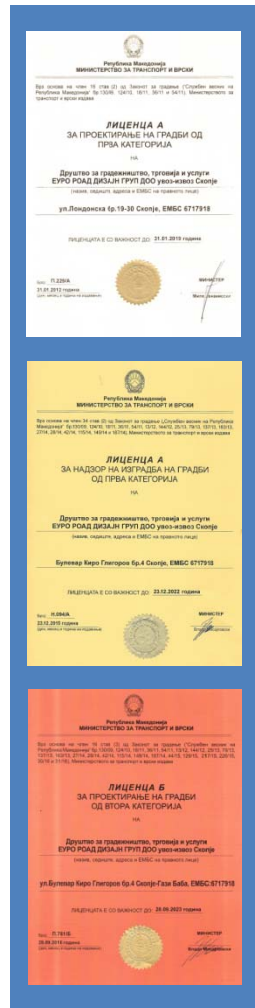


ИНВЕСТИТОР: ОПШТИНА НЕГОТИНО

ОСНОВЕН ПРОЕКТ ЗА ПОТИСЕН ЦЕВКОВОД И РЕЗЕРВОАР ЗА ВОДА ЗА ПИЕЊЕ ВО с. ТРЕМНИК, ОПШТИНА НЕГОТИНО



ПАТНА КАРТА НА
МАГИСТРАЛНИ И РЕГИОНАЛНИ ПАТИШТА

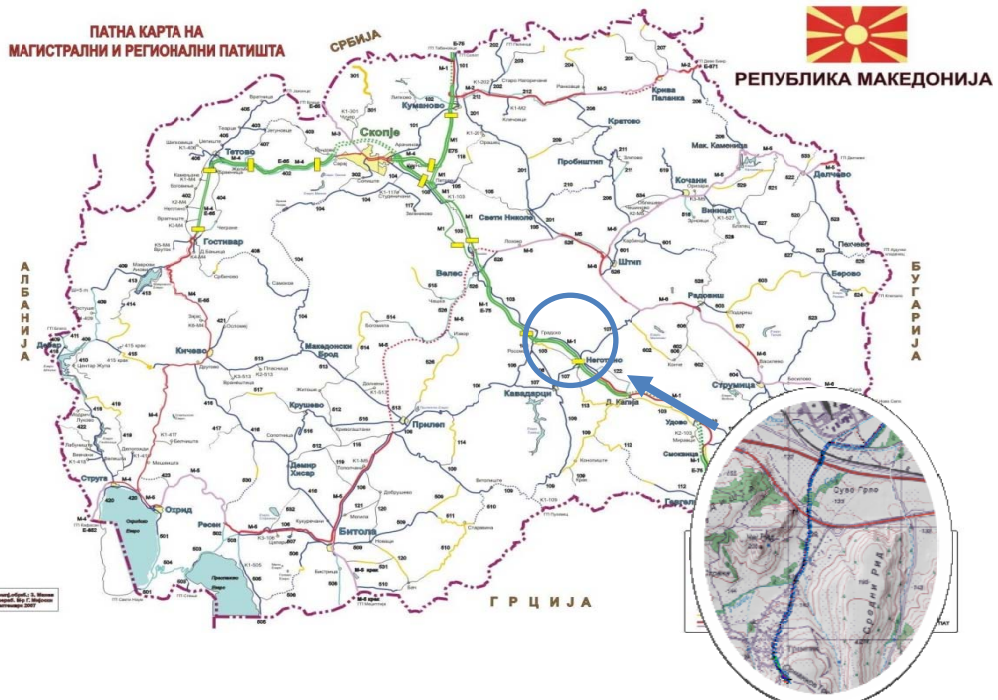

ПРОЕКТИРАЊЕ: ДГТУ ЕУРО РОАД ДИЗАЈН ГРУП доо Скопје

ИНЖЕНЕРСКА ОБЛАСТ: ВОДОВОД И КАНАЛИЗАЦИЈА “ВК”

МЕСТО НА ИЗВЕДБА: с. ТРЕМНИК, ОПШТИНА НЕГОТИНО

Тех.бр. ВК_321/2018


Скопје, Септември 2018 г





IV. ГРАФИЧКИ ДЕЛ



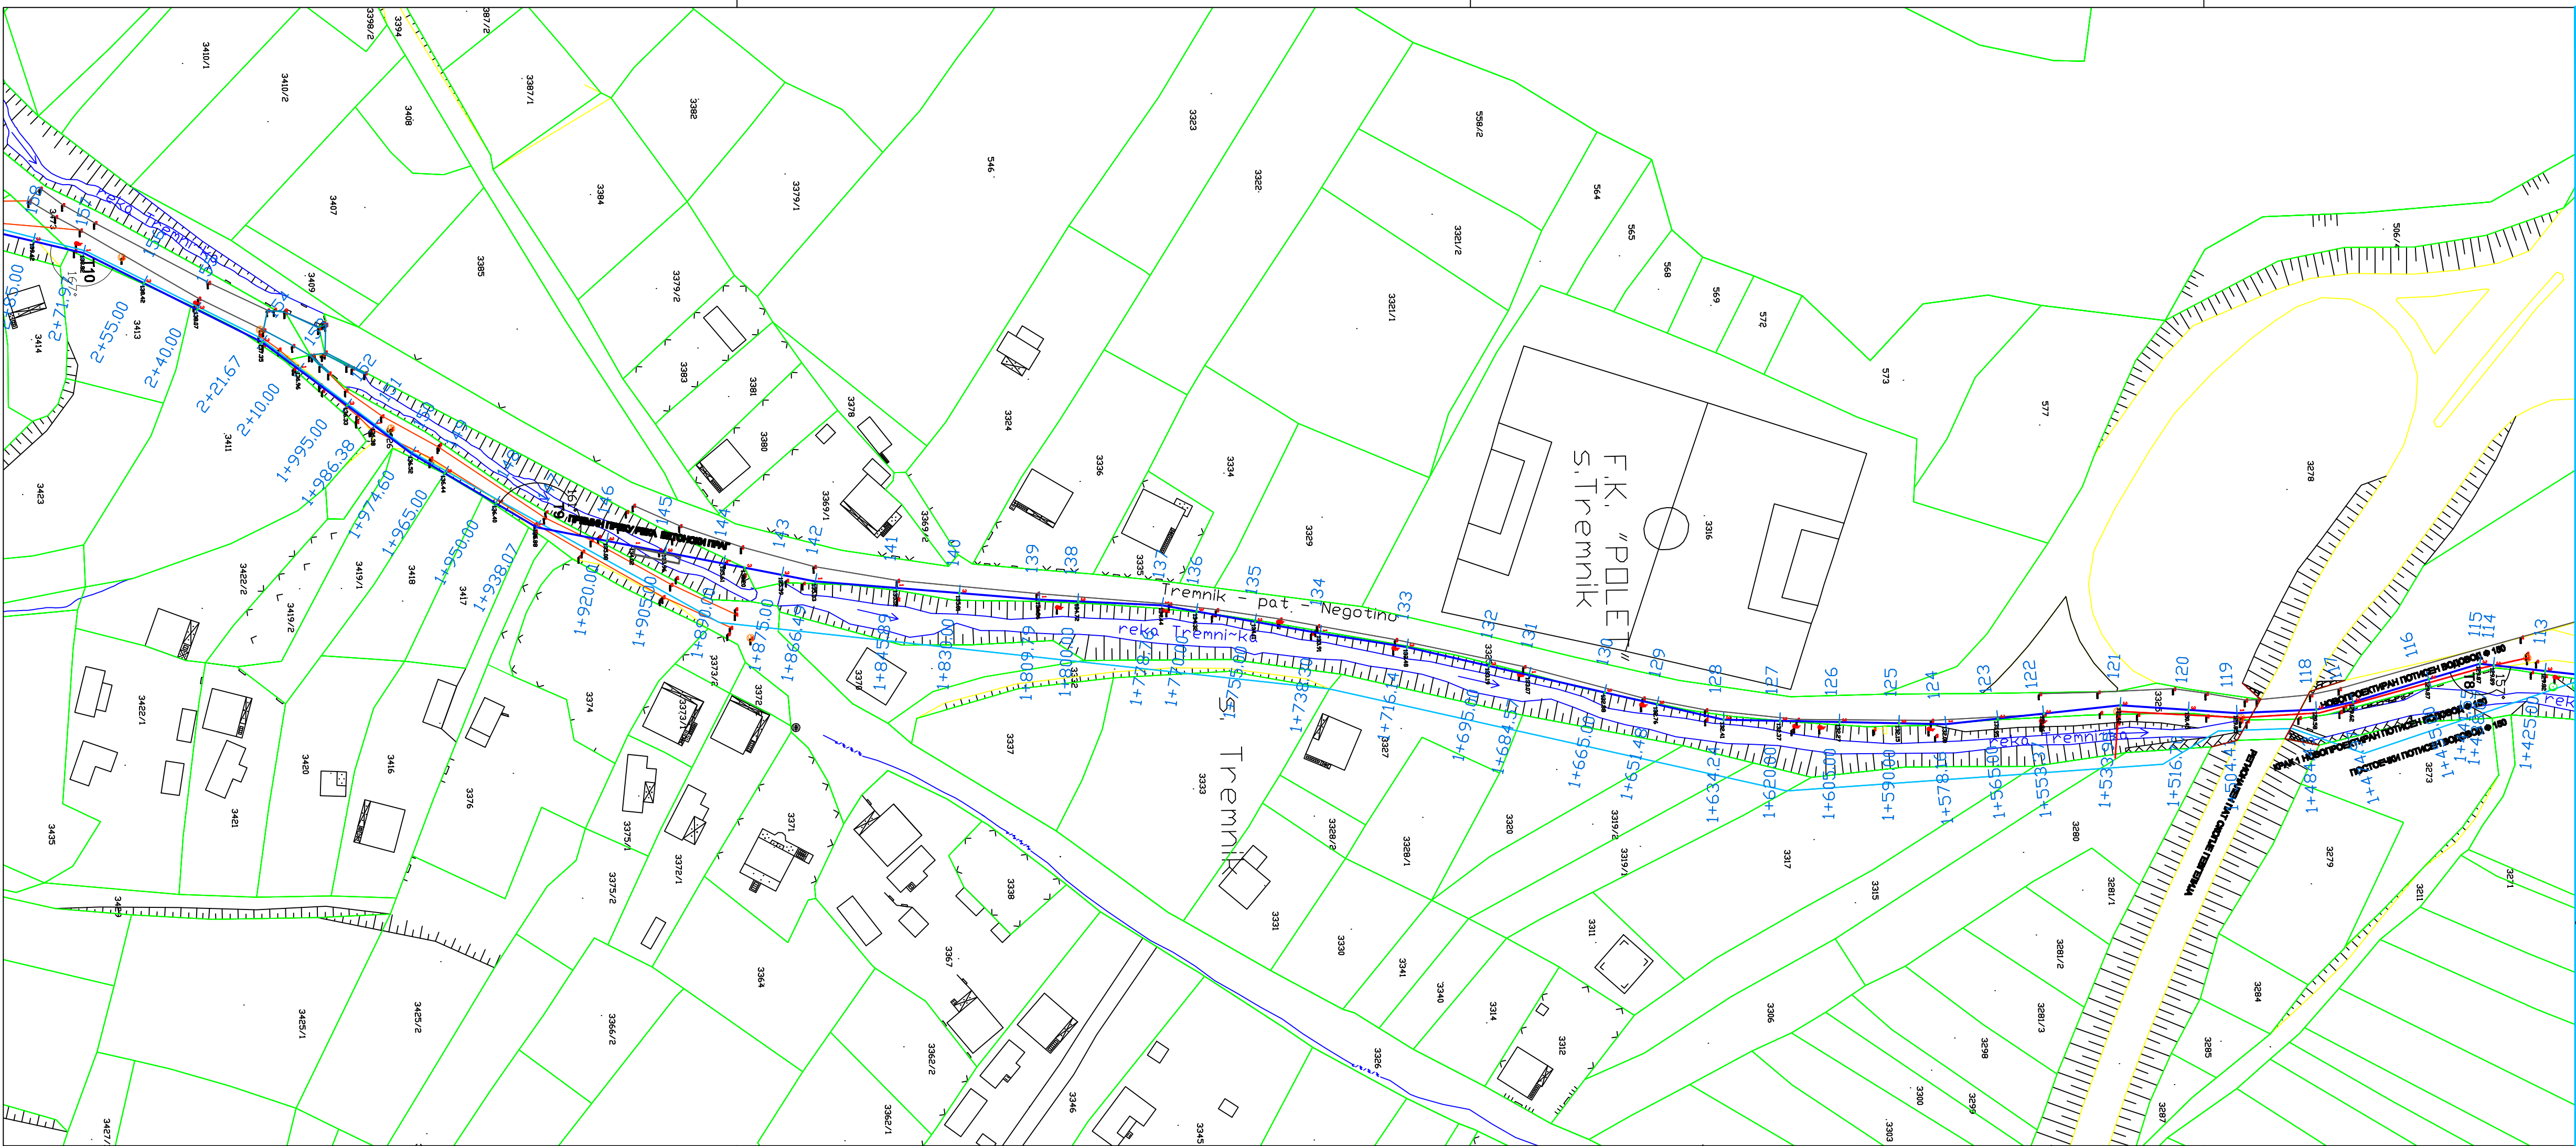

Резиме

Забелешки

Дата

М.П.

Проектант:
ЕуроРод Дизајн Груп
ДОО Скопје
www.euroroad-designgroup.com

EURO ROAD DESIGN GROUP
design, revision and consulting

Инвеститор:
Општина Неготино

Проект:
Основан проект за потисен цевковод и резервоар за вода за пиење во с. Треник Општина Неготино

Цртач:
Ситуација со хоризонтално решение (пр. 113-пр.157)

Одговорен пројектант:
Слаѓан Стојановски, дипл.град.инж.
бр.на овластување А 2.1713

Соработници:
Билјана Стојановска, дипл.град.инж.


технички број:	БК_321/2018	Број на лист:	11
Вид на проект: водовод и канализација	БК	Вкупно листови:	35
Формат: А3(297mm-786mm)		Размер:	1:1000

Датум, место:


Септември 2018, Скопје



Ревија		Забелешки	
Дата		М.П.	
Проектант: ЕуроРод Дизајн Груп 100 Скопје www.euroroad-designgroup.com			
Инвеститор: Општина Неготино			
Проект: Основан проект за потисан цевковод и резервоар за вода за пиење во с. Треник Општина Неготино			
Цртеж: Ситуација со хоризонтално решение (пр. 157-пр. 215)			
Одговорен проектант: Стефан Стојановски, дипл.град.инж. Бр.на овластување А 2.1713			
Соработници: Билјана Стојановска, дипл.град.инж.			
технички број: ВК_321/2018		Број на лист: 12	
Вид на проект: водоснаб. и канализација		Вкупно листови: 35	
Формат: А3(297mm-1000mm)		Размер: 1:1000	
Датум, место:		Септември 2018, Скопје	

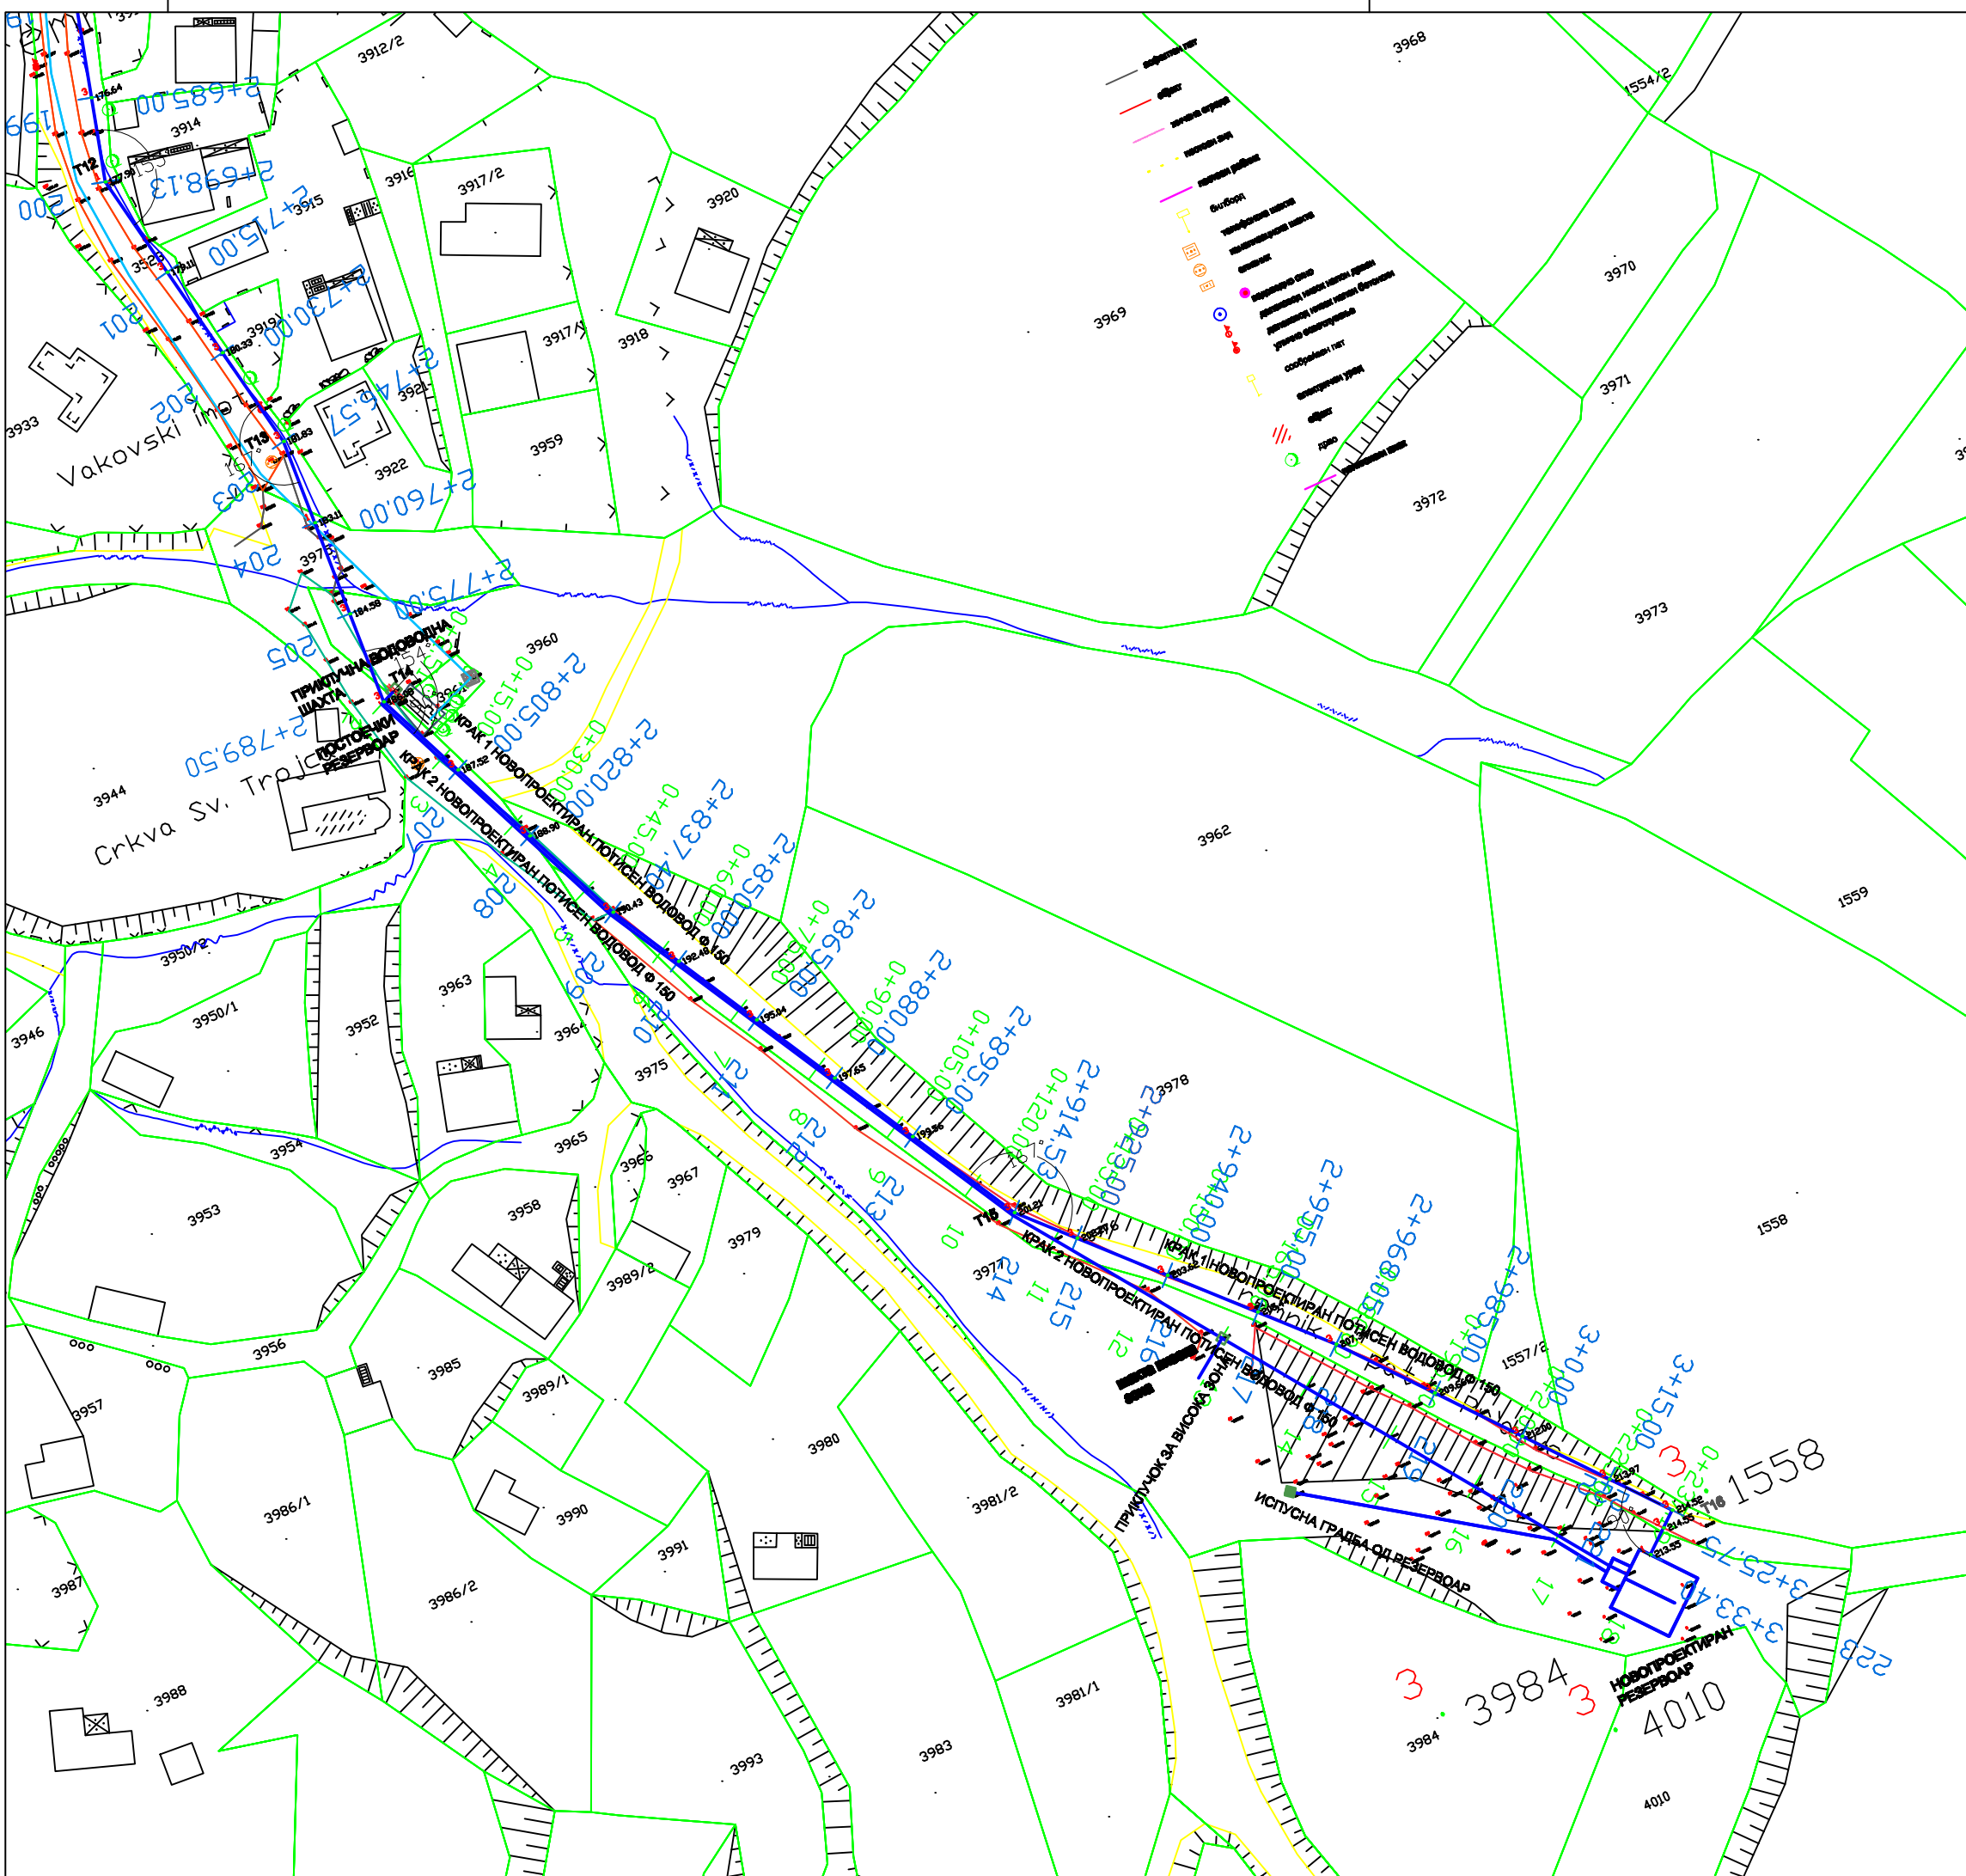

Ревизија		Забелешки	
Дата		М.П.	
Проектант: ЕуроРад Дизајн Груп дОО Скопје www.euro-rad-design-group.com			
Инвеститор: Општина Неготино		ЕURO ROAD DESIGN GROUP design, revision and consulting	
Проект: Основен проект за потисен цевковод и резервоар за вода за пиење во с. Треник Општина Неготино			
Цртач: Ситуација со хоризонтално решение (пр. 215-пр. 223)			
Одговорен проектант: Слаѓан Стојановски, дипл.град.инж. бр.на овластување А 2.1713			
Соработници: Билјана Стојановска, дипл.град.инж.			
технички број: ВК_321/2018		Број на лист: 13	
Вид на проект: водовод и канализација		Вкупно листови: 35	
Формат: А3(297mm-420mm)		Размер: 1:1000	
Датум, место:		Септември 2018, Скопје	

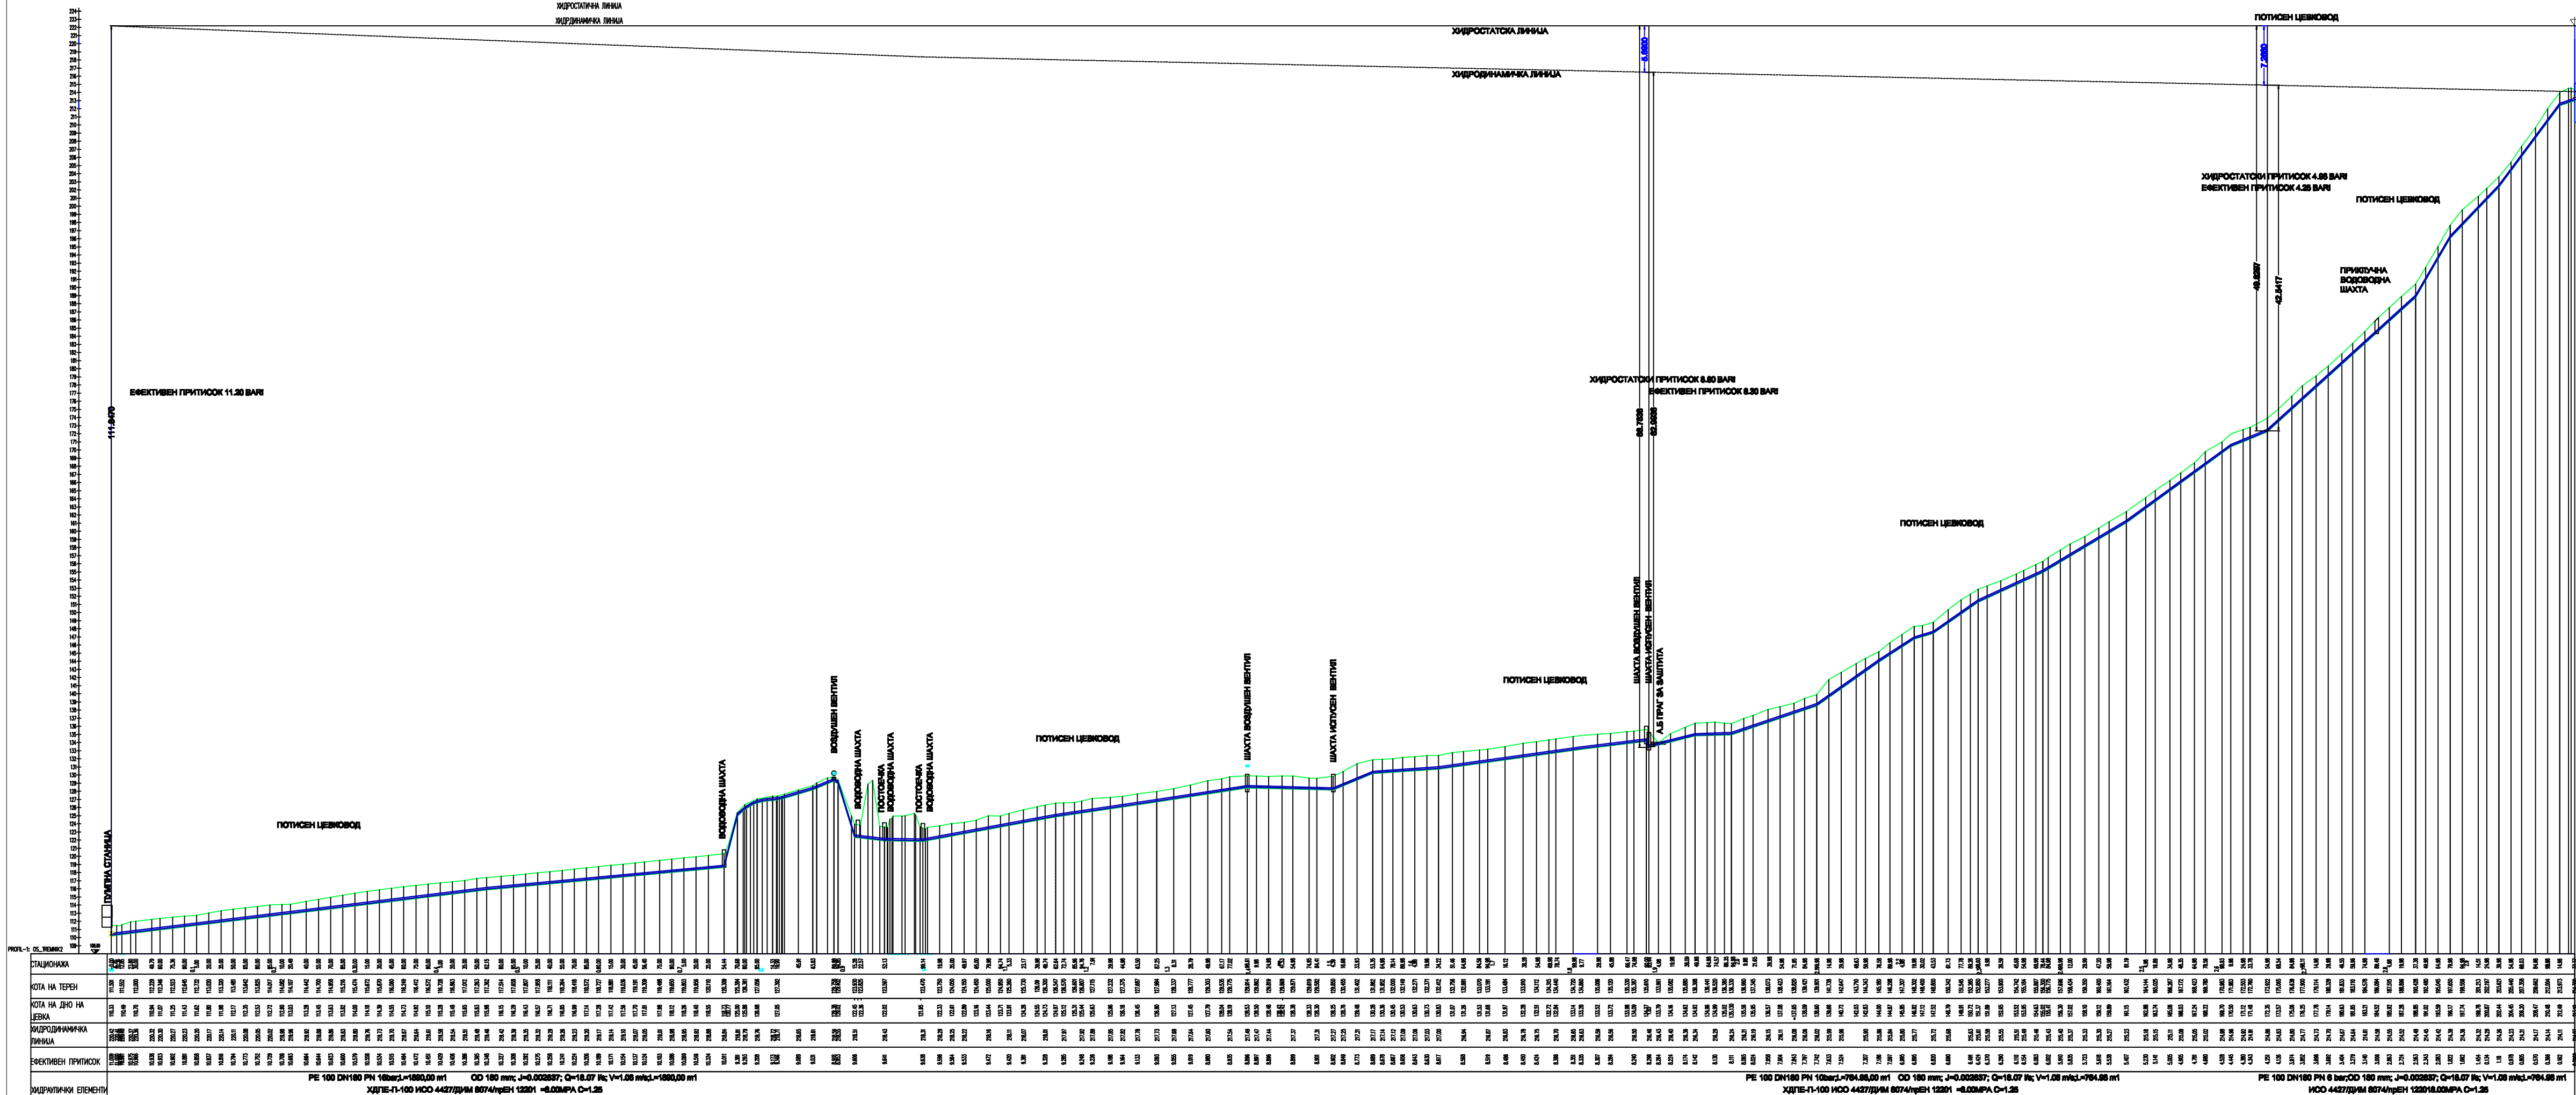





РЕЗЕРВОАР




ОСНОВА - нота 210.11/209.81 mNV

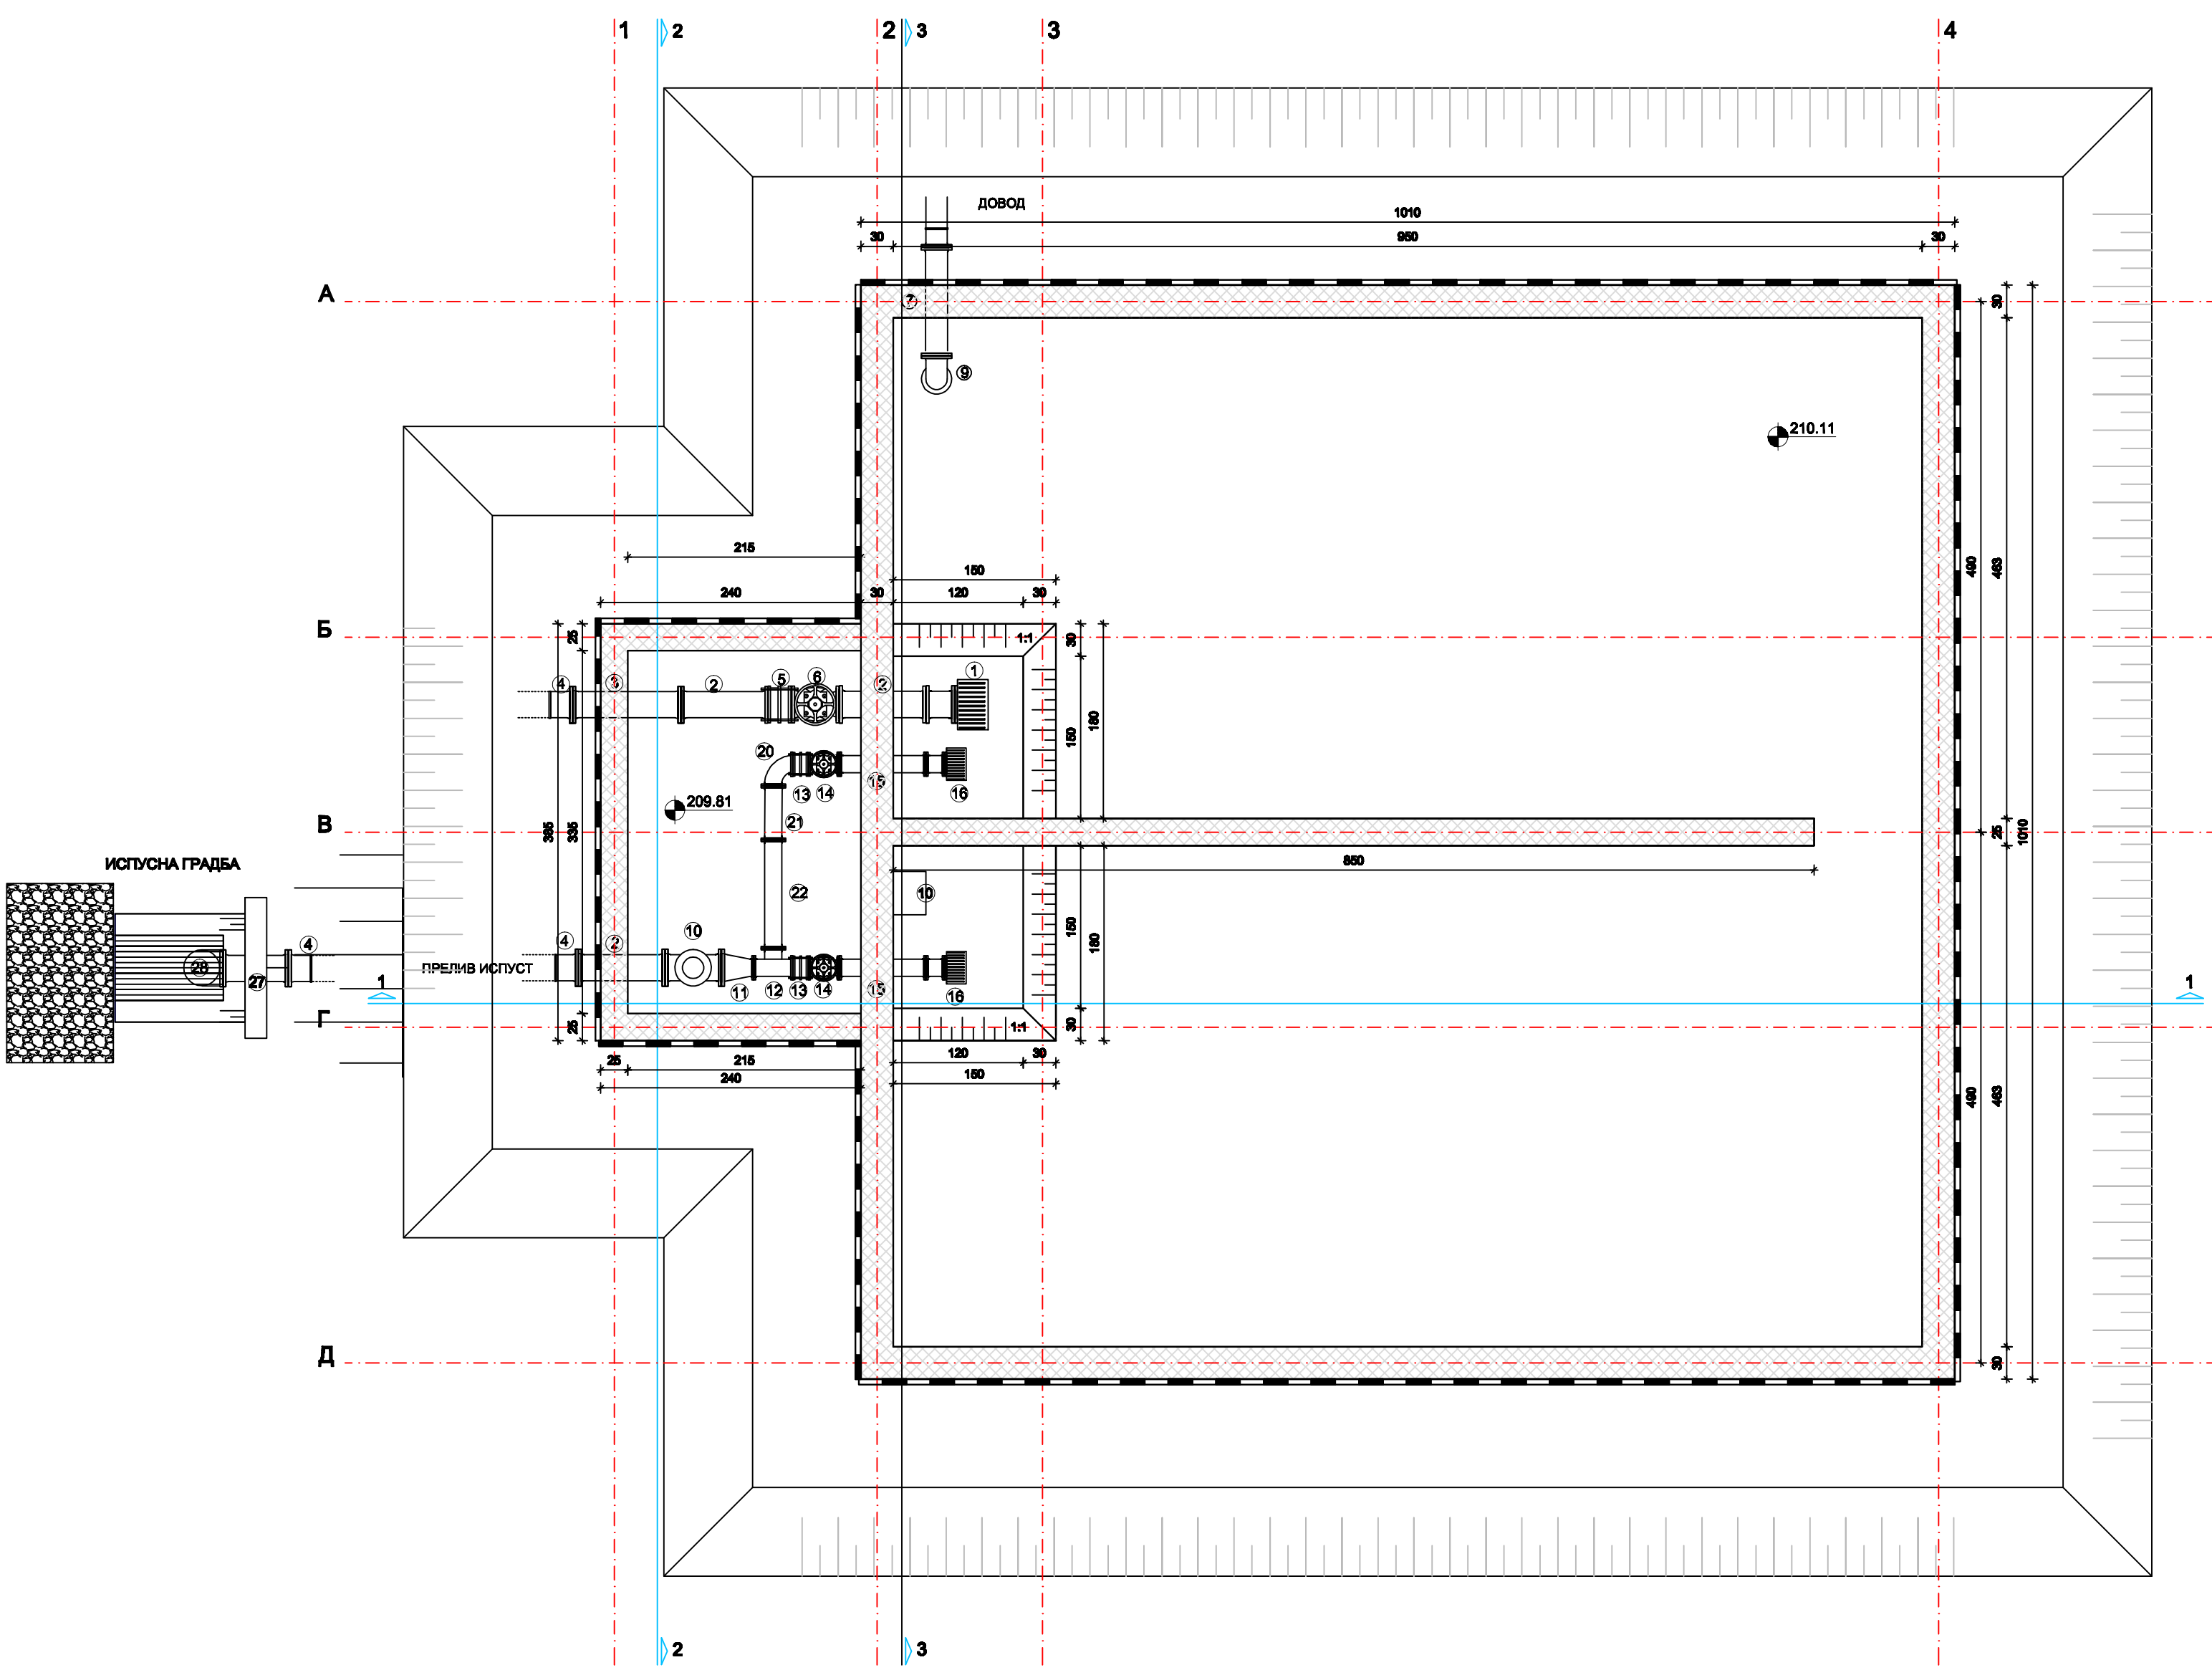


ОСНОВА - нота 213.71mNV

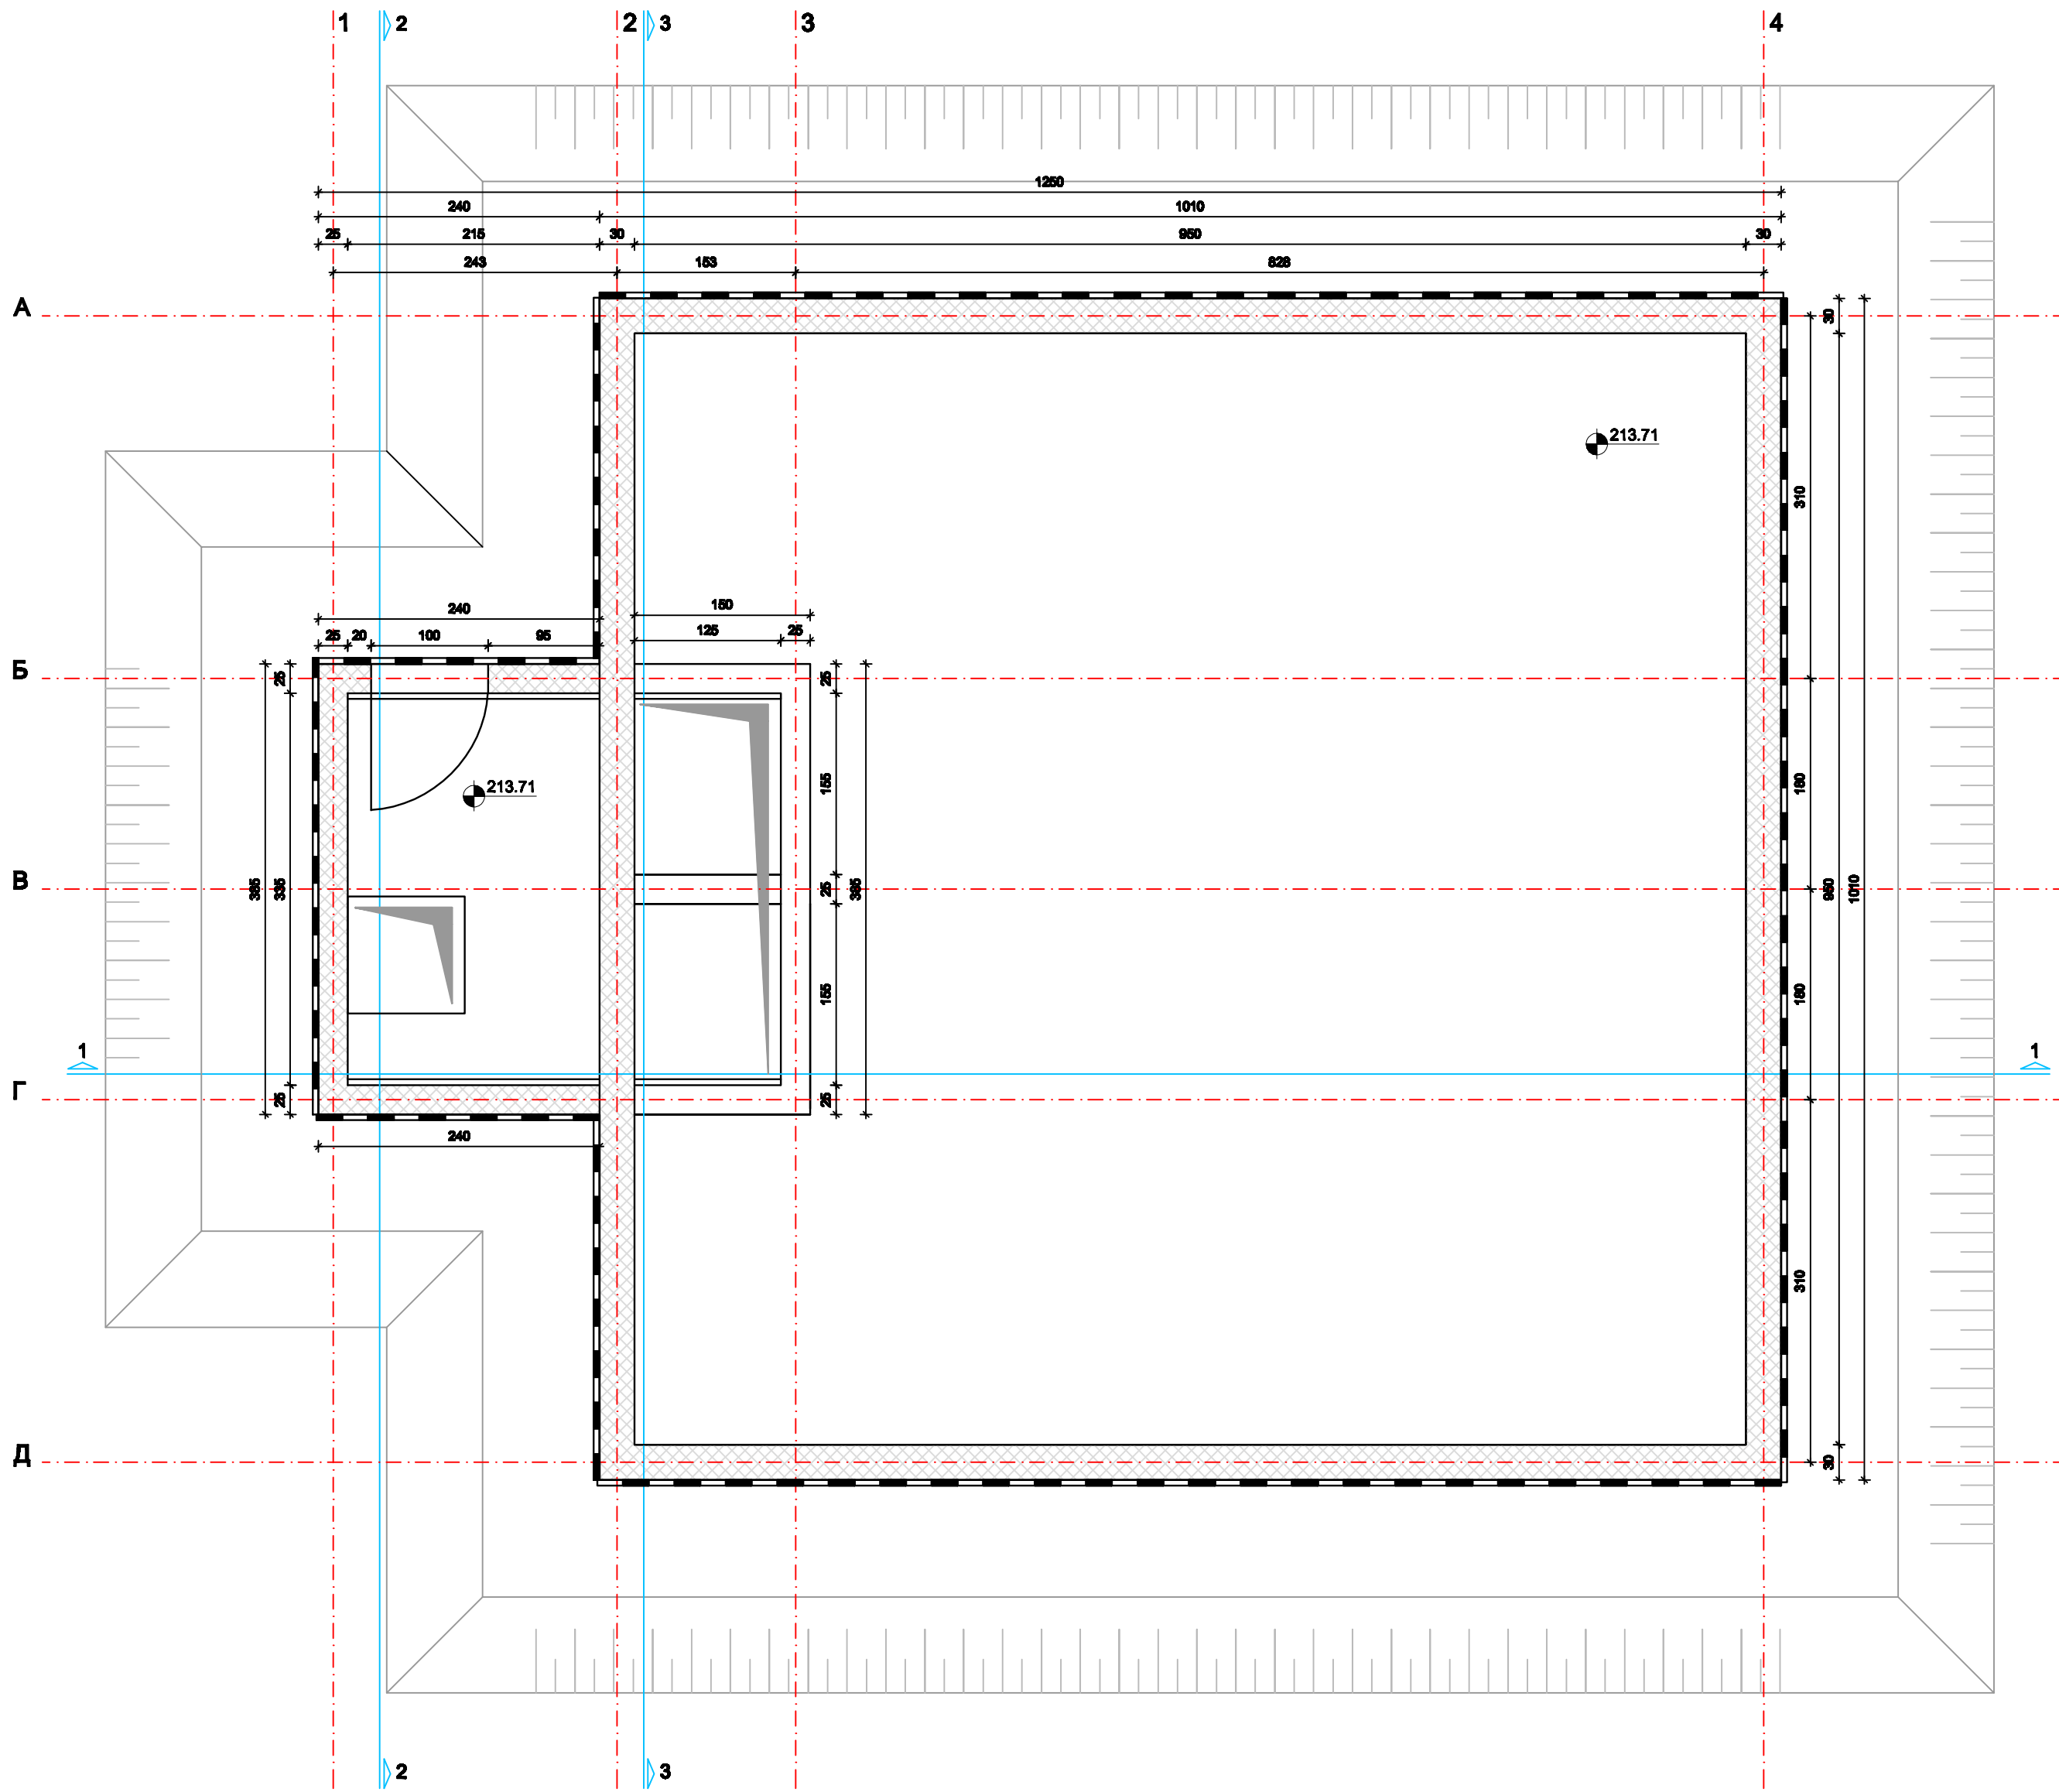


ПРЕСЕК 3-3

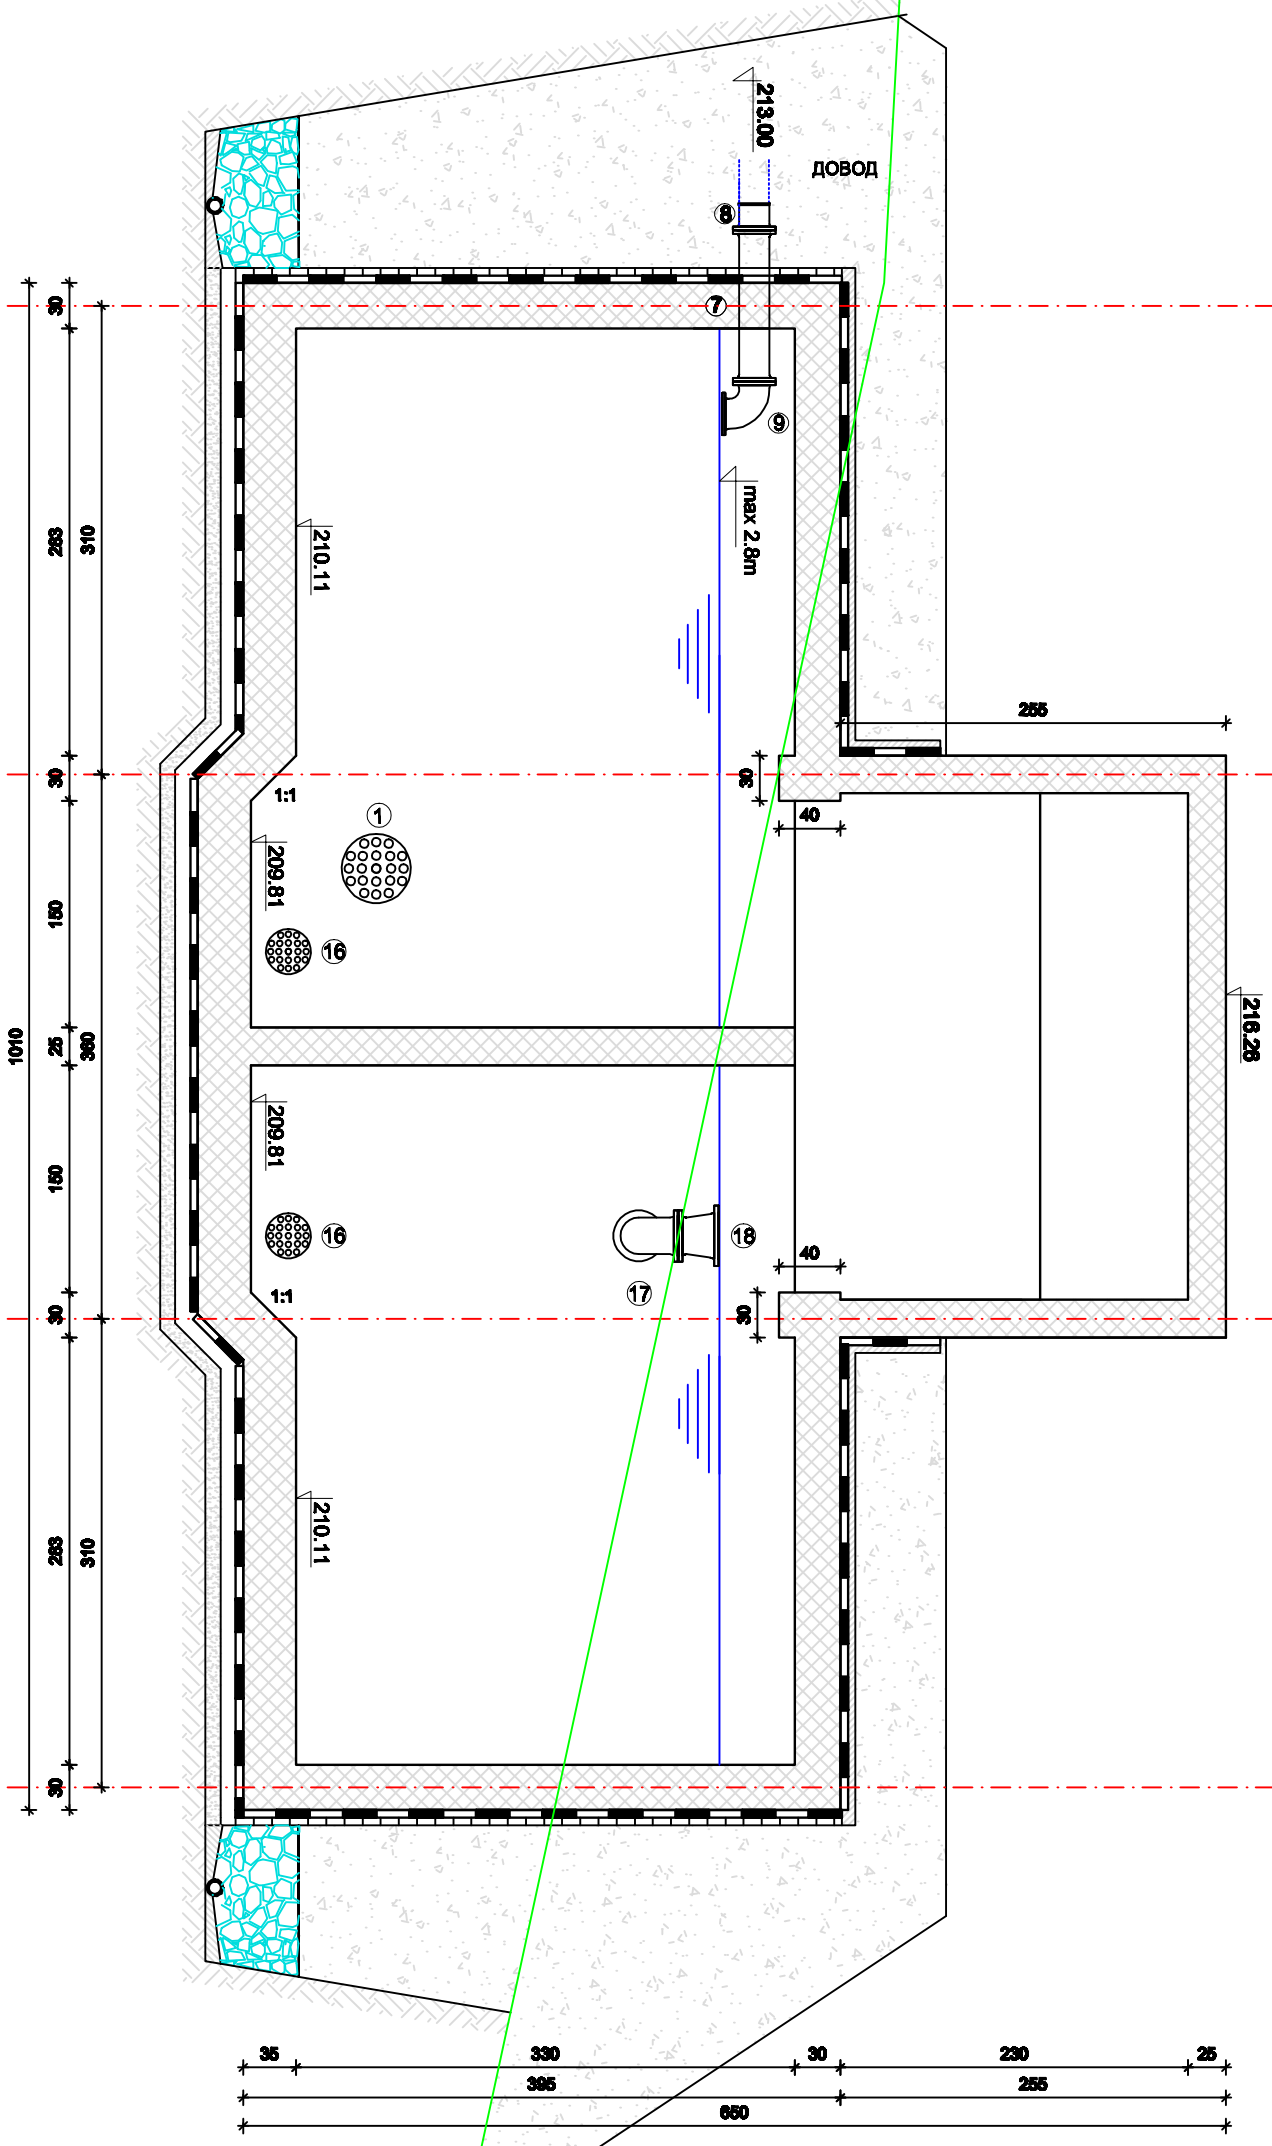

ПРЕСЕК 2-2

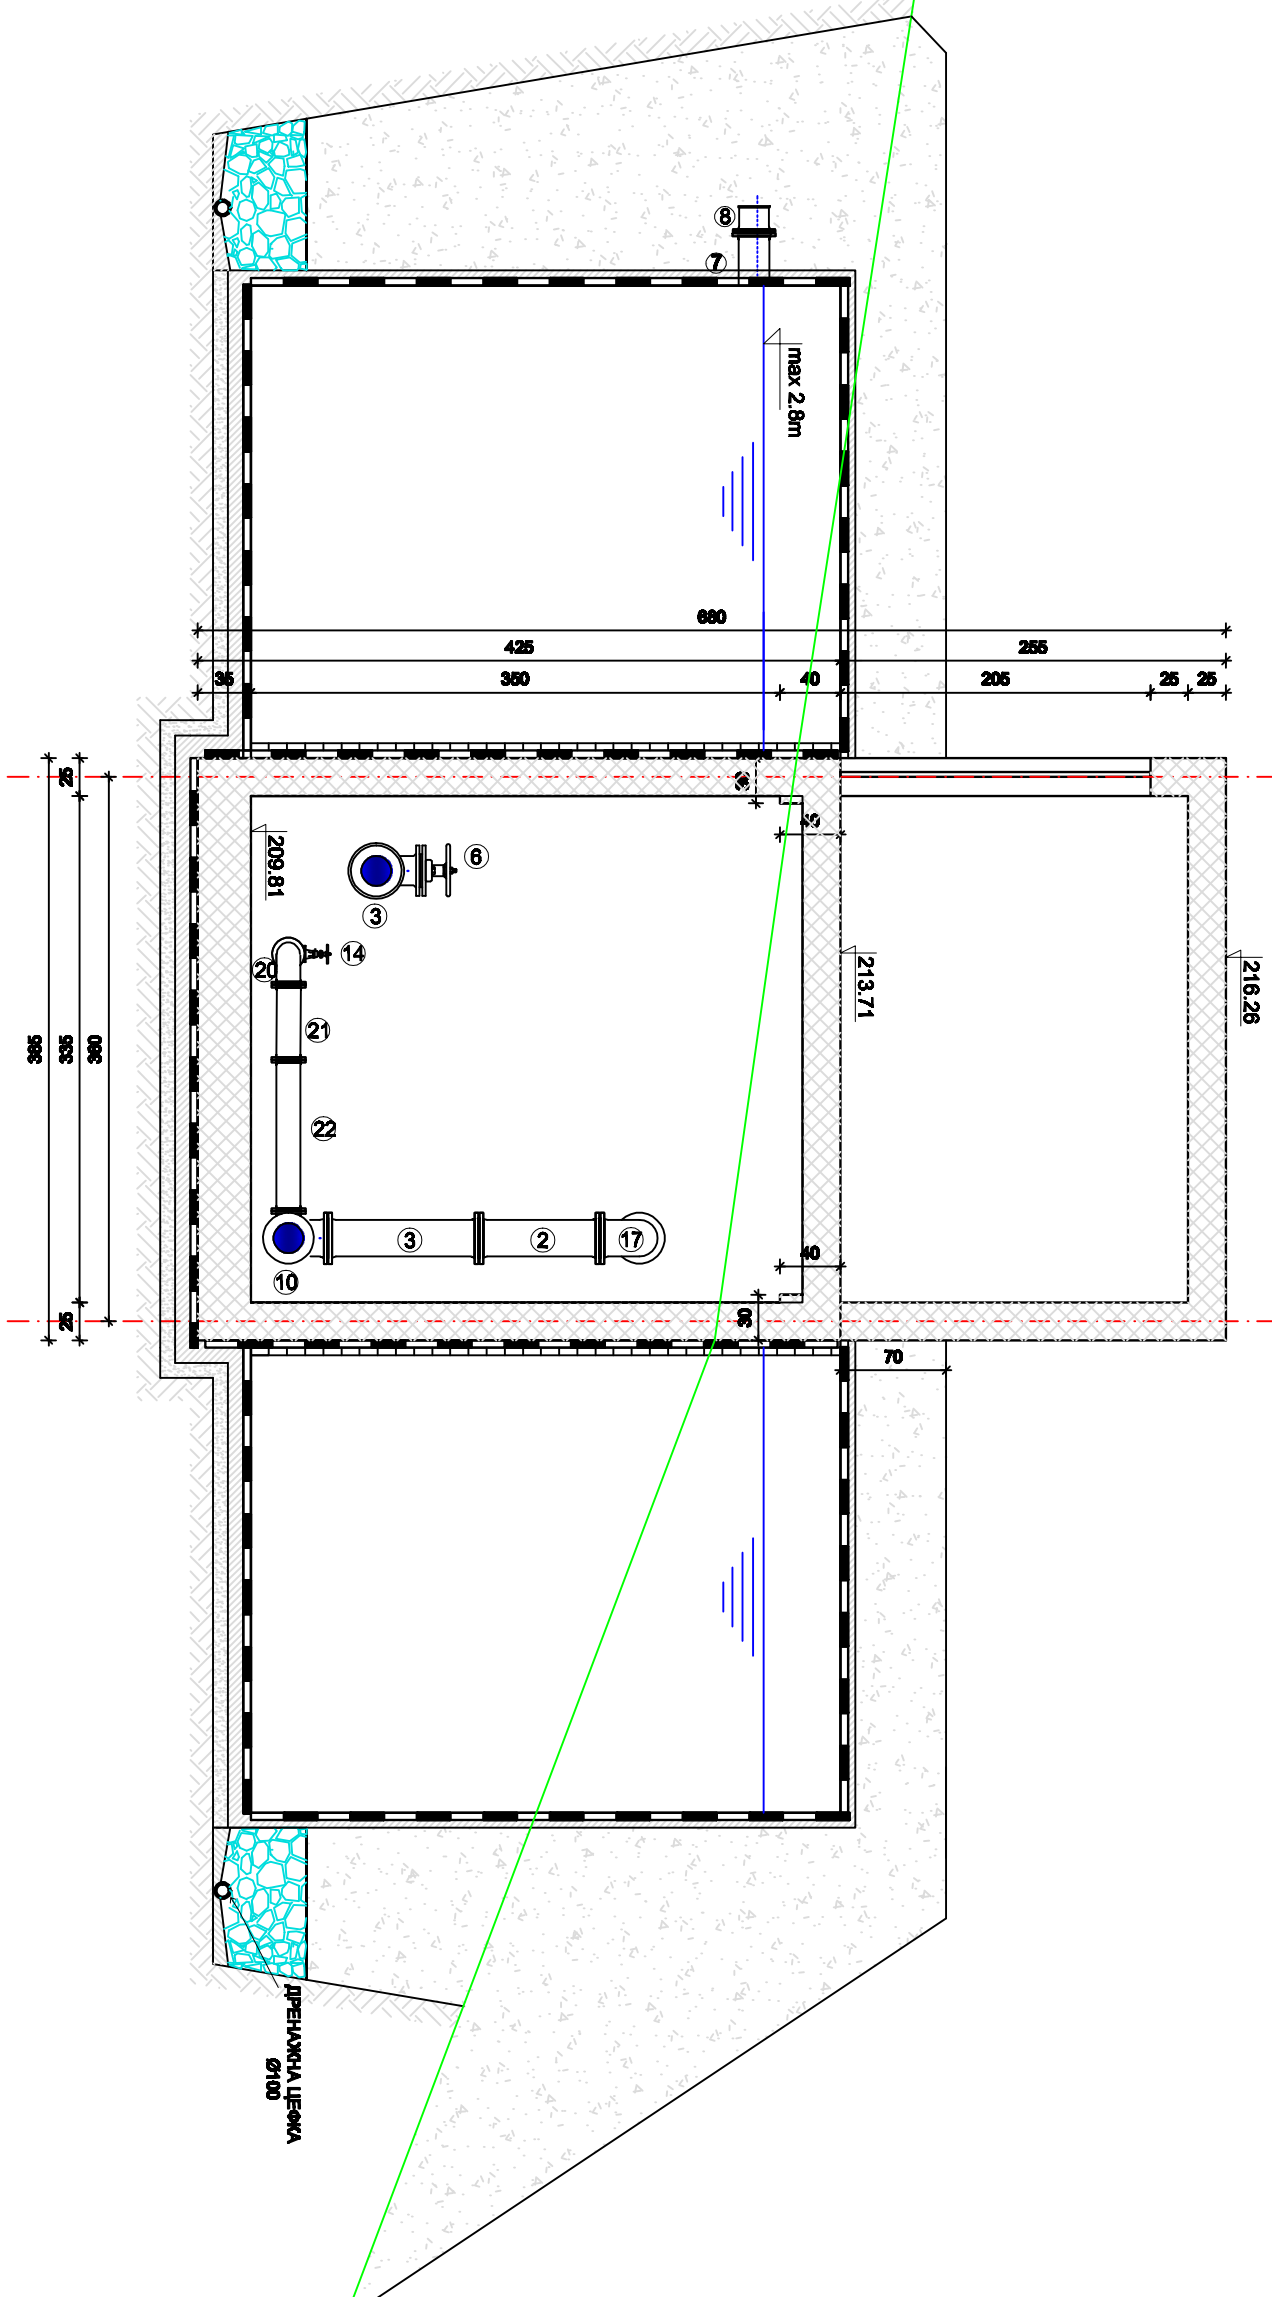

ПРЕСЕК 1-1

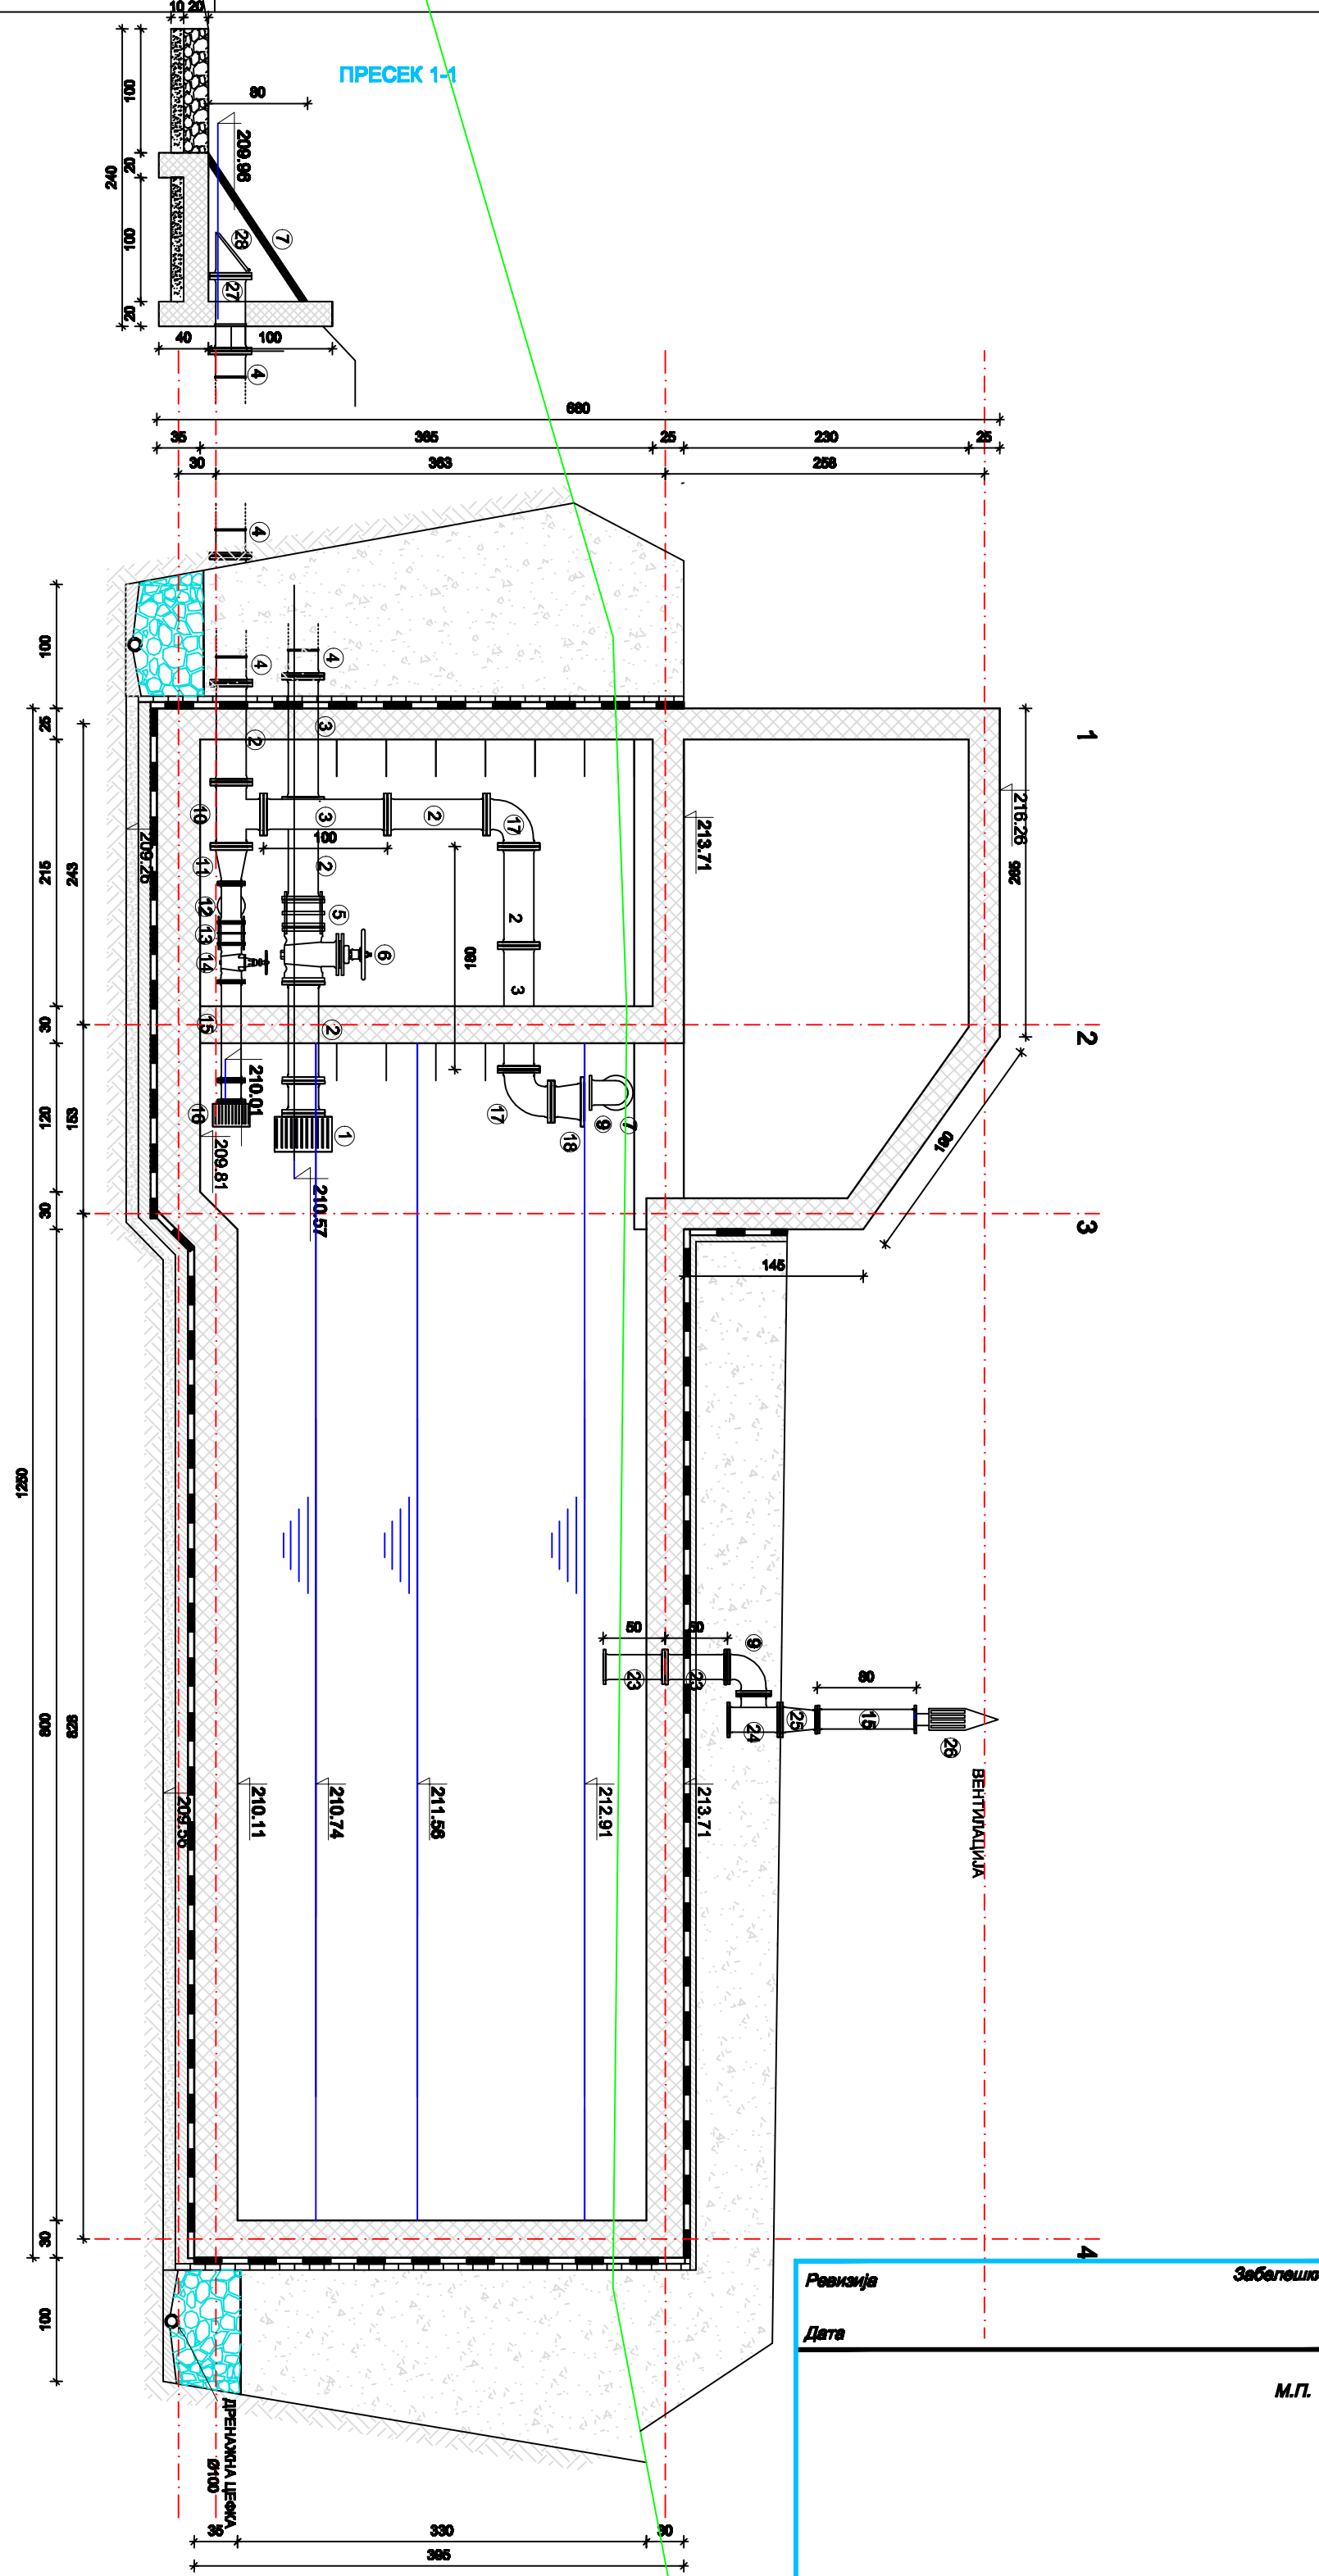

СПЕЦИФИКАЦИЈА НА ФАСОНСКИ ДЕЛОВИ И АРМАТУРИ

п.б	ИСПУСНА ГРАДБА ОЗНАКА	Ø [mm]	КОМ.	п.б	ДОВОД ОЗНАКА	Ø [mm]	КОМ.
4	адаптер спој со фланша	225	1	7	FF L= 600	150	1
27	FF L= 600	200	1	8	адаптер спој со фланша	180	1
28	ЖАВЕН ПОКЛОП.	200	1	9	N 90°	150	1
п.б	ВЕНТИЛАЦИЈА ОЗНАКА	Ø [mm]	КОМ.	п.б	ПРЕЛИВ ИСПУСТ ОЗНАКА	Ø [mm]	КОМ.
24	T 150/150	150/150	1	18	H FFR 250/200	250/200	1
23	FF L= 500	150	2	17	N 90°	200	2
15	FF L= 800	100	1	3	FF L= 1000	200	2
9	N 90°	150	1	2	FF L= 800	200	3
25	H FFR 150/100	150/100	1	10	T	200/200	1
26	ВЕН. КАПА	100	1	4	адаптер спој со фланша	225	1
п.б	ОДВОД ОЗНАКА	Ø [mm]	КОМ.	11	H FFR 200/100	200/100	1
1	уоксна корпа	200	1	12	T	100/100	1
2	FF L= 600	200	2	13	МОНТАЖНО ДЕМЛАЧЕ	100	2
3	FF L= 1000	250	1	14	OZ	100	2
4	адаптер спој со фланша	225	1	15	FF L= 800	100	2
5	МОНТАЖНО ДЕМЛАЧЕ	200	1	16	уоксна корпа	100	1
6	OZ	200	1	22	FF L= 1000	100	1
				21	FF L= 500	100	1
				20	N 90°	100	1

Ревизија	Забелешка
Дата	М.П.
Проектант: ЕуроРоад Дизајн Груп www.euroroad-design.com	
Инвеститор: Општина Неготино	
Проект: Основан проект за потисан цевковод и резервоар за вода за пиење во с. Треник, Општина Неготино	
Цртач: Основан и прелив со фасонски делови и арматури во резервоар	
Одговорен проектант: Слава Стојановски, д.г.и. Број на овластување А 2.1713	
Соработник: Билјана Стојановска, д.г.и.	
Технички број: ВК_32/2018	Број на лист: 02
Вид на проект: мозаик и монтажна	Вкупно листови: 07
Формат: A3 (840mmx1189mm)	Размер: 1:50
Дата, место	Септември 2018, Скопје